


# TWO TREES MANAGEMENT

		<b>PROJECT:</b>	DOMINO SITE E	# 16001	REVISION HISTORY		
		ADDRESS: DOMINO SITE E, BROOKLYN, NY		CONTACT: T. ROBINSON - (917) 589-7828	REV	DESCRIPTION	
		<b>ITEM:</b>		FACADE			
		<b>RELEASE NAME:</b>		16001_ZINC PANEL TYPES			
		<b>ISSUE DATE:</b>		7/28/2016	REVISION	A	
		<b>DRAWN:</b>		CHECKED:	<b>PROJECT MANAGER:</b>		
		SP			TR		
<b>CONTRACTOR</b>		325 KENT CONSTRUCTION LLC	<b>ARCHITECT</b>	ISMAEL LEYVA	<b>FLAT FILE LOCATION:</b>		
		<u>HI-TECH METALS, MFG LLC</u> <u>ARCHITECTURAL METAL FABRICATION</u> 59-20 56TH AVE. MASPETH, NY 11378 (718) 894-1212		<b>PRODUCTION DEPT.</b>		<b>SHOP MANAGER:</b>	
				<u>COMPLETED DATE:</u> _____ <u>SHIPPED DATE:</u> _____ <u>CHECKED BY:</u> _____ <u>PACKING SLIP:</u> _____ <u>INITIAL:</u> _____ <u>INITIAL:</u> _____			

**NOTES:**

SUBMITTED FOR APPROVAL, 7-26-16  
 REVISED & SUBMITTED FOR RECORD, 9-2-16


# ZINC PERFORATED PANEL TYPES TYPICAL FLOORS

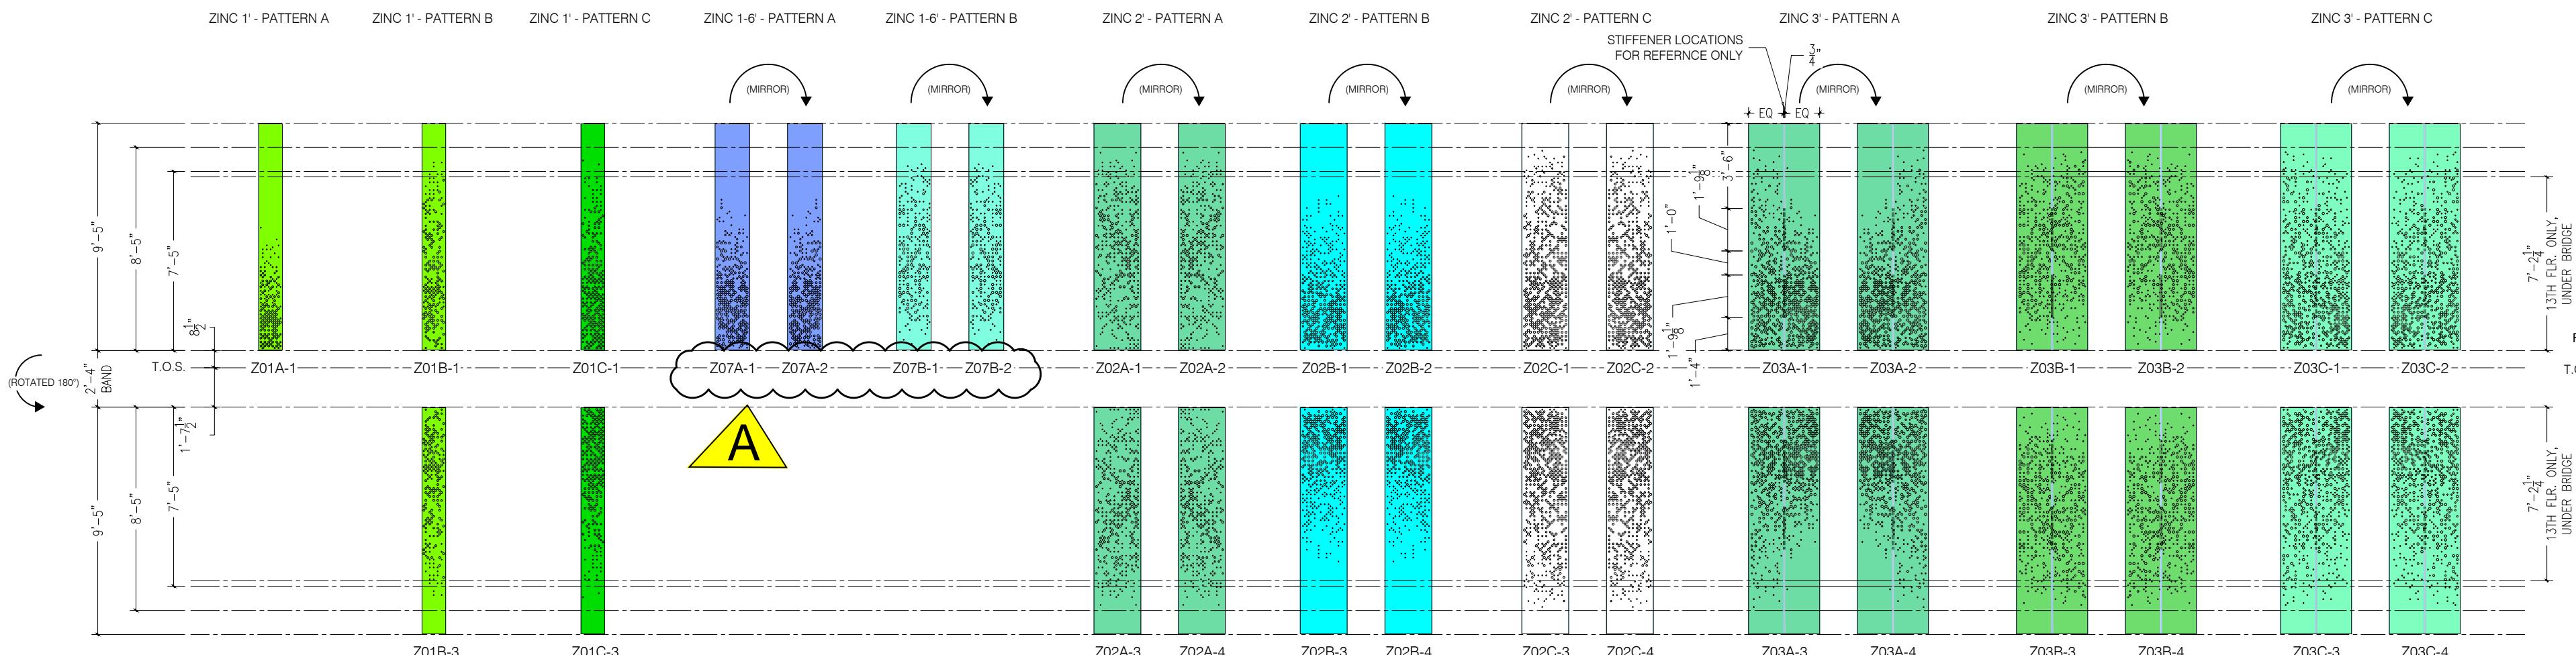

NOTES:

- 1) UNLESS NOTED AS "ACTUAL" ALL DIMENSIONS NOTED ARE CENTERLINE, NOMINAL PANEL DIMENSIONS (CENTERLINES DEMARCADE 3/4" REVEAL JOINT).
- 2) ALL "FLEX" PANELS MARKED ON ELEVATIONS, CUT DOWN FROM TYPICAL PERFORATION PATTERNS (LEAVING 3/4" SOLID BORDER AND RE-CENTERED ON FINAL PANEL WIDTH)


## ATYPICAL FLOORS

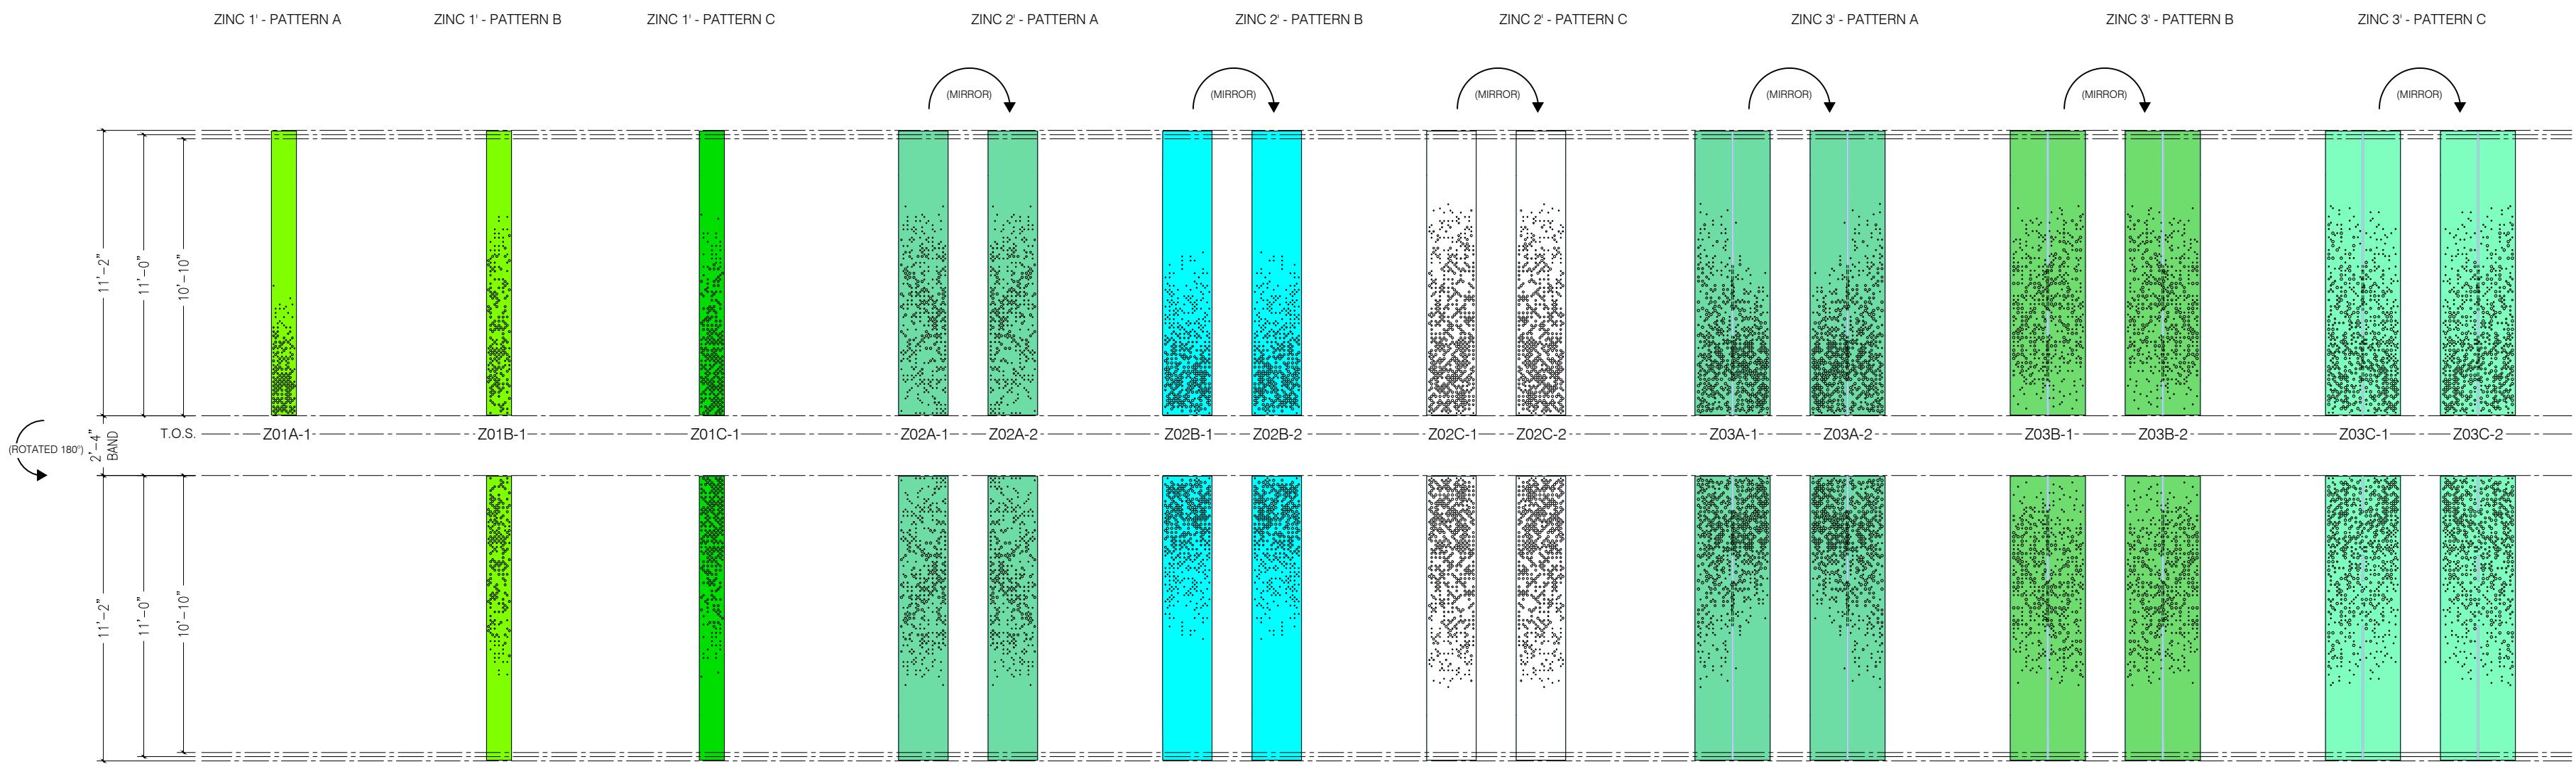

NOTES:

- 1) UNLESS NOTED AS "ACTUAL" ALL DIMENSIONS NOTED ARE CENTERLINE, NOMINAL PANEL DIMENSIONS (CENTERLINES DEMARcate 3/4" REVEAL JOINT).
- 2) ALL "FLEX" PANELS MARKED ON ELEVATIONS, CUT DOWN FROM TYPICAL PERFORATION PATTERNS (LEAVING 3/4" SOLID BORDER AND RE-CENTERED ON FINAL PANEL WIDTH)


MISC. PANELS

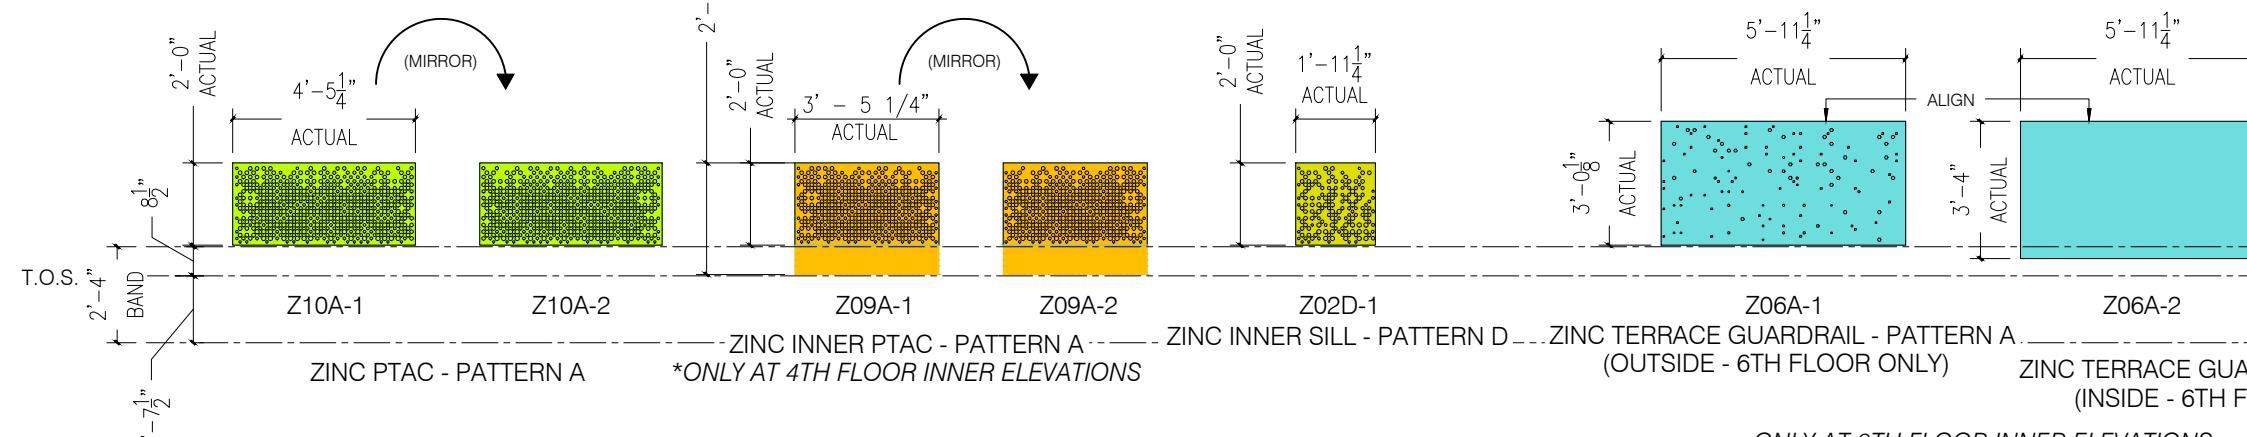

NOTES:

- 1) UNLESS NOTED AS "ACTUAL" ALL DIMENSIONS NOTED ARE CENTERLINE, NOMINAL PANEL DIMENSIONS (CENTERLINES DEMARcate 3/4" REVEAL JOINT).
- 2) ALL "FLEX" PANELS MARKED ON ELEVATIONS, CUT DOWN FROM TYPICAL PERFORATION PATTERNS (LEAVING 3/4" SOLID BORDER AND RE-CENTERED ON FINAL PANEL WIDTH)

## RECEPTACLE/LIGHT PANELS

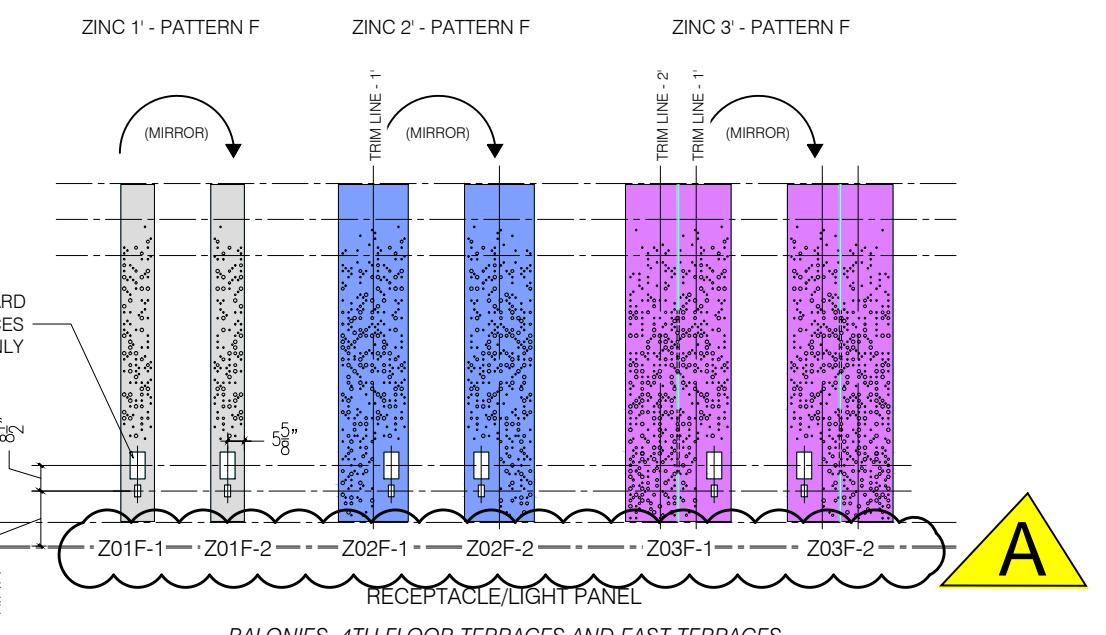

**RECEIPT PLACE/EIGHTY FIVE**


## NOTES:

## **CONTRACT NOTES:**

**HI-TECH METALS WILL NOT BE  
RESPONSIBLE FOR ANY  
MEASUREMENTS OR DETAILS AFFECTING  
OTHER WORK EXCEPT OUR OWN, OR ANY  
ERRORS OCCURRING DUE TO THE USE OF  
THESE DRAWINGS BY OTHER PARTIES**

**NO PART OF THESE DRAWINGS MAY BE  
REPRODUCED IN ANY FORM WITHOUT THE  
EXPRESSED PERMISSION OF HI TECH**

**GENERAL CONTRACTOR AND/OR  
ARCHITECT'S APPROVAL OF ALL  
DIMENSIONS AND DETAILS IS REQUIRED  
PRIOR TO FABRICATION**

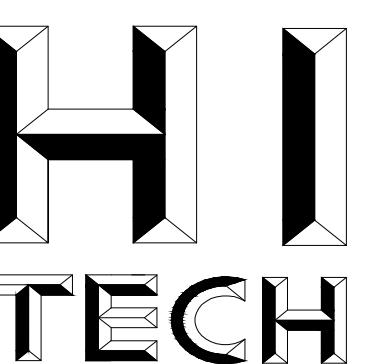

ARCHITECTURAL METAL FABRICATION

59-20 56th AVENUE  
MASPETH, N.Y. 11378

HONE (718) 894-1212

(800) 394-2712

Customer:  
**TWO TREES MANAGEMENT Co.**  
**45 MAIN STREET, SUITE 602**  
**BROOKLYN, NY 11201**

Architect  
**ISMAEL LEYVA ARCHITECTS P.C.**  
48 WEST 37 STREET, NEW YORK, NY 10018

# Project **DOMINO SITE E BUILDING**

BROOKLYN, NY

---

Drawn by Date

Scale:	Job Number
NOT	<b>16001</b>

SHEET #	NEW <b>S-1</b>	REVISION <b>A</b>
---------	-------------------	----------------------

## Z000 NON-PERFORATED VERTICAL PANEL TABLE

PANEL ID	PANEL TYPE	BEND PROFILE	WIDTH (IN)	HEIGHT (IN)	PANEL TYPE (QTY)
Z000-1-021	VERTICAL	TYPE 1	11.625	100.25	2
Z000-1-026	VERTICAL	TYPE 1	23.25	108.125	35
Z000-1-027	VERTICAL	TYPE 1	15.25	108.125	2
Z000-1-028	VERTICAL	TYPE 1	35.25	108.125	39
Z000-1-029	VERTICAL	TYPE 1	23.625	108.125	9
Z000-1-030	VERTICAL	TYPE 1	11.25	108.125	38
Z000-1-031	VERTICAL	TYPE 1	24.75	108.125	1
Z000-1-032	VERTICAL	TYPE 1	12.75	108.125	3
Z000-1-033	VERTICAL	TYPE 1	13.75	108.125	2
Z000-1-034	VERTICAL	TYPE 1	18.75	108.125	1
Z000-1-035	VERTICAL	TYPE 1	35.625	108.125	2
Z000-1-068	VERTICAL	TYPE 1	24.125	108.125	1
Z000-1-070	VERTICAL	TYPE 1	10.125	108.125	1
Z000-1-071	VERTICAL	TYPE 1	16.8125	108.125	1
Z000-1-193	VERTICAL	TYPE 1	18	108.125	1
Z000-1-194	VERTICAL	TYPE 1	21.75	108.125	1
Z000-1-195	VERTICAL	TYPE 1	11.625	108.125	3
Z000-1-196	VERTICAL	TYPE 1	27.75	108.125	1
Z000-1-197	VERTICAL	TYPE 1	32.25	108.125	1
Z000-1-198	VERTICAL	TYPE 1	17.75	108.125	1
Z000-1-199	VERTICAL	TYPE 1	17.25	108.125	3
Z000-1-200	VERTICAL	TYPE 1	17.625	100.25	1
Z000-1-201	VERTICAL	TYPE 1	23.25	100.25	1
Z000-1-202	VERTICAL	TYPE 1	28.25	100.25	1
Z000-1-225	VERTICAL	TYPE 1	13.25	108.125	1
Z000-1-226	VERTICAL	TYPE 1	21.25	108.125	2
Z000-1-227	VERTICAL	TYPE 1	15.75	108.125	2
Z000-1-228	VERTICAL	TYPE 1	26.25	108.125	1
Z000-1-229	VERTICAL	TYPE 1	10	108.125	1
Z000-1-230	VERTICAL	TYPE 1	22.625	108.125	1
Z000-1-231	VERTICAL	TYPE 1	21	108.125	1
Z000-1-334	VERTICAL	TYPE 1	11.25	7.125	1
Z000-1-336	VERTICAL	TYPE 1	13	108.125	1
Z000-1-337	VERTICAL	TYPE 1	31.25	108.125	1
Z000-1-338	VERTICAL	TYPE 1	21.625	108.125	1
Z000-1-339	VERTICAL	TYPE 1	22.5	108.125	1
Z000-1-355	VERTICAL	TYPE 1	19.75	108.125	1
Z000-1-356	VERTICAL	TYPE 1	21.9375	108.125	1
Z000-1-357	VERTICAL	TYPE 1	24.5625	108.125	1
Z000-1-358	VERTICAL	TYPE 1	24.5	108.125	1
Z000-1-391	VERTICAL	TYPE 1	20	120.125	1
Z000-1-392	VERTICAL	TYPE 1	23.25	120.125	1
Z000-1-393	VERTICAL	TYPE 1	35.25	120.125	2
Z000-1-394	VERTICAL	TYPE 1	11.25	120.125	3
Z000-1-395	VERTICAL	TYPE 1	27.875	120.125	1
Z000-1-396	VERTICAL	TYPE 1	23.75	120.125	1
Z000-1-397	VERTICAL	TYPE 1	15.25	120.125	1
Z000-1-398	VERTICAL	TYPE 1	23.625	120.125	1
Z000-1-399	VERTICAL	TYPE 1	35.625	120.125	1
Z000-1-400	VERTICAL	TYPE 1	19.5	120.125	1
Z000-1-438	VERTICAL	TYPE 1	29.75	108.125	1
Z000-1-439	VERTICAL	TYPE 1	23	108.125	1

PANEL ID	PANEL TYPE	BEND PROFILE	WIDTH (IN)	HEIGHT (IN)	PANEL TYPE (QTY)
Z000-1-441	VERTICAL	TYPE 1	17	108.125	1
Z000-1-476	VERTICAL	TYPE 1	19.25	108.125	3
Z000-1-477	VERTICAL	TYPE 1	10.75	108.125	1
Z000-1-478	VERTICAL	TYPE 1	26.375	108.125	1
Z000-1-500	VERTICAL	TYPE 1	11.25	133.75	8
Z000-1-501	VERTICAL	TYPE 1	23.25	133.75	16
Z000-1-502	VERTICAL	TYPE 1	35.25	133.75	10
Z000-1-503	VERTICAL	TYPE 1	13.3125	133.75	1
Z000-1-505	VERTICAL	TYPE 1	22.75	133.75	1
Z000-1-506	VERTICAL	TYPE 1	20.25	133.75	1
Z000-1-507	VERTICAL	TYPE 1	38.125	133.75	1
Z000-1-508	VERTICAL	TYPE 1	28.25	133.75	1
Z000-1-509	VERTICAL	TYPE 1	19.4375	133.75	1
Z000-1-522	VERTICAL	TYPE 1	11.25	34.5	13
Z000-1-523	VERTICAL	TYPE 1	35.25	34.5	14
Z000-1-527	VERTICAL	TYPE 1	14.25	34.5	2
Z000-1-530	VERTICAL	TYPE 1	17.625	34.5	1
Z000-1-531	VERTICAL	TYPE 1	23.25	34.5	5
Z000-1-532	VERTICAL	TYPE 1	11.25	34.5	5
Z000-1-533	VERTICAL	TYPE 1	35.25	34.5	3
Z000-1-535	VERTICAL	TYPE 1	23.25	34.5	15
Z000-1-536	VERTICAL	TYPE 1	29	34.5	1
Z000-1-537	VERTICAL	TYPE 1	32.25	34.5	1
Z000-1-538	VERTICAL	TYPE 1	13.625	34.5	1
Z000-1-540	VERTICAL	TYPE 1	13.25	34.5	1
Z000-1-541	VERTICAL	TYPE 1	13.25	133.5	1
Z000-1-542	VERTICAL	TYPE 1	32.75	34.5	1
Z000-1-544	VERTICAL	TYPE 1	18.25	34.5	1
Z000-1-545	VERTICAL	TYPE 1	29.25	34.5	1
Z000-1-546	VERTICAL	TYPE 1	31	34.5	2
Z000-1-547	VERTICAL	TYPE 1	9.25	34.5	2
Z000-1-548	VERTICAL	TYPE 1	16.25	34.5	2
Z000-1-549	VERTICAL	TYPE 1	25.3125	34.5	1
Z000-1-550	VERTICAL	TYPE 1	27	34.5	1
Z000-1-552	VERTICAL	TYPE 1	37.25	34.5	1
Z000-1-553	VERTICAL	TYPE 1	35.25	34.5	1
Z000-1-554	VERTICAL	TYPE 1	15.25	34.5	1
Z000-1-555	VERTICAL	TYPE 1	23.625	34.5	1
Z000-1-556	VERTICAL	TYPE 1	21	34.5	1
Z000-1-557	VERTICAL	TYPE 1	24.25	34.5	1
Z000-1-612	VERTICAL	TYPE 1	35.25	34.5	1
Z000-1-614	VERTICAL	TYPE 1	23.25	34.5	1
Z000-1-615	VERTICAL	TYPE 1	39.25	38.625	2
Z000-1-616	VERTICAL	TYPE 1	21.75	38.625	4
Z000-1-617	VERTICAL	TYPE 1	38.75	38.625	2
PANEL TOTAL					320

## PANEL RAIL LAYOUT TABLE

PANEL HEIGHT (IN)	RAIL #
<= 11	1
> 11 AND <= 54.5	2
> 54.5 AND <= 102.5	3
> 102.5	4

REFER TO HTMI DETAIL S-5 TO S-10,  
FOR NV3 RAIL SET-OUT

**HI TECH**  
ARCHITECTURAL METAL FABRICATION  
59-20 56TH AVE.  
MASPETH, NY 11378  
(718) 894-1212

**CONTRACTOR**

325 KENT CONSTRUCTION LLC

**ARCHITECT**

ISMAEL LEYVA

**PROJECT #**

DOMINO SITE E

**ITEM**

FAÇADE

**DRAWING**


</div

## Z000 NON-PERFORATED VERTICAL PANEL


**Z000-1-030 (SHOWN)**




BACK VIEW

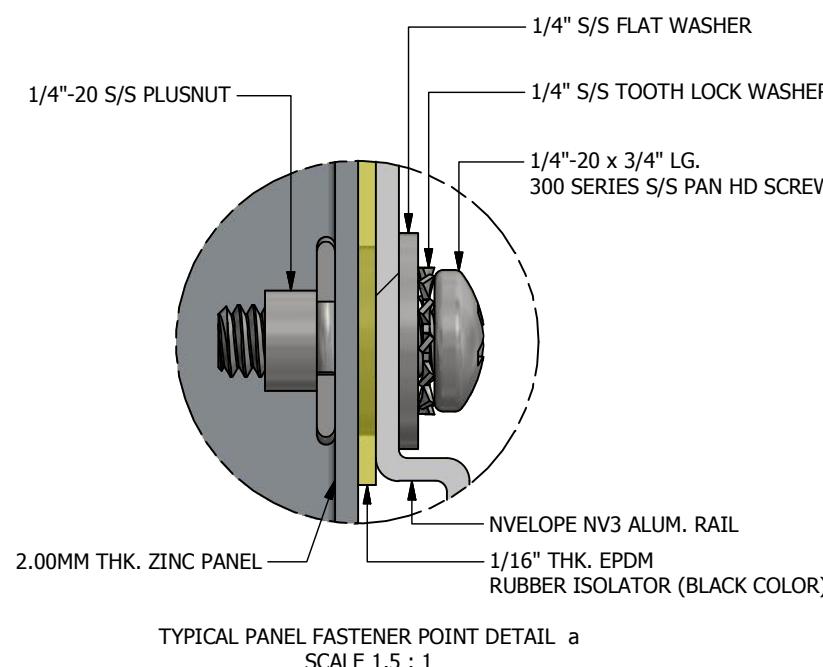


**TYPICAL PANEL FASTENER POINT DETAIL**  
**SCALE 1.5 : 1**

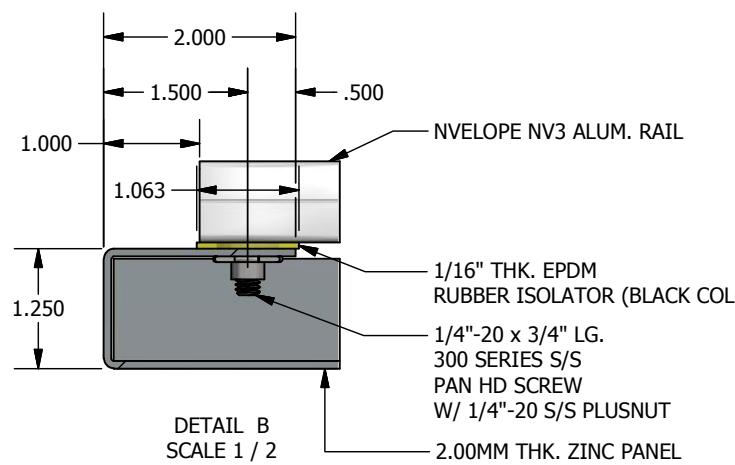

**STIFFENERS NOT SHOWN,  
REFER TO HTMI STIFFENER DETAIL**

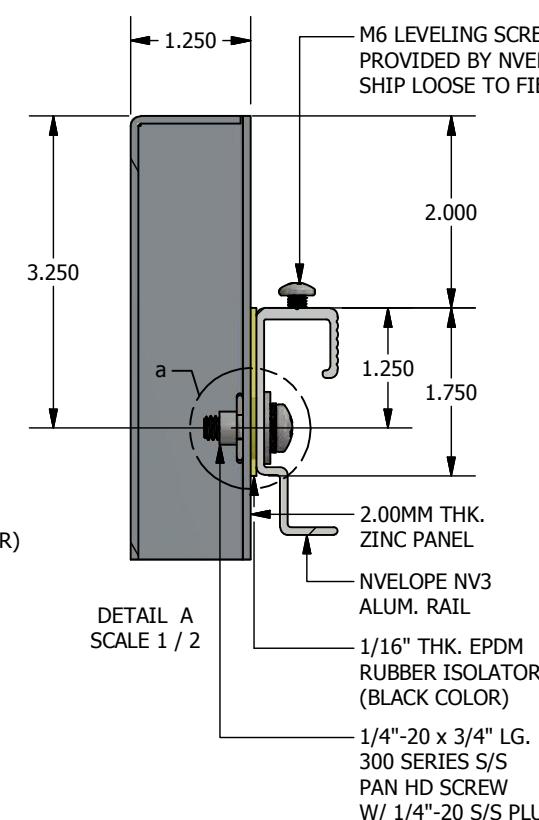

DETAIL A  
SCALE 1 / 2


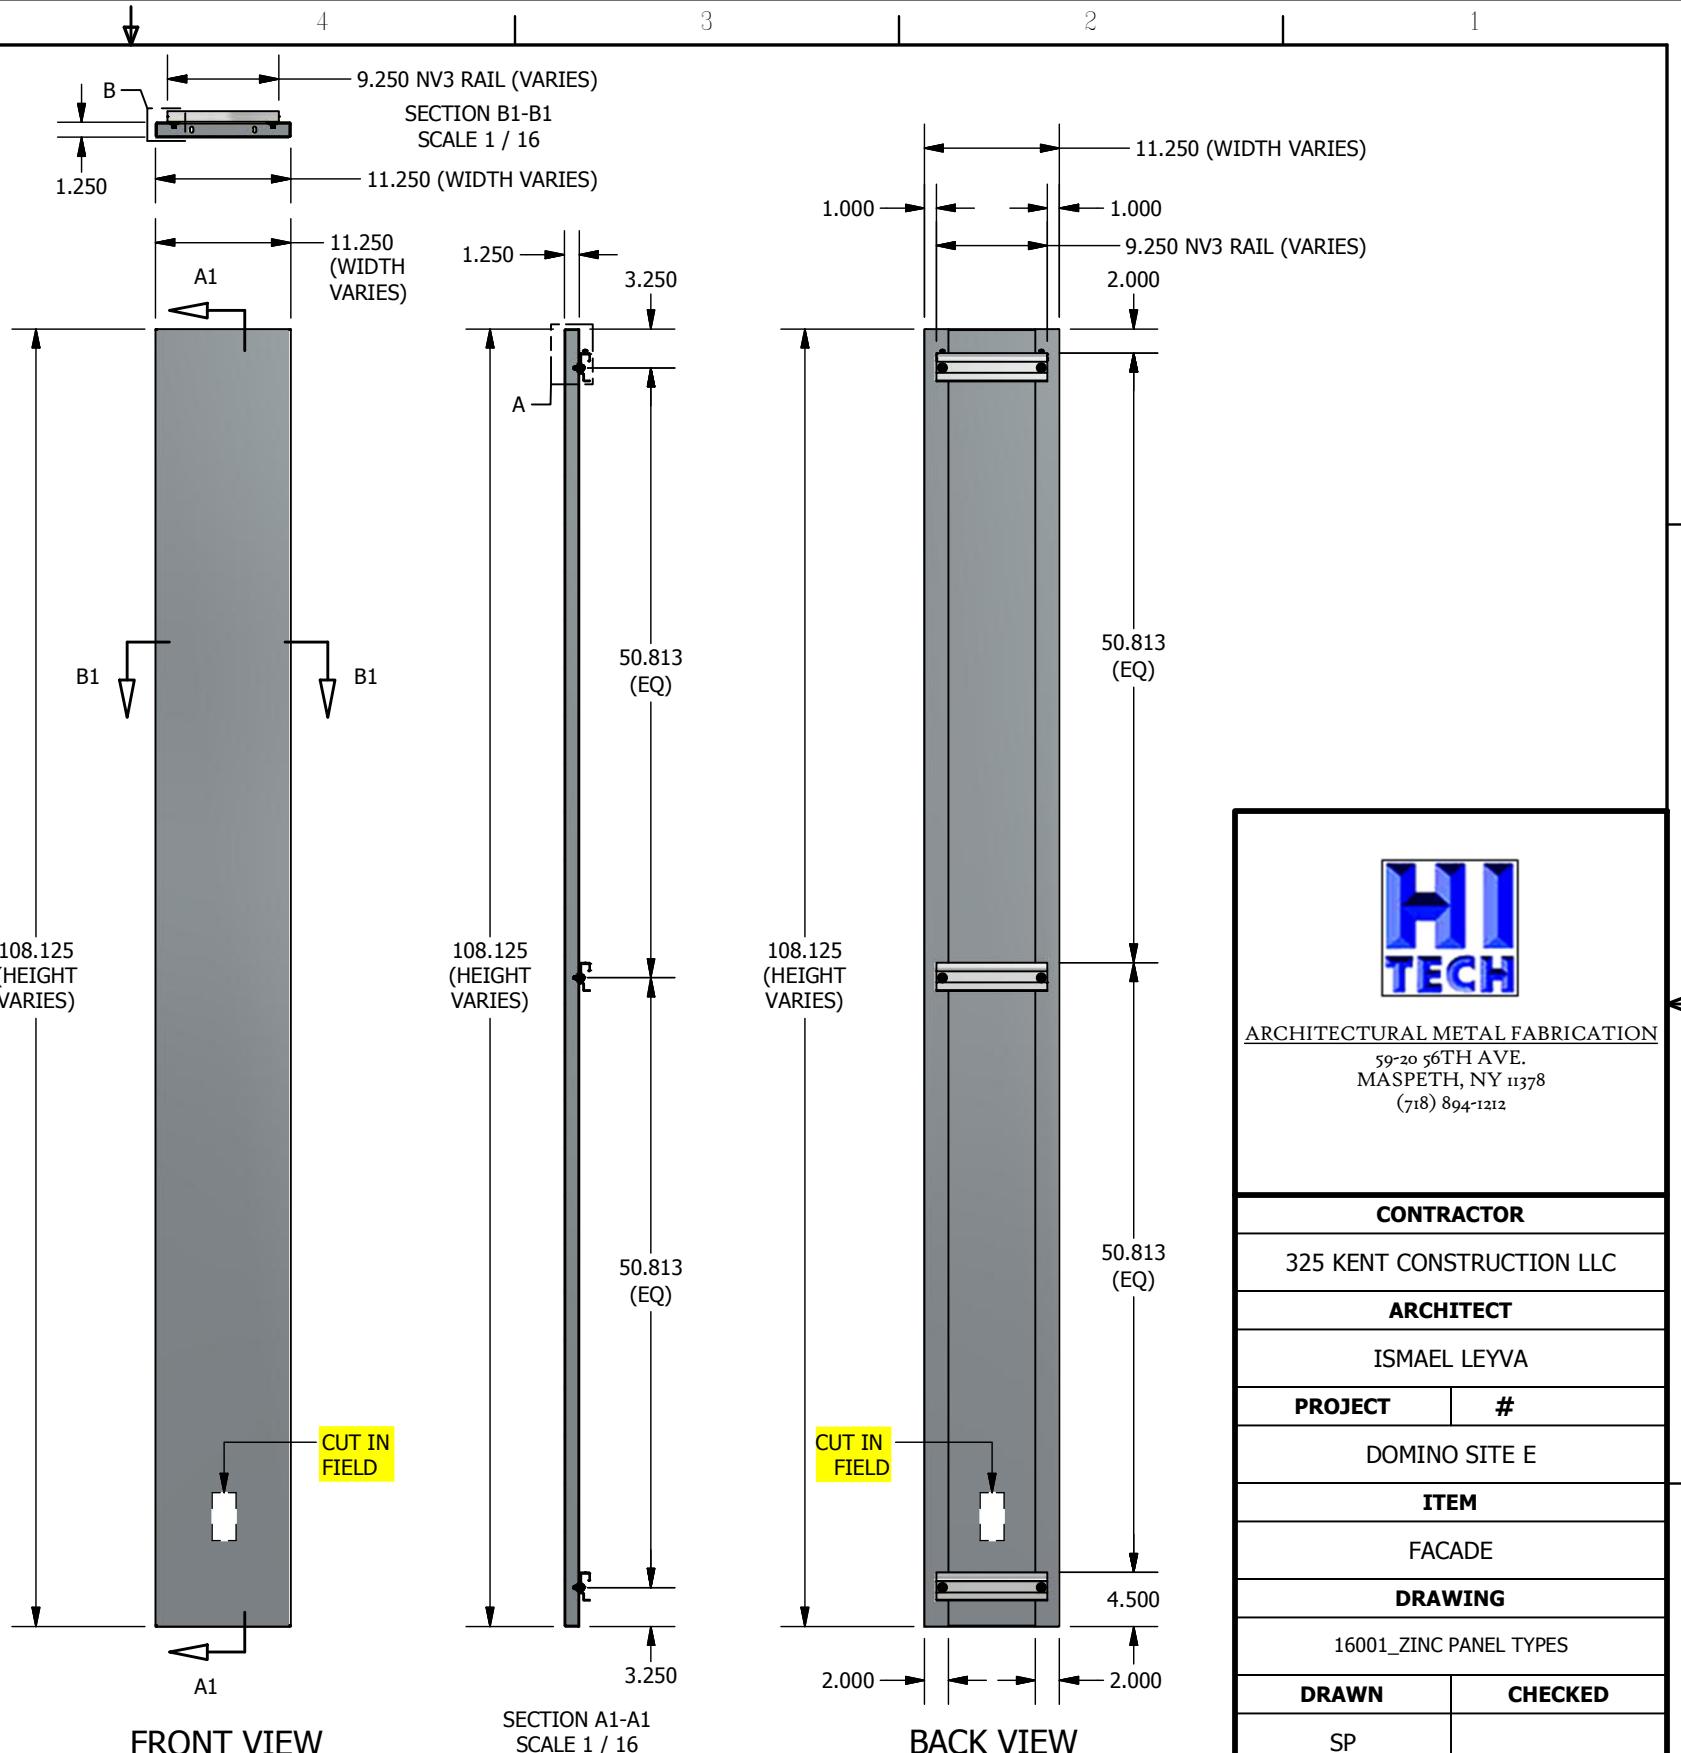


SECTION A1  
SCALE 1 / 1


PART TAG:	Z000 'VERTICAL' PANELS: PANEL ID PER TABLE	ISSUE DATE	REVISION
QT:	(QTY) PER TABLE (SHEET 1)	7/28/2016	A
MATERIAL:	2.00MM ZINC	SCALE	SHEET NUMBER
FINISH:	ZINC - NATURAL; ALUM. - BLACK ANOD.		
FLAT FILE:		(AS SHOWN)	2 / 37

PANEL ID	PANEL TYPE	BEND PROFILE	WIDTH (IN)	HEIGHT (IN)	PANEL TYPE (QTY)
Z000-1-029	VERTICAL	TYPE 1_CL	23.625	108.125	2
Z000-1-338	VERTICAL	TYPE 1_CL	21.625	108.125	1
Z000-1-504	VERTICAL	TYPE 1_CL	26.125	133.75	1
Z000-1-534	VERTICAL	TYPE 1_CL	21.875	34.5	1
Z000-1-539	VERTICAL	TYPE 1_CL	23.625	133.5	1
Z000-1-543	VERTICAL	TYPE 1_CL	35.125	34.5	1
PANEL TOTAL					7

**Z000-1-029 (SHOWN)**

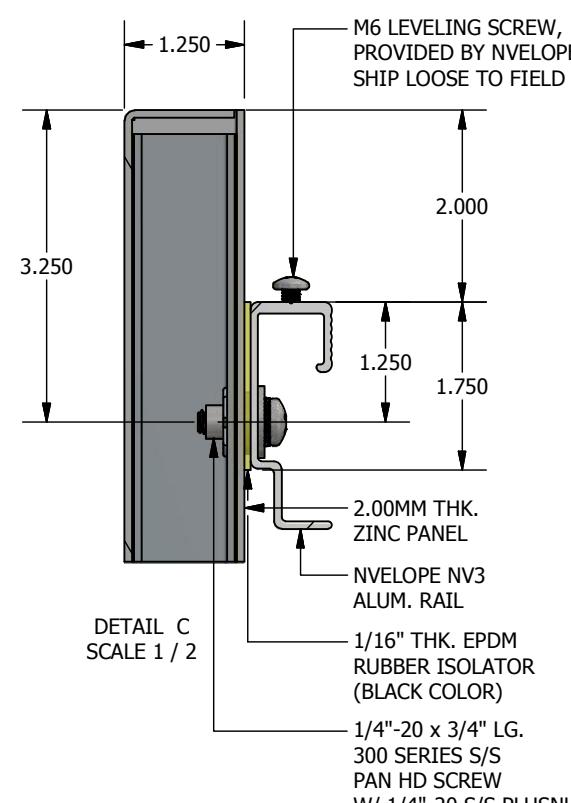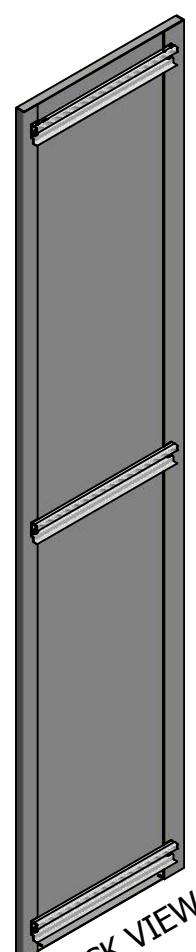

DETAIL C  
SCALE 1 / 2

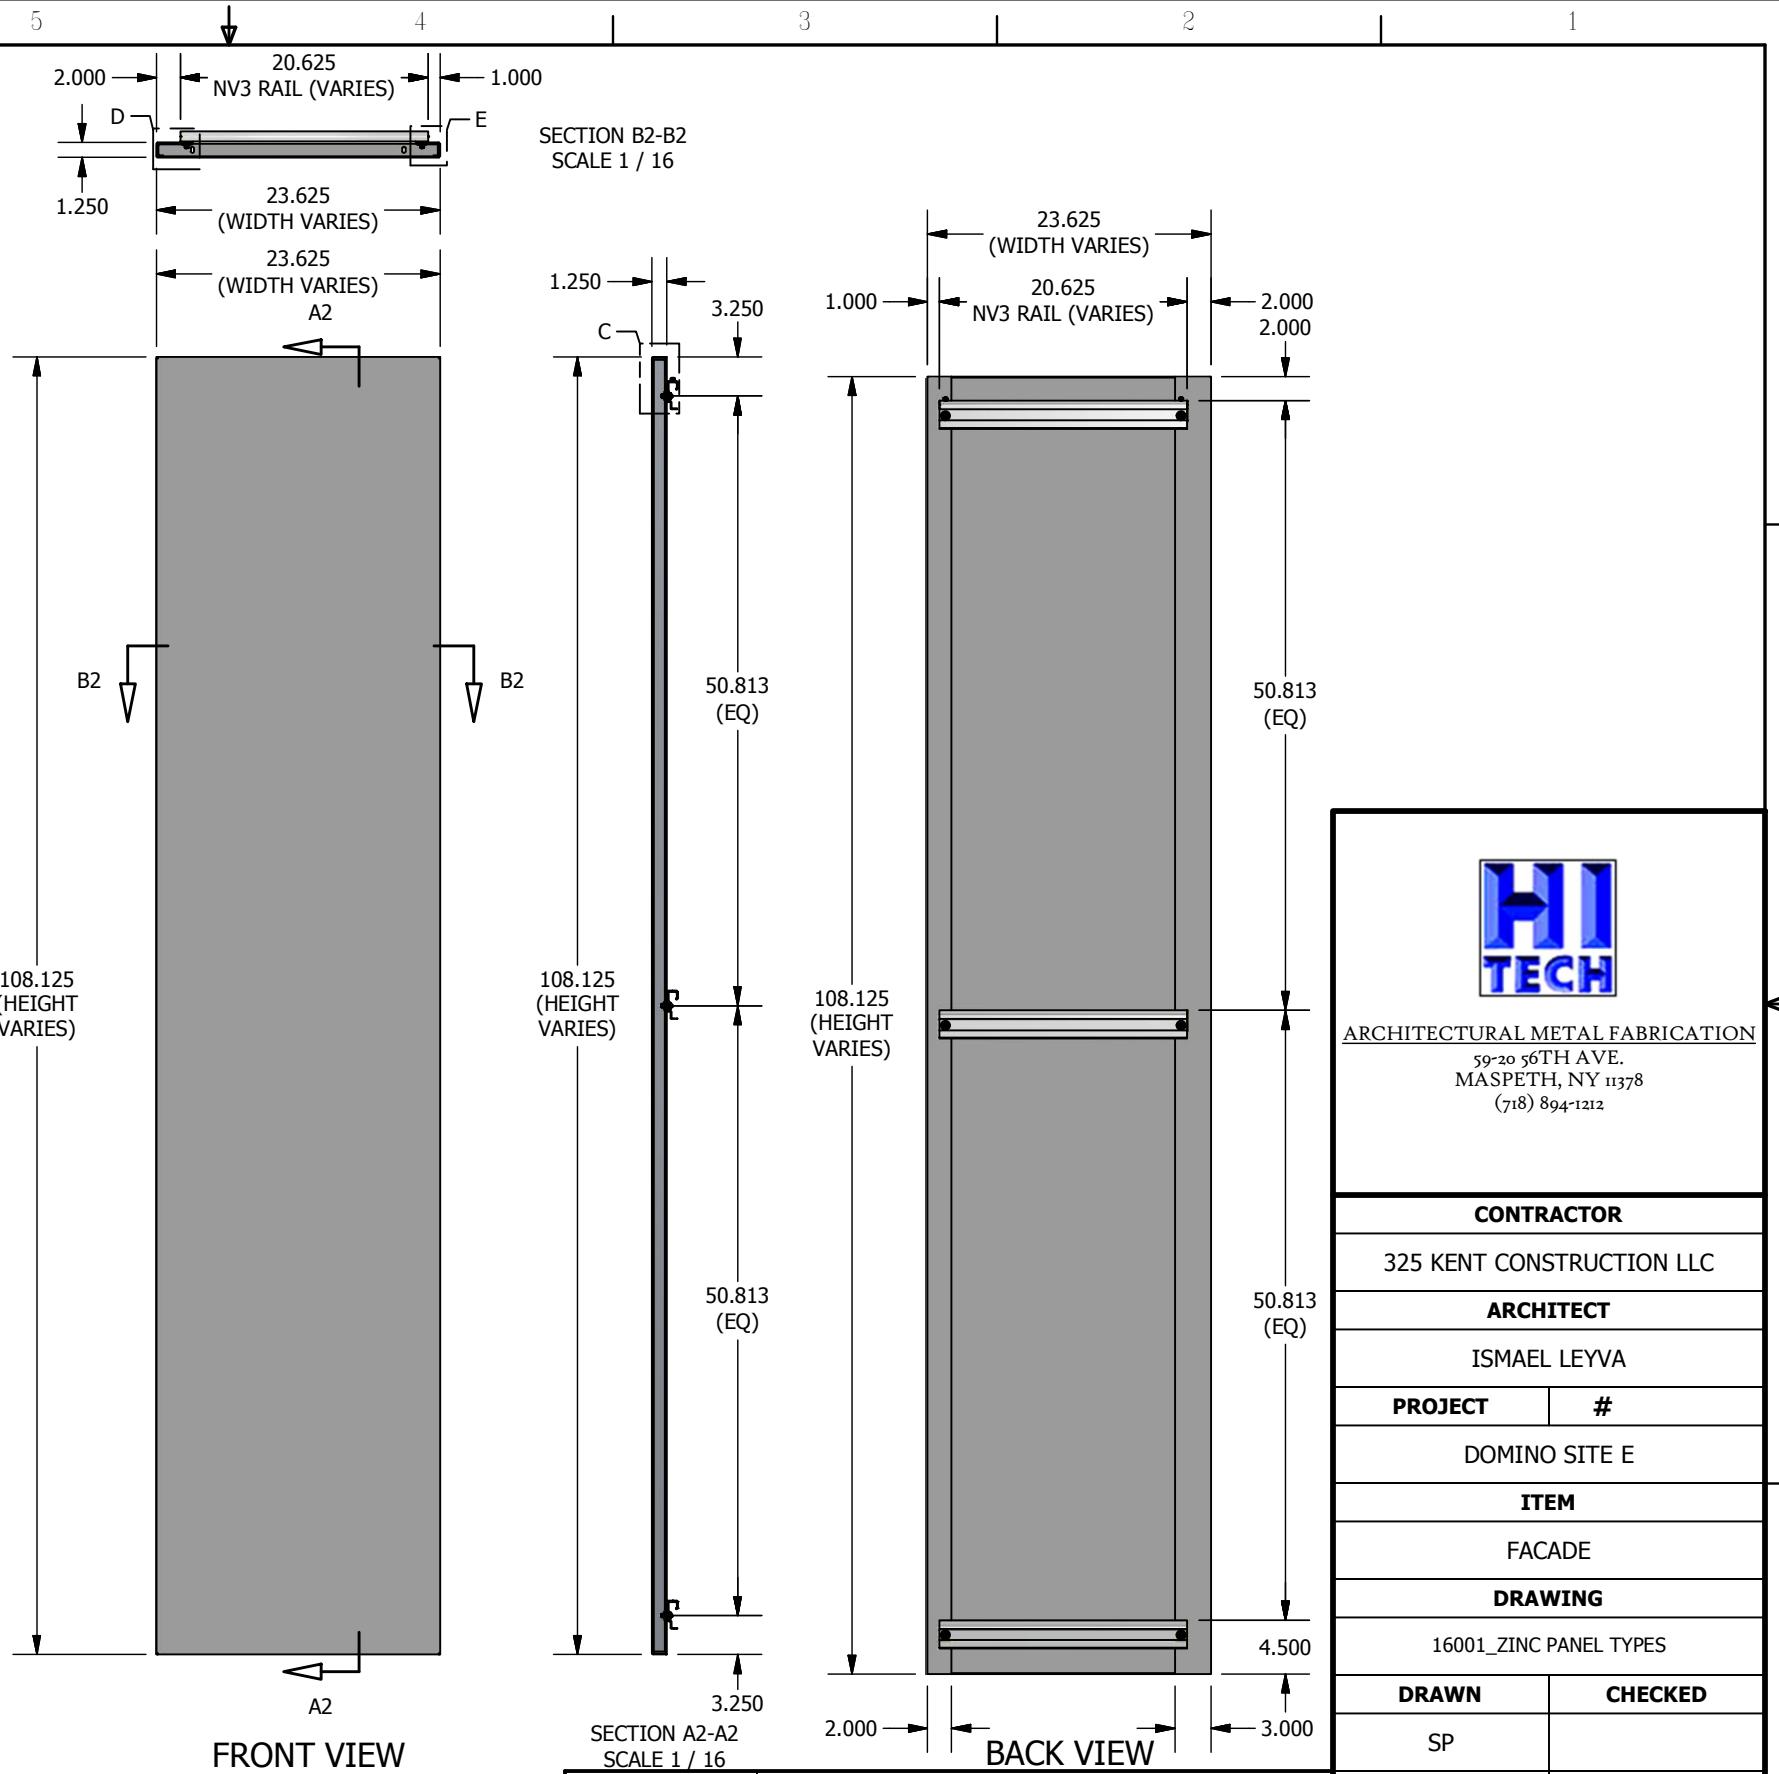

ARCHITECTURAL METAL FABRICATION  
59-20 56TH AVE.  
MASPETH, NY 11378  
(718) 804-1312

---

2025 KENT CONSTRUCTION LLC

ARCHITECT

**PROJECT** #

DOMINO SITE E

## FACADE

## DRAWING

---

<b>DRAWN</b>	<b>CHECKED</b>
--------------	----------------



卷之三

7/28/2016 | A

DOWN) 3

PANEL ID	PANEL TYPE	BEND PROFILE	WIDTH (IN)	HEIGHT (IN)	PANEL TYPE (QTY)
Z000-1-021	VERTICAL	TYPE 1_CR	11.625	100.25	1
Z000-1-027	VERTICAL	TYPE 1_CR	15.25	108.125	1
Z000-1-029	VERTICAL	TYPE 1_CR	23.625	108.125	6
Z000-1-032	VERTICAL	TYPE 1_CR	12.75	108.125	1
Z000-1-069	VERTICAL	TYPE 1_CR	25.625	108.125	1
Z000-1-335	VERTICAL	TYPE 1_CR	18.125	108.125	1
Z000-1-504	VERTICAL	TYPE 1_CR	26.125	133.75	1
Z000-1-529	VERTICAL	TYPE 1_CR	21.625	34.5	1
Z000-1-551	VERTICAL	TYPE 1_CR	23.375	34.5	1
PANEL TOTAL					14

**Z000-1-029 (SHOWN)**

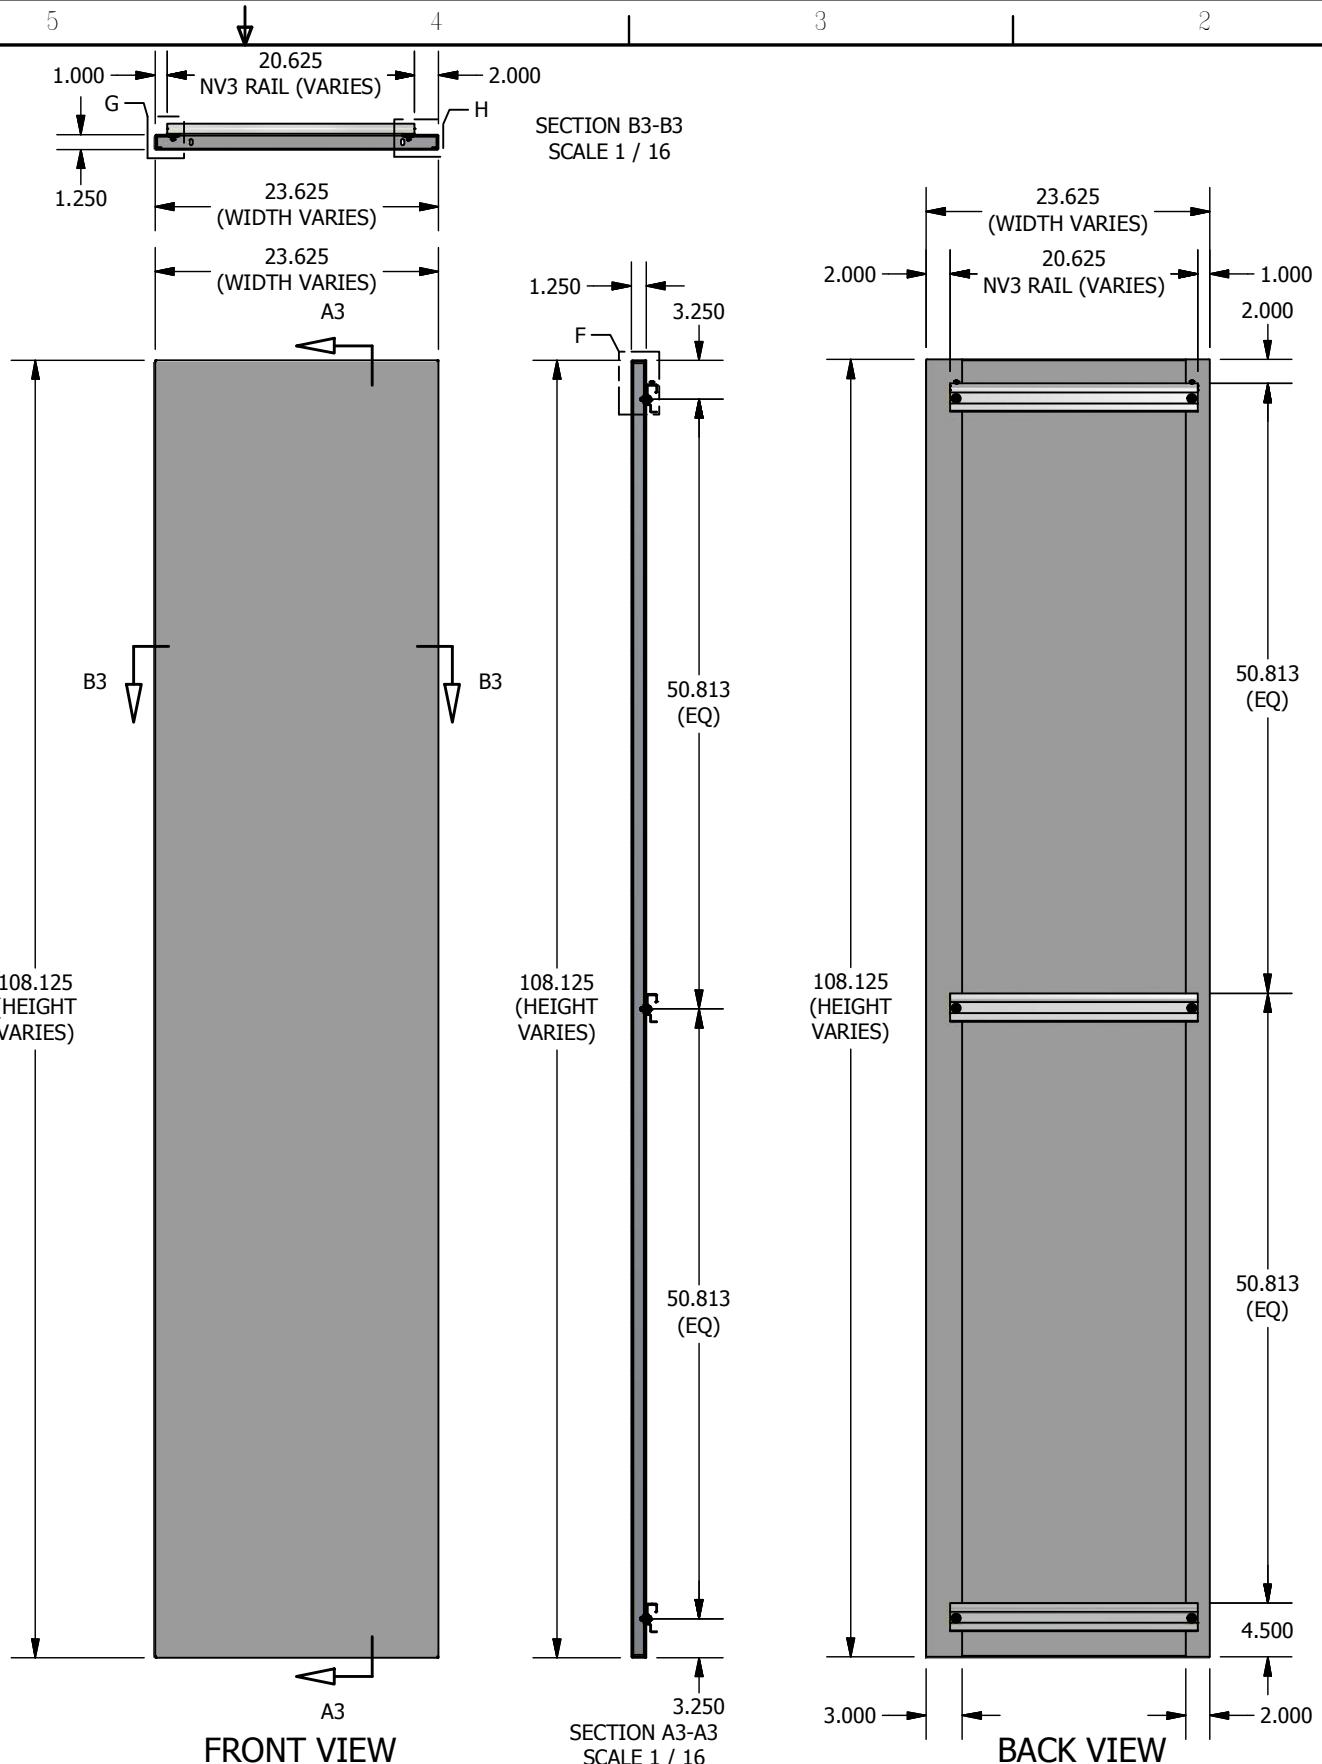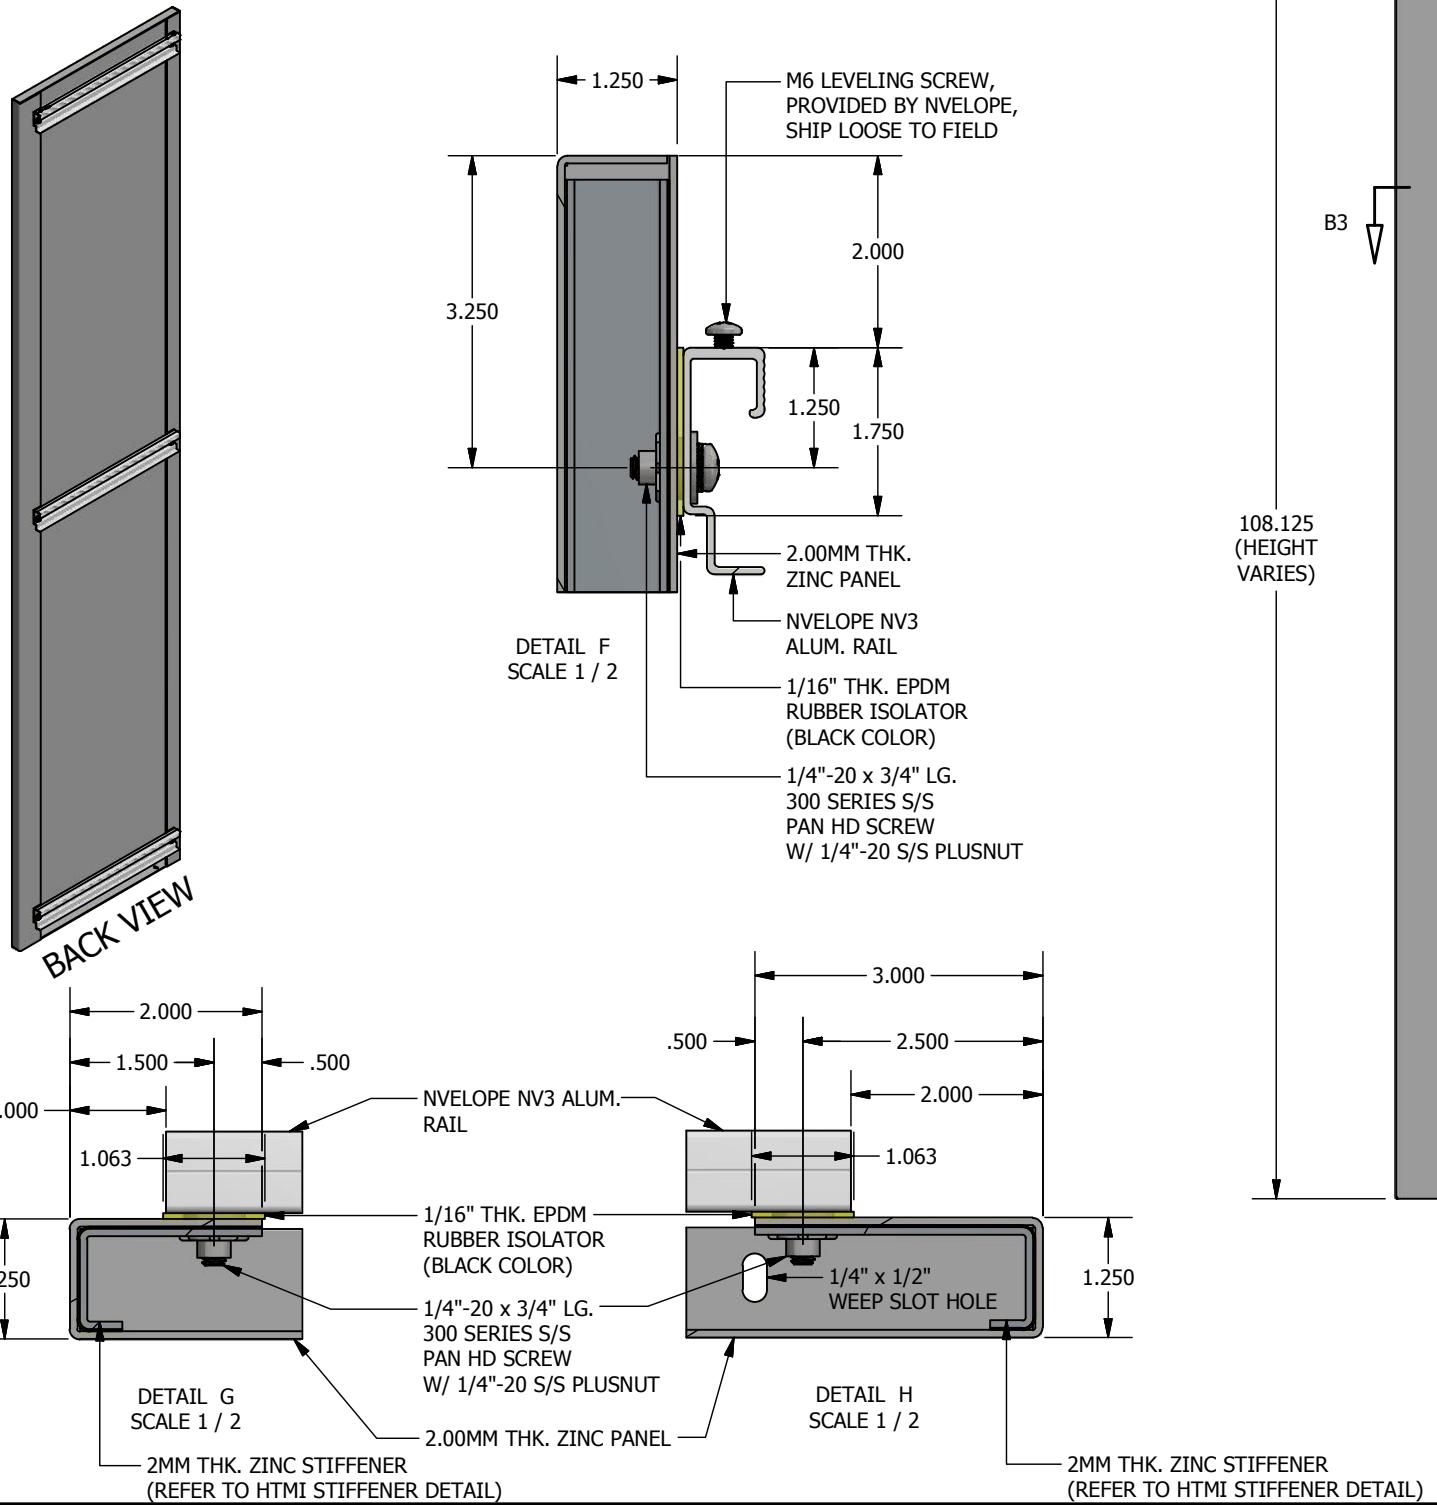

ARCHITECTURAL METAL FABRICATION  
59-20 56TH AVE.  
MASPETH, NY 11378  
(718) 842-1122

CONTINUATION

325 KENT CONSTRUCTION LLC

---

ARCHITECT

TSMAFI | FYVA

PROJECT	#
---------	---

#### **ITEM**

---

ACADE

#### **DRAWING**

## 16001 ZINC PANEL TYPES

**CHECK**

6P

**DATE** | **REVI**

/2016 | A

SALE SHEET M

SCALE 1 / 16		BACK VIEW	
PART TAG:	CORNER RIGHT Z000 'VERTICAL' PANELS: PANEL ID PER TABLE	ISSUE DATE	REVISION
QT:	(QTY) PER TABLE	7/28/2016	A
MATERIAL:	2.00MM ZINC	SCALE	SHEET NUMBER
FINISH:	ZINC - NATURAL; ALUM. - BLACK ANOD.	(AS SHOWN)	4 / 37
FLAT FILE:			

## '1-FT' VERTICAL PANEL TABLE

PANEL ID	PANEL TYPE	BEND PROFILE	WIDTH (IN)	HEIGHT (IN)	PANEL TYPE (QTY)
Z01A-1-000	VERTICAL	TYPE 1	11.25	96.75	25
Z01A-1-001	VERTICAL	TYPE 1	11.25	100.25	237
Z01A-1-002	VERTICAL	TYPE 1	11.25	108.125	1
Z01A-1-003	VERTICAL	TYPE 1	11.625	100.25	2
Z01A-1-004	VERTICAL	TYPE 1	11.25	112.25	21
Z01A-1-005	VERTICAL	TYPE 1	11.25	88.5625	6
Z01A-1-006	VERTICAL	TYPE 1	10.5625	108.125	1
Z01A-1-007	VERTICAL	TYPE 1	10.875	108.125	1
Z01A-1-008	VERTICAL	TYPE 1	11.25	131.25	12
Z01A-1-009	VERTICAL	TYPE 1	12.125	131.25	1
Z01A-1-010	VERTICAL	TYPE 1	11.25	133.5	1
Z01A-1-011	VERTICAL	TYPE 1	11.25	129.75	2
Z01B-1-000	VERTICAL	TYPE 1	11.25	96.75	4
Z01B-1-001	VERTICAL	TYPE 1	10.25	96.75	3
Z01B-1-002	VERTICAL	TYPE 1	11.25	100.25	139
Z01B-1-003	VERTICAL	TYPE 1	11.625	100.25	7
Z01B-1-004	VERTICAL	TYPE 1	11.625	108.125	1
Z01B-1-005	VERTICAL	TYPE 1	9.625	100.25	1
Z01B-1-006	VERTICAL	TYPE 1	11.25	112.25	10
Z01B-1-007	VERTICAL	TYPE 1	11.25	88.5625	5
Z01B-1-008	VERTICAL	TYPE 1	11.25	131.25	16
Z01B-1-010	VERTICAL	TYPE 1	14.25	133.75	1
Z01B-1-011	VERTICAL	TYPE 1	11.25	129.75	3
Z01B-3-000	VERTICAL	TYPE 1	11.25	96.75	4
Z01B-3-001	VERTICAL	TYPE 1	10.25	96.75	1
Z01B-3-002	VERTICAL	TYPE 1	11.25	100.25	66
Z01B-3-003	VERTICAL	TYPE 1	11.25	108.125	3
Z01B-3-004	VERTICAL	TYPE 1	11.25	88.5625	1
Z01B-3-005	VERTICAL	TYPE 1	11.625	112.25	1
Z01B-3-007	VERTICAL	TYPE 1	11.25	112.25	1

PANEL ID	PANEL TYPE	BEND PROFILE	WIDTH (IN)	HEIGHT (IN)	PANEL TYPE (QTY)
Z01B-3-008	VERTICAL	TYPE 1	11.625	100.25	1
Z01B-3-009	VERTICAL	TYPE 1	11.25	131.25	16
Z01B-3-010	VERTICAL	TYPE 1	12.75	131.25	1
Z01B-3-011	VERTICAL	TYPE 1	12.125	131.25	1
Z01B-3-013	VERTICAL	TYPE 1	11.25	133.75	2
Z01B-3-015	VERTICAL	TYPE 1	11.25	133.5	12
Z01B-3-017	VERTICAL	TYPE 1	18.25	133.5	1
Z01B-3-018	VERTICAL	TYPE 1	9.25	133.5	2
Z01B-3-019	VERTICAL	TYPE 1	14.6875	129.75	1
Z01B-3-020	VERTICAL	TYPE 1	11.25	129.75	1
Z01B-3-021	VERTICAL	TYPE 1	13.25	133.5	1
Z01C-1-000	VERTICAL	TYPE 1	11.25	96.75	23
Z01C-1-001	VERTICAL	TYPE 1	11.25	100.25	191
Z01C-1-002	VERTICAL	TYPE 1	11.625	100.25	2
Z01C-1-003	VERTICAL	TYPE 1	11.25	112.25	15
Z01C-1-004	VERTICAL	TYPE 1	11.25	88.5625	4
Z01C-1-005	VERTICAL	TYPE 1	11.625	112.25	1
Z01C-1-006	VERTICAL	TYPE 1	11.25	108.125	1
Z01C-1-007	VERTICAL	TYPE 1	11.625	101.125	1
Z01C-1-008	VERTICAL	TYPE 1	11.25	131.25	14
Z01C-1-009	VERTICAL	TYPE 1	11.25	129.75	2
Z01C-1-010	VERTICAL	TYPE 1	11.25	129.75	1
Z01C-3-000	VERTICAL	TYPE 1	11.25	100.25	4
Z01C-3-001	VERTICAL	TYPE 1	11.25	108.125	1
Z01C-3-002	VERTICAL	TYPE 1	11.625	100.25	1
Z01C-3-003	VERTICAL	TYPE 1	11.25	112.25	2
Z01C-3-004	VERTICAL	TYPE 1	11.25	131.25	4
Z01C-3-005	VERTICAL	TYPE 1	11.25	133.75	1
Z01C-3-006	VERTICAL	TYPE 1	11.25	133.5	5
Z01C-3-007	VERTICAL	TYPE 1	11.25	129.75	2
PANEL TOTAL					891

\*PANELS CONFLICT WITH TERRACE CONCRETE CURB, HOLD FOR FURTHER COORDINATION

## '1-FT' VERTICAL PANEL (WITH CUTOUT) TABLE

NOTE: CANNOT RELEASE DUE TO CUTOUTS

PANEL ID	PANEL TYPE	BEND PROFILE	WIDTH (IN)	HEIGHT (IN)	PANEL TYPE (QTY)
Z01B-1-000	VERTICAL	TYPE 1_CO	11.25	96.75	1
Z01B-3-000	VERTICAL	TYPE 1_CO	11.25	96.75	1
PANEL TOTAL					2

\*PANELS NEED NOTCHES (4TH FL, INNER SOUTH AND NORTH), HOLD FOR FURTHER COORDINATION



CONTRACTOR

325 KENT CONSTRUCTION LLC

ARCHITECT

ISMAEL LEYVA

PROJECT #

DOMINO SITE E

ITEM

FAÇADE

DRAWING

16001\_ZINC PANEL TYPES

DRAWN CHECKED

SP

ISSUE DATE REVISION

7/28/2016 A

SCALE SHEET NUMBER

(AS SHOWN) 5 / 37




PART TAG:	
QT:	
MATERIAL:	
FINISH:	
FLAT FILE:	

**'1-FT' VERTICAL PANEL**  
**Z01A-1-001 (SHOWN)**


D



BACK VIEW

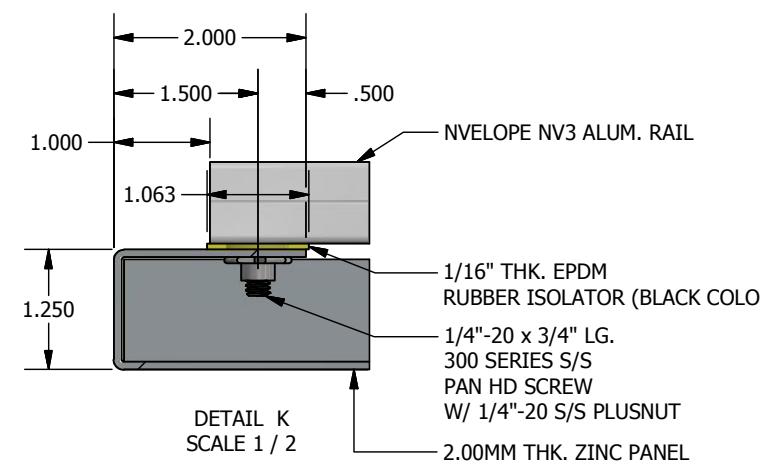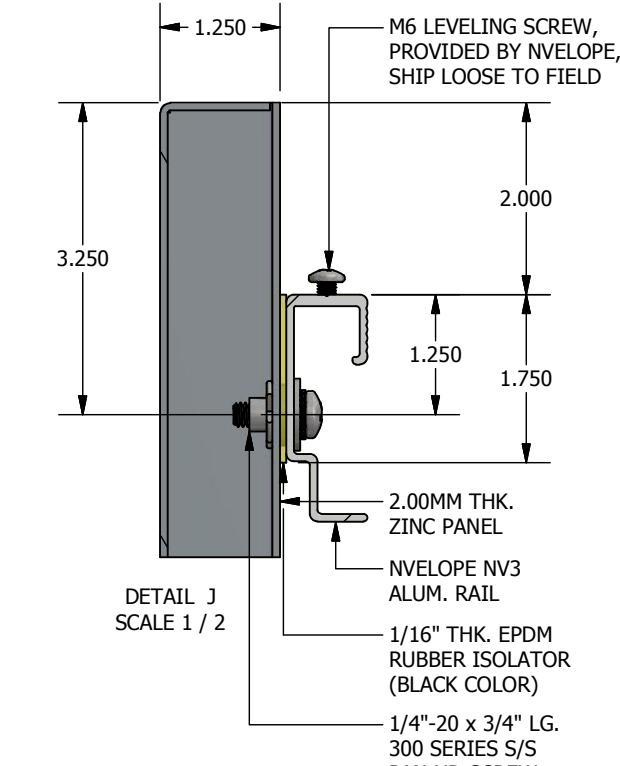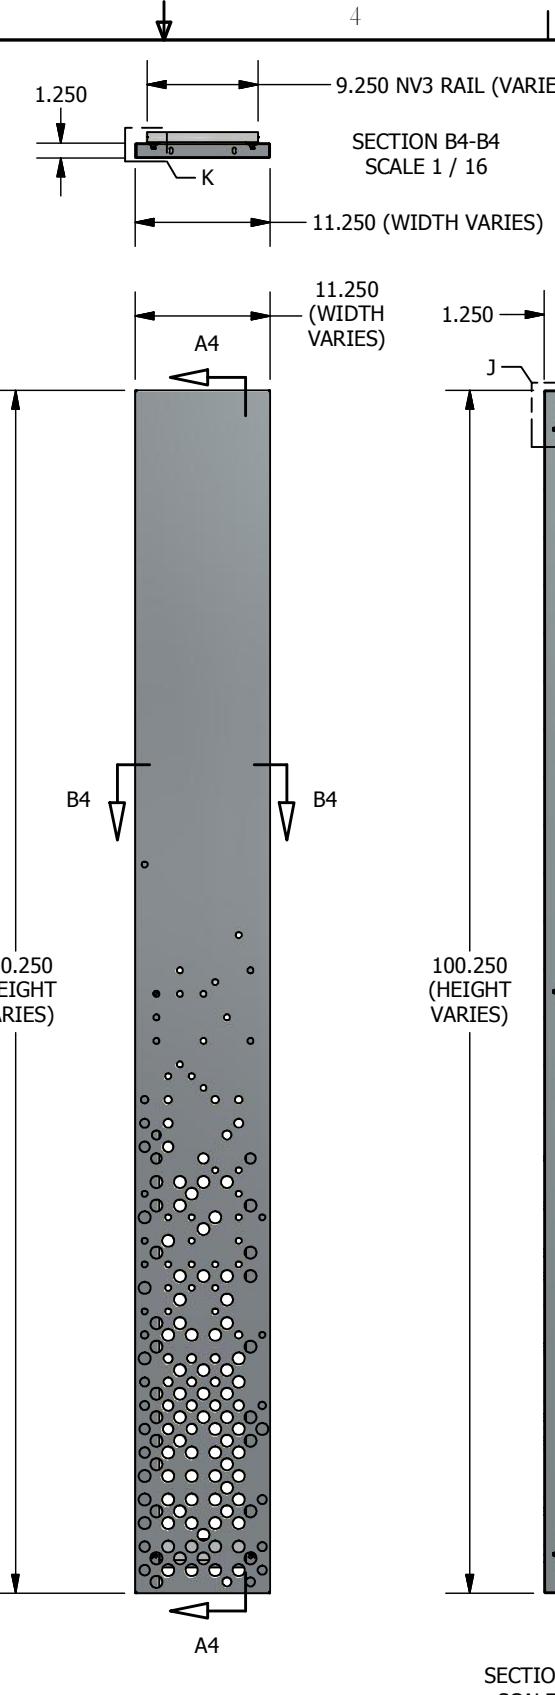
**STIFFENERS NOT SHOWN,  
REFER TO HTMI STIFFENER DETAIL**


FRONT VIEW

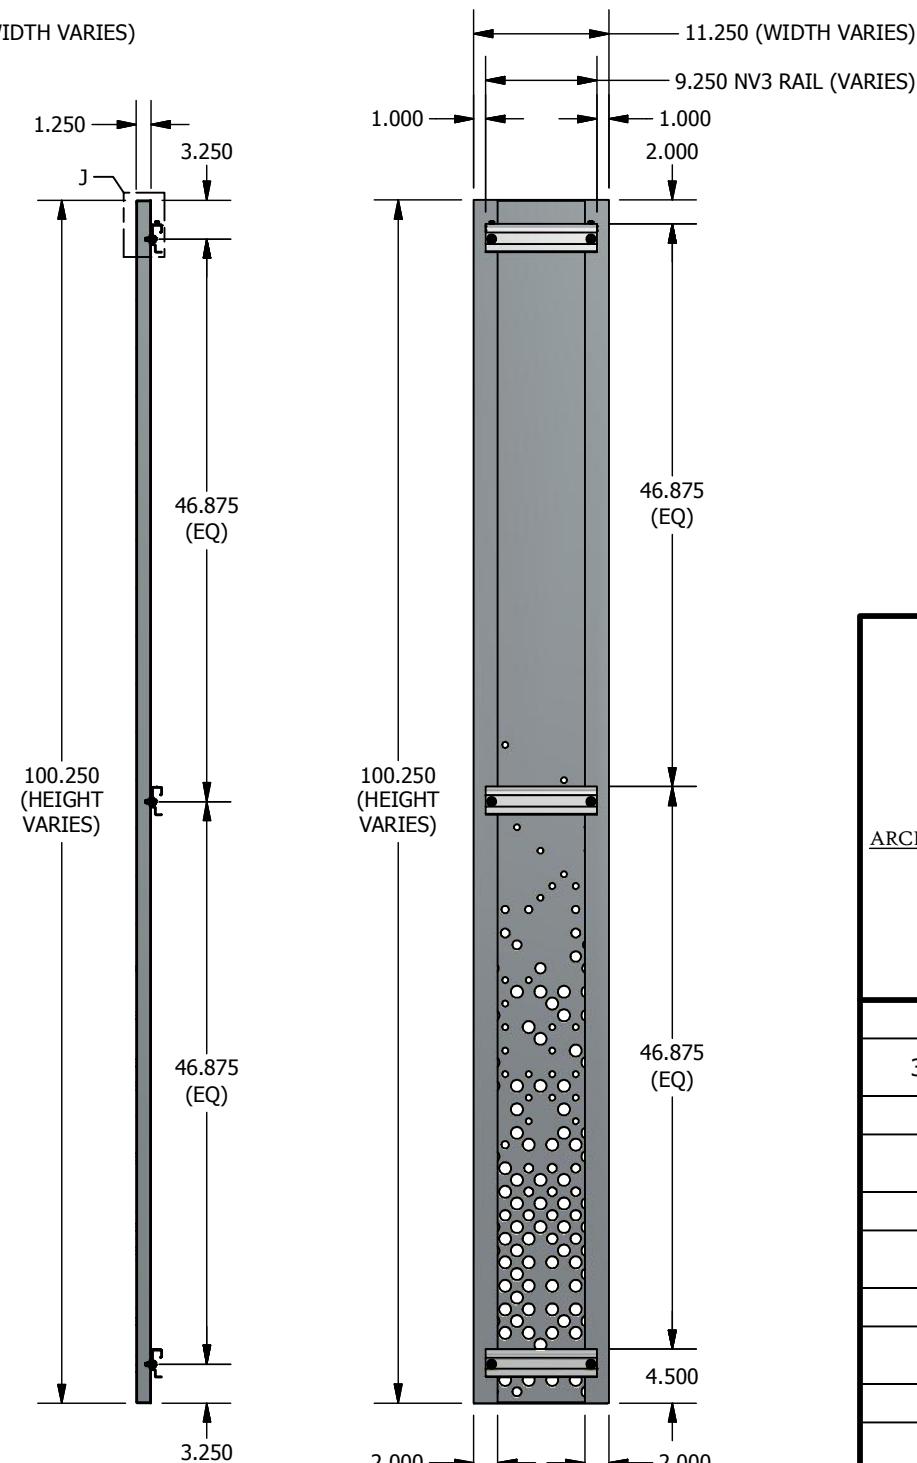


BACK VIEW


<b>HTM</b> TECH	
ARCHITECTURAL METAL FABRICATION 59-20 56TH AVE. MASPETH, NY 11378 (718) 894-1212	
<b>CONTRACTOR</b>	325 KENT CONSTRUCTION LLC
<b>ARCHITECT</b>	ISMAEL LEYVA
<b>PROJECT #</b>	DOMINO SITE E
<b>ITEM</b>	FAÇADE
<b>DRAWING</b>	16001_ZINC PANEL TYPES
<b>DRAWN</b>	<b>CHECKED</b>
SP	
<b>ISSUE DATE</b>	<b>REVISION</b>
7/28/2016	A
<b>SCALE</b>	<b>SHEET NUMBER</b>
(AS SHOWN)	6 / 37

8 7 6 5 4 3 2 1


PANEL ID	PANEL TYPE	BEND PROFILE	WIDTH (IN)	HEIGHT (IN)	PANEL TYPE (QTY)
Z01F-1-000	VERTICAL	TYPE 1	11.25	96.75	6
Z01F-1-001	VERTICAL	TYPE 1	11.25	100.25	7
Z01F-2-000	VERTICAL	TYPE 1	11.25	96.75	7
Z01F-2-001	VERTICAL	TYPE 1	13.75	108.125	1
Z01F-2-002	VERTICAL	TYPE 1	11.25	100.25	2
Z01F-2-003	VERTICAL	TYPE 1	17.625	120.125	1
Z01F-2-004	VERTICAL	TYPE 1	12.5	120.125	1
PANEL TOTAL					25

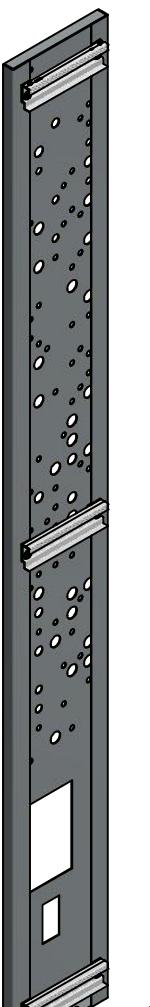**Z01F-1-001 (SHOWN)****\*HOLD FOR LIGHT FIXTURE APPROVED DRAWING**

BACK VIEW

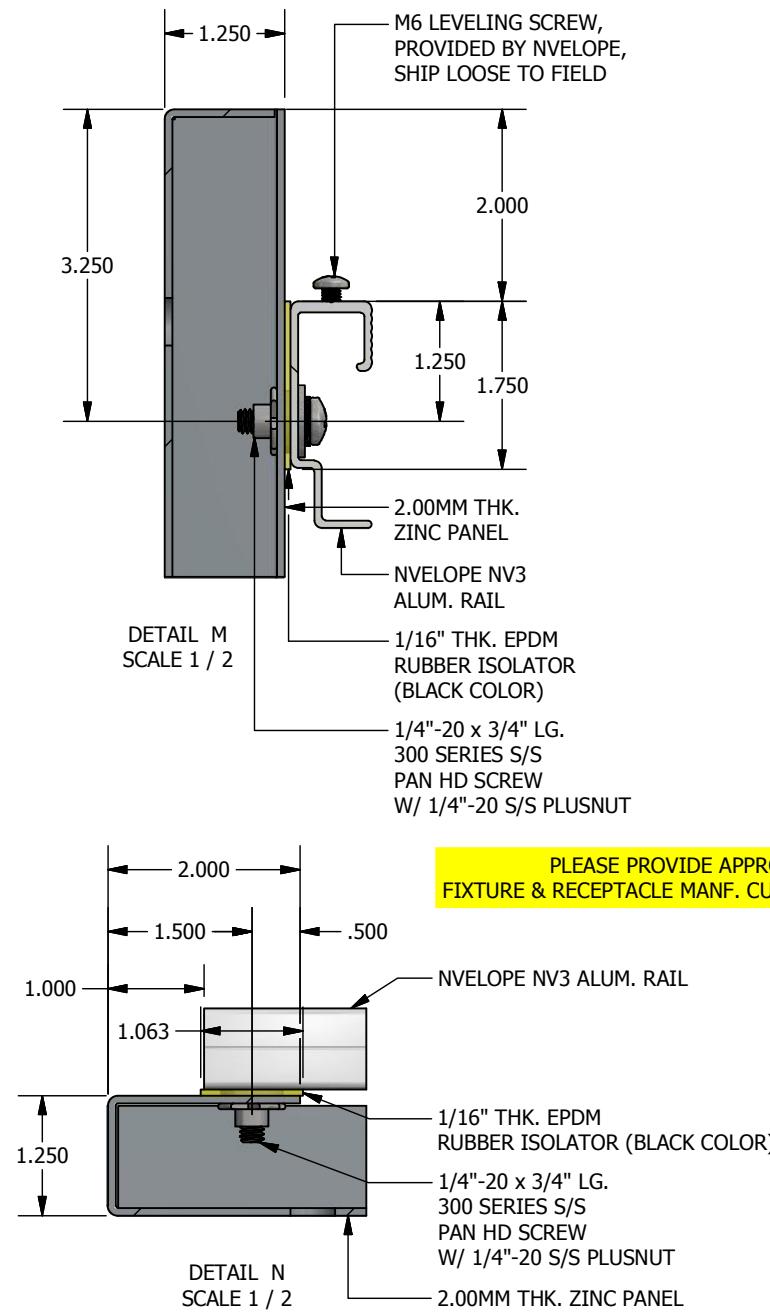

**STIFFENERS NOT SHOWN,  
REFER TO HTMI STIFFENER DETAIL**

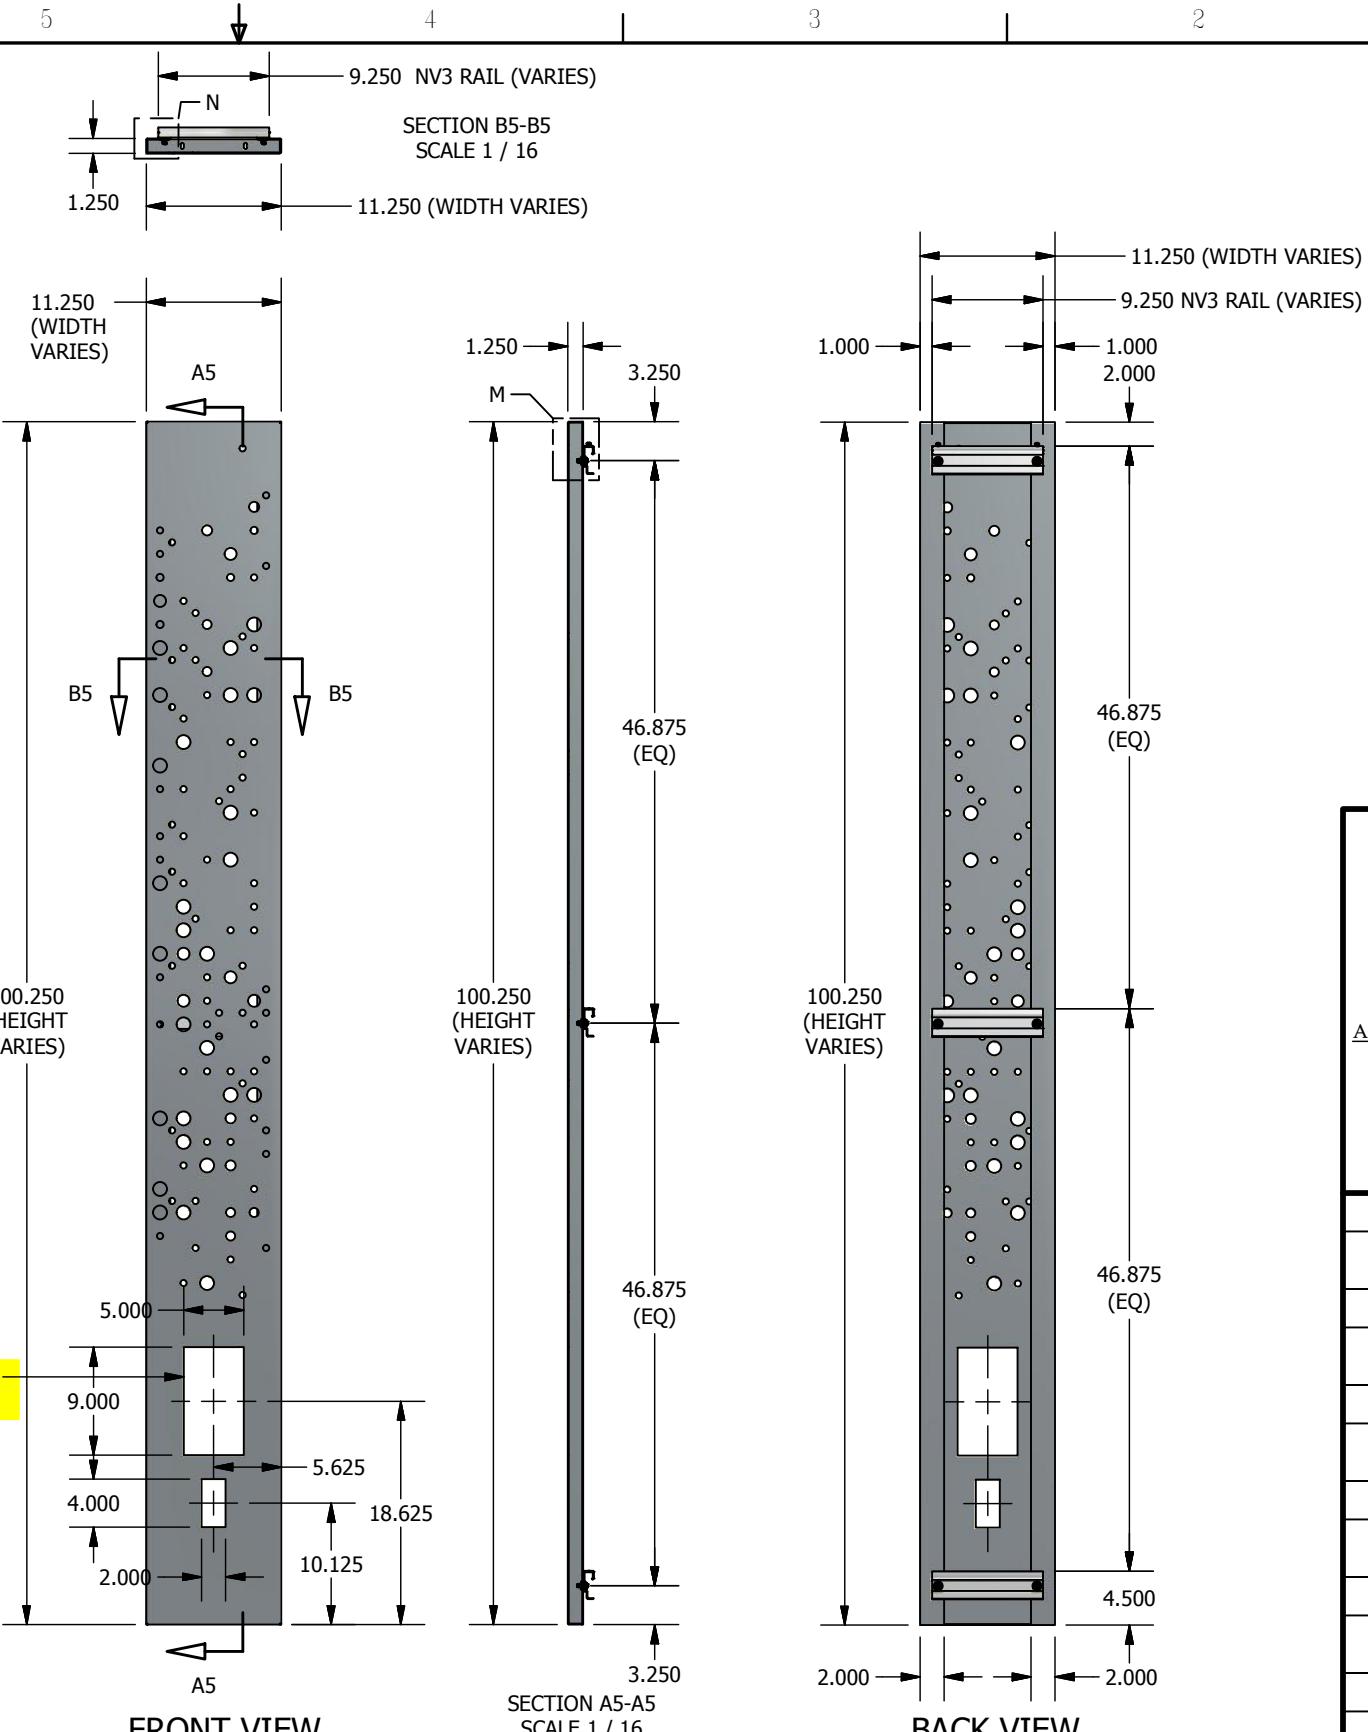

PART TAG:	Z01F '1-FT' PANELS: PANEL ID PER TABLE	ISSUE DATE	
QT:	(QTY) PER TABLE	REVISION	A
MATERIAL:	2.00MM ZINC	7/28/2016	
FINISH:	ZINC - NATURAL; ALUM. - BLACK ANOD.	SCALE	
FLAT FILE:	(AS SHOWN)	SHEET NUMBER	7 / 37



ARCHITECTURAL METAL FABRICATION  
59-20 56TH AVE.  
MASPETH, NY 11378  
(718) 894-1212

**CONTRACTOR**

325 KENT CONSTRUCTION LLC

**ARCHITECT**

ISMAEL LEYVA

**PROJECT #**

DOMINO SITE E

**ITEM**

FAÇADE

**DRAWING**

16001\_ZINC PANEL TYPES

**DRAWN**

SP


**CHECKED****ISSUE DATE**

A


**REVISION****SCALE****SHEET NUMBER****FLAT FILE:****(AS SHOWN)**

PANEL ID	PANEL TYPE	BEND PROFILE	WIDTH (IN)	HEIGHT (IN)	PANEL TYPE (QTY)
Z07A-1-000	VERTICAL	TYPE 1	17.25	100.25	7
Z07A-1-001	VERTICAL	TYPE 1	17.25	88.5625	1
Z07A-1-002	VERTICAL	TYPE 1	17.25	131.25	2
Z07A-2-000	VERTICAL	TYPE 1	17.25	100.25	1
Z07B-1-000	VERTICAL	TYPE 1	17.25	100.25	4
Z07B-1-001	VERTICAL	TYPE 1	17.25	88.5625	1
Z07B-2-000	VERTICAL	TYPE 1	17.25	100.25	2
Z07B-2-001	VERTICAL	TYPE 1	17.25	88.5625	1
PANEL TOTAL					19


Z07A-1-000 (SHOWN)

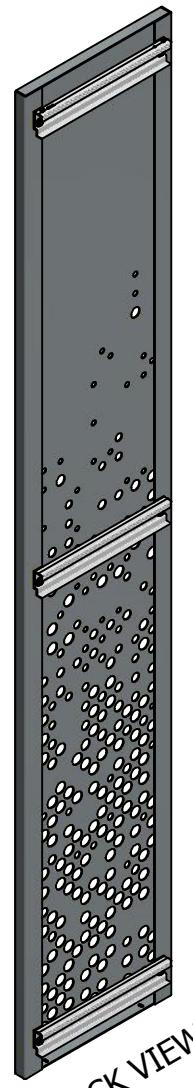


BACK VIEW

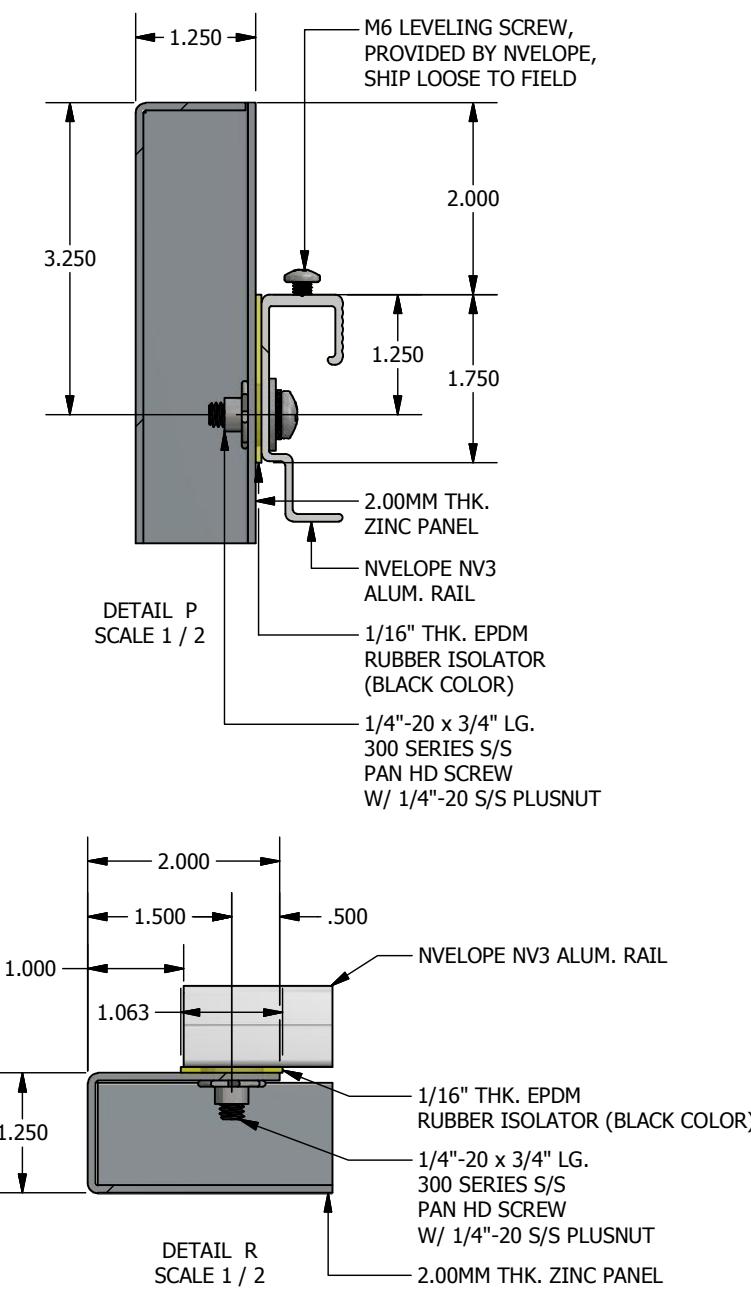

**STIFFENERS NOT SHOWN,  
REFER TO HTMI STIFFENER DETAIL**

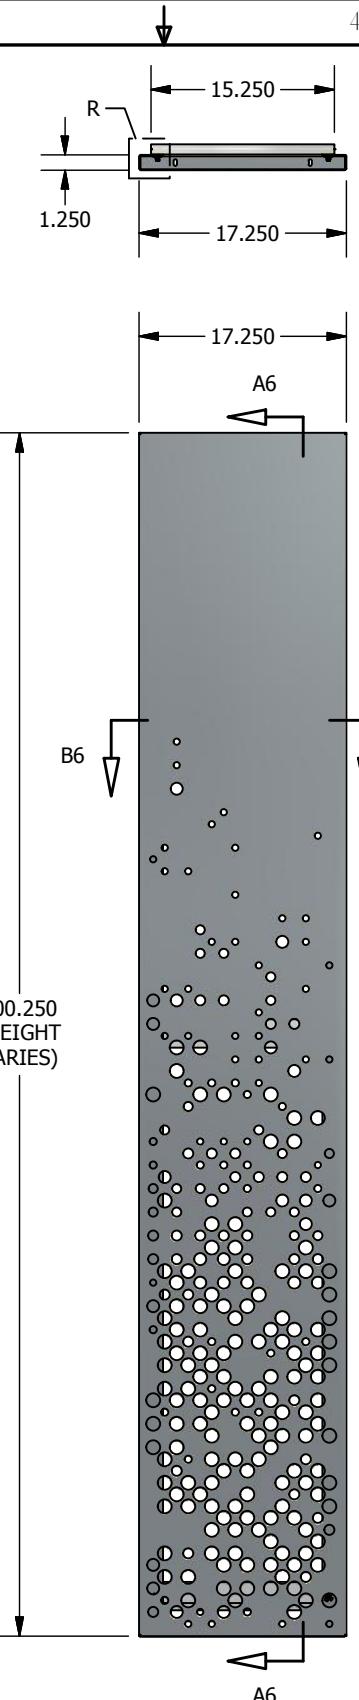

SECTION B6-B6  
SCALE 1 / 16

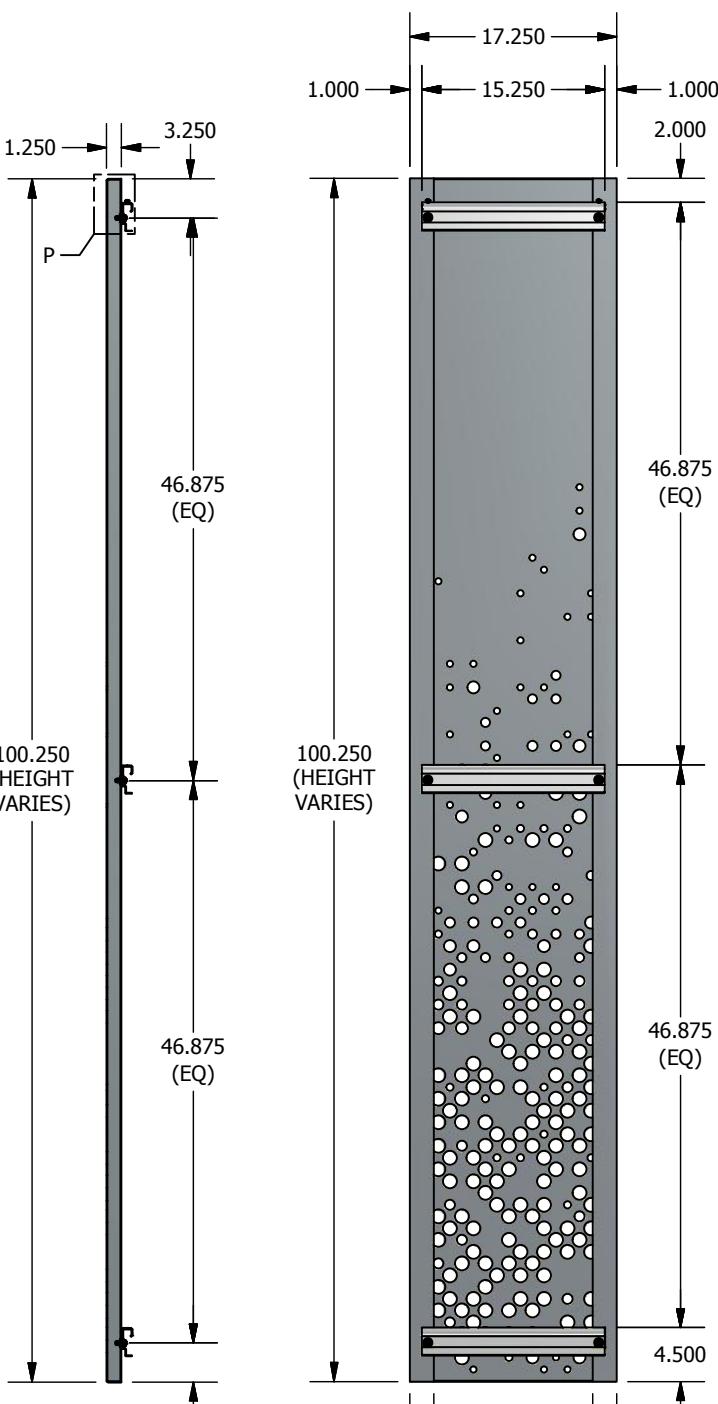

SECTION A6-A6  
SCALE 1 / 16




EXCERPT		ISSUE DATE	REVISION
PART TAG:	'1.5-FT' PANELS: PANEL ID PER TABLE	7/28/2016	A
QT:	(QTY) PER TABLE	SCALE	SHEET NUMBER
MATERIAL:	2.00MM ZINC		
FINISH:	ZINC - NATURAL; ALUM. - BLACK ANOD.	(AS SHOWN)	8 / 37
FLAT FILE:			

## '2-Ft' VERTICAL PANEL TABLE



PANEL ID	PANEL TYPE	BEND PROFILE	WIDTH (IN)	HEIGHT (IN)	PANEL TYPE (QTY)	PANEL ID	PANEL TYPE	BEND PROFILE	WIDTH (IN)	HEIGHT (IN)	PANEL TYPE (QTY)	PANEL ID	PANEL TYPE	BEND PROFILE	WIDTH (IN)	HEIGHT (IN)	PANEL TYPE (QTY)
Z02A-1-000	VERTICAL	TYPE 1	23.25	96.75	7	Z02A-3-011	VERTICAL	TYPE 1	23.25	133.5	8	Z02B-3-000	VERTICAL	TYPE 1	23.25	100.25	1
Z02A-1-001	VERTICAL	TYPE 1	23.25	100.25	85	Z02A-3-013	VERTICAL	TYPE 1	23	133.5	1	Z02B-3-001	VERTICAL	TYPE 1	23.25	108.125	2
Z02A-1-002	VERTICAL	TYPE 1	20.0625	100.25	1	Z02A-3-014	VERTICAL	TYPE 1	15.25	133.5	1	Z02B-3-002	VERTICAL	TYPE 1	19.375	100.25	1
Z02A-1-003	VERTICAL	TYPE 1	25.25	100.25	1	Z02A-3-015	VERTICAL	TYPE 1	24.25	133.5	1	Z02B-3-003	VERTICAL	TYPE 1	23.25	133.75	1
Z02A-1-005	VERTICAL	TYPE 1	24.25	108.125	1	Z02A-3-017	VERTICAL	TYPE 1	23.25	129.75	1	Z02B-3-004	VERTICAL	TYPE 1	23.25	133.5	5
Z02A-1-006	VERTICAL	TYPE 1	23.25	108.125	2	Z02A-3-018	VERTICAL	TYPE 1	39.25	133.5	2	Z02B-3-005	VERTICAL	TYPE 1	23.25	129.75	1
Z02A-1-008	VERTICAL	TYPE 1	21.625	100.25	2	Z02A-3-019	VERTICAL	TYPE 1	21.75	133.5	2	Z02B-3-006	VERTICAL	TYPE 1	25.25	129.75	1
Z02A-1-009	VERTICAL	TYPE 1	21.125	100.25	1	Z02A-4-000	VERTICAL	TYPE 1	23.25	100.25	6	Z02B-4-000	VERTICAL	TYPE 1	23.25	100.25	4
Z02A-1-011	VERTICAL	TYPE 1	16.5625	108.125	1	Z02A-4-001	VERTICAL	TYPE 1	18.25	108.125	1	Z02B-4-002	VERTICAL	TYPE 1	23.25	108.125	1
Z02A-1-012	VERTICAL	TYPE 1	17.25	108.125	2	Z02A-4-002	VERTICAL	TYPE 1	20.375	108.125	1	Z02B-4-003	VERTICAL	TYPE 1	23.875	131.25	1
Z02A-1-015	VERTICAL	TYPE 1	9.625	100.25	1	Z02A-4-003	VERTICAL	TYPE 1	23.25	108.125	1	Z02B-4-004	VERTICAL	TYPE 1	23.25	133.75	2
Z02A-1-016	VERTICAL	TYPE 1	23.25	112.25	6	Z02A-4-004	VERTICAL	TYPE 1	21.125	112.25	1	Z02B-4-005	VERTICAL	TYPE 1	23.25	129.75	1
Z02A-1-017	VERTICAL	TYPE 1	23.625	112.25	1	Z02A-4-005	VERTICAL	TYPE 1	23.25	112.25	1	Z02C-1-000	VERTICAL	TYPE 1	23.25	96.75	2
Z02A-1-018	VERTICAL	TYPE 1	23	108.125	1	Z02A-4-006	VERTICAL	TYPE 1	19.25	133.75	1	Z02C-1-001	VERTICAL	TYPE 1	23.25	100.25	90
Z02A-1-020	VERTICAL	TYPE 1	17.25	100.25	1	Z02A-4-009	VERTICAL	TYPE 1	21.25	133.5	1	Z02C-1-002	VERTICAL	TYPE 1	24.625	100.25	1
Z02A-1-021	VERTICAL	TYPE 1	11.75	100.25	1	Z02A-4-010	VERTICAL	TYPE 1	23.25	133.5	4	Z02C-1-003	VERTICAL	TYPE 1	23.625	100.25	1
Z02A-1-022	VERTICAL	TYPE 1	23.875	131.25	1	Z02A-4-011	VERTICAL	TYPE 1	16.25	133.5	1	Z02C-1-005	VERTICAL	TYPE 1	23.25	88.5625	1
Z02A-1-023	VERTICAL	TYPE 1	23.25	131.25	3	Z02A-4-012	VERTICAL	TYPE 1	23.25	129.75	1	Z02C-1-006	VERTICAL	TYPE 1	23.25	112.25	8
Z02A-1-024	VERTICAL	TYPE 1	20.75	131.25	1	Z02A-4-013	VERTICAL	TYPE 1	23.25	129.75	1	Z02C-1-007	VERTICAL	TYPE 1	23.25	120.125	1
Z02A-1-026	VERTICAL	TYPE 1	23.25	133.75	1	Z02B-1-000	VERTICAL	TYPE 1	23.25	96.75	4	Z02C-1-009	VERTICAL	TYPE 1	22	131.25	1
Z02A-1-027	VERTICAL	TYPE 1	17.5	133.75	1	Z02B-1-001	VERTICAL	TYPE 1	23.75	96.75	1	Z02C-1-010	VERTICAL	TYPE 1	23.25	131.25	3
Z02A-1-029	VERTICAL	TYPE 1	21.5	133.5	1	Z02B-1-002	VERTICAL	TYPE 1	23.25	100.25	194	Z02C-1-011	VERTICAL	TYPE 1	16.25	129.75	1
Z02A-1-030	VERTICAL	TYPE 1	16.25	129.75	1	Z02B-1-003	VERTICAL	TYPE 1	19.25	100.25	1	Z02C-1-012	VERTICAL	TYPE 1	26.25	129.75	1
Z02A-1-031	VERTICAL	TYPE 1	23.25	129.75	4	Z02B-1-004	VERTICAL	TYPE 1	17.25	100.25	2	Z02C-1-013	VERTICAL	TYPE 1	17.75	129.75	1
Z02A-1-032	VERTICAL	TYPE 1	15.875	129.75	1	Z02B-1-005	VERTICAL	TYPE 1	26.25	108.125	1	Z02C-2-000	VERTICAL	TYPE 1	23.25	96.75	5
Z02A-1-034	VERTICAL	TYPE 1	19	129.75	1	Z02B-1-006	VERTICAL	TYPE 1	18	100.25	1	Z02C-2-001	VERTICAL	TYPE 1	23.25	100.25	97
Z02A-1-035	VERTICAL	TYPE 1	21.75	133.5	2	Z02B-1-007	VERTICAL	TYPE 1	14	108.125	1	Z02C-2-002	VERTICAL	TYPE 1	23.625	100.25	3
Z02A-2-000	VERTICAL	TYPE 1	23.25	96.75	7	Z02B-1-008	VERTICAL	TYPE 1	23.25	88.5625	5	Z02C-2-003	VERTICAL	TYPE 1	35.25	100.25	1
Z02A-2-001	VERTICAL	TYPE 1	23.25	100.25	91	Z02B-1-009	VERTICAL	TYPE 1	23.25	112.25	6	Z02C-2-004	VERTICAL	TYPE 1	23.25	108.125	2
Z02A-2-002	VERTICAL	TYPE 1	15.25	100.25	1	Z02B-1-010	VERTICAL	TYPE 1	23.625	112.25	1	Z02C-2-006	VERTICAL	TYPE 1	23.4375	100.25	1
Z02A-2-003	VERTICAL	TYPE 1	24.1875	100.25	1	Z02B-1-012	VERTICAL	TYPE 1	23.25	108.125	2	Z02C-2-007	VERTICAL	TYPE 1	23.25	112.25	5
Z02A-2-004	VERTICAL	TYPE 1	21.625	100.25	2	Z02B-1-013	VERTICAL	TYPE 1	23.625	100.25	1	Z02C-2-008	VERTICAL	TYPE 1	20.75	108.125	1
Z02A-2-006	VERTICAL	TYPE 1	16.75	108.125	1	Z02B-1-014	VERTICAL	TYPE 1	23.25	131.25	3	Z02C-2-009	VERTICAL	TYPE 1	23.25	131.25	3
Z02A-2-008	VERTICAL	TYPE 1	20.875	108.125	1	Z02B-1-015	VERTICAL	TYPE 1	23.25	129.75	1	Z02C-2-010	VERTICAL	TYPE 1	20.8125	129.75	1
Z02A-2-010	VERTICAL	TYPE 1	21.125	100.25	1	Z02B-1-017	VERTICAL	TYPE 1	18.0625	129.75	1	Z02C-2-011	VERTICAL	TYPE 1	21.75	129.75	1
Z02A-2-011	VERTICAL	TYPE 1	13	108.125	1	Z02B-2-000	VERTICAL	TYPE 1	23.25	96.75	13	Z02C-3-000	VERTICAL	TYPE 1	23.25	100.25	6
Z02A-2-012	VERTICAL	TYPE 1	23.25	108.125	4	Z02B-2-001	VERTICAL	TYPE 1	23.25	100.25	200	Z02C-3-002	VERTICAL	TYPE 1	23.25	133.75	1
Z02A-2-013	VERTICAL	TYPE 1	13.75	108.125	1	Z02B-2-003	VERTICAL	TYPE 1	14	108.125	1	Z02C-3-003	VERTICAL	TYPE 1	22	131.25	1
Z02A-2-014	VERTICAL	TYPE 1	23.25	112.25	5	Z02B-2-004	VERTICAL	TYPE 1	26.25	108.125	1	Z02C-3-004	VERTICAL	TYPE 1	14.25	133.5	1
Z02A-2-015	VERTICAL	TYPE 1	21.125	112.25	1	Z02B-2-006	VERTICAL	TYPE 1	23.25	112.25	12	Z02C-3-005	VERTICAL	TYPE 1	27	133.5	1
Z02A-2-016	VERTICAL	TYPE 1	17.25	100.25	2	Z02B-2											

8 7 6 5 4 3 2 1




**'2-FT' VERTICAL PANEL**  
**Z02A-1-001 (SHOWN)**

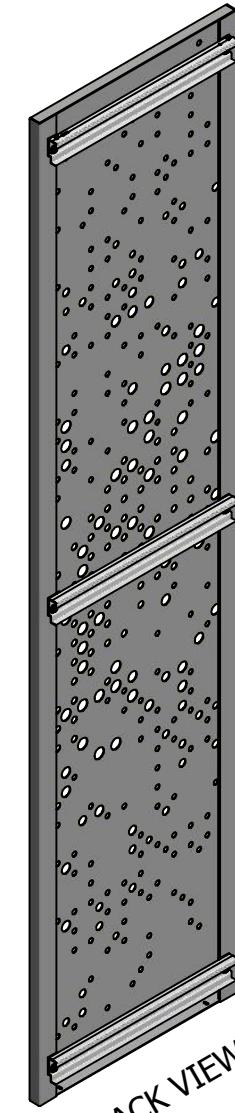

BACK VIEW

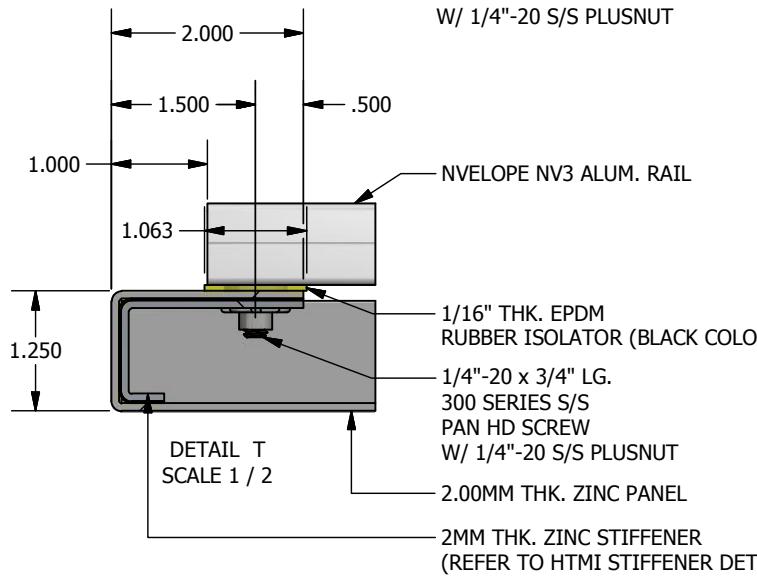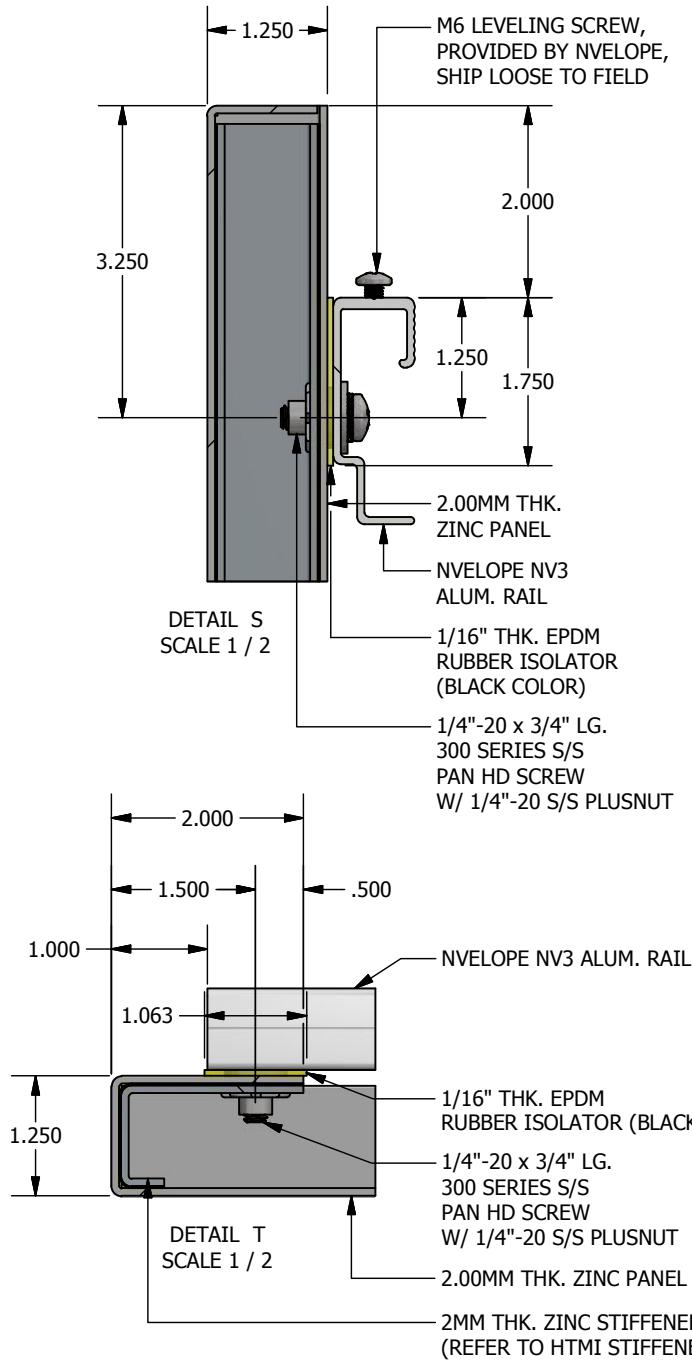

FRONT VIEW

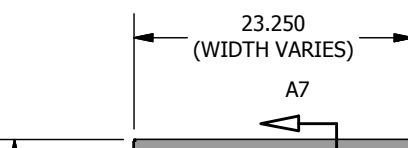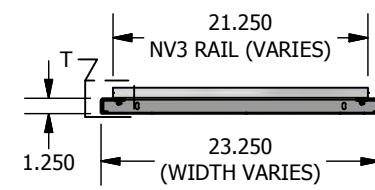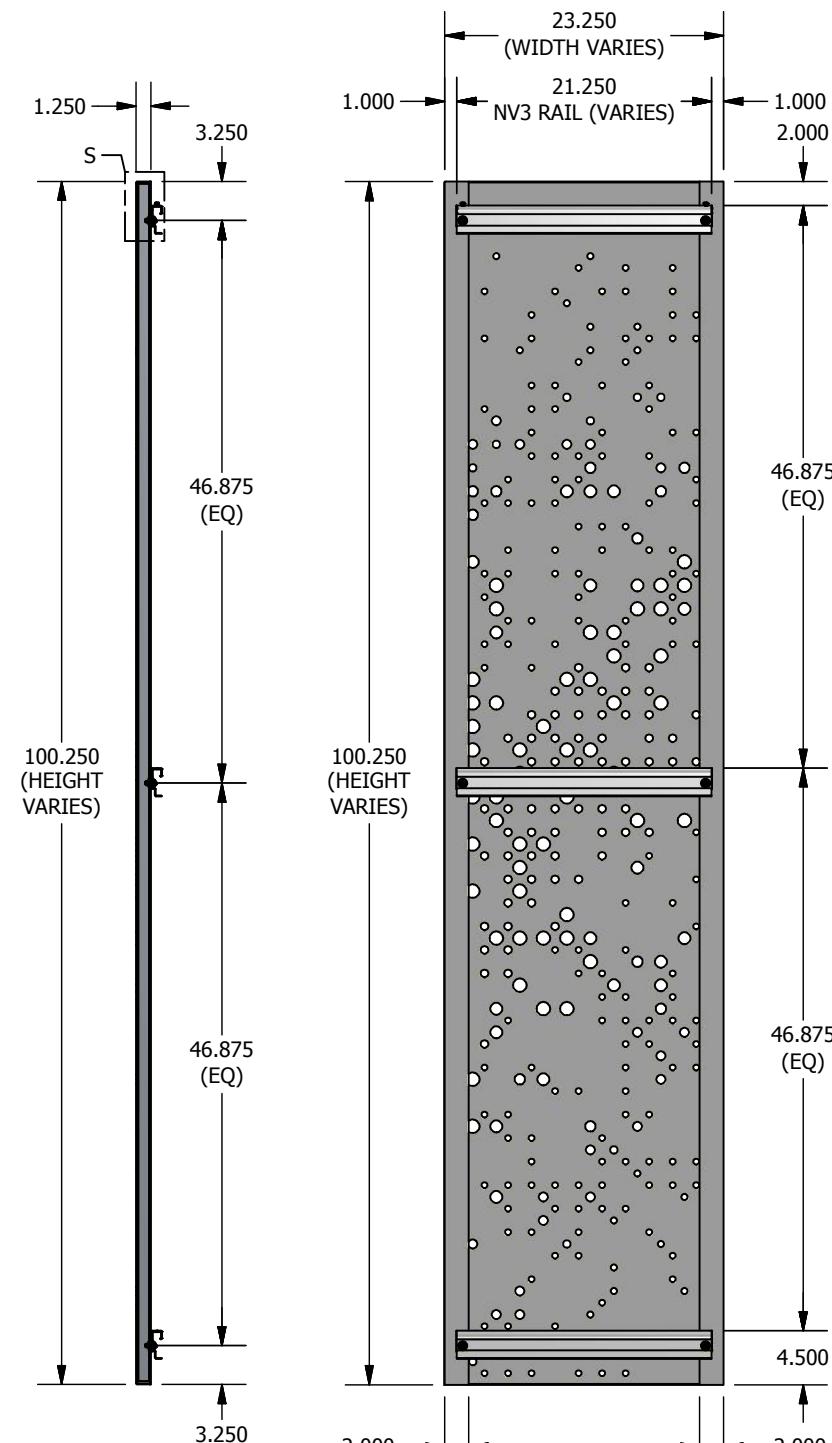SECTION B7-B7  
SCALE 1 / 16

PART TAG:	'2-FT' PANELS: PANEL ID PER TABLE	ISSUE DATE	REVISION
QT:	(QTY) PER TABLE (SHEET 9)	7/28/2016	A
MATERIAL:	2.00MM ZINC	SCALE	SHEET NUMBER
FINISH:	ZINC - NATURAL; ALUM. - BLACK ANOD.	(AS SHOWN)	10 / 37
FLAT FILE:			



ARCHITECTURAL METAL FABRICATION  
59-20 56TH AVE.  
MASPETH, NY 11378  
(718) 894-1212

**CONTRACTOR**

325 KENT CONSTRUCTION LLC

**ARCHITECT**

ISMAEL LEYVA

**PROJECT #**

DOMINO SITE E

**ITEM**

FAÇADE

**DRAWING**

16001\_ZINC PANEL TYPES

**DRAWN CHECKED**

SP

**ISSUE DATE REVISION**

7/28/2016 A

**SCALE SHEET NUMBER**


10 / 37

8




7

6

PANEL ID	PANEL TYPE	BEND PROFILE	WIDTH (IN)	HEIGHT (IN)	PANEL TYPE (QTY)
Z02F-1-000	VERTICAL	TYPE 1	23.25	96.75	7
Z02F-1-001	VERTICAL	TYPE 1	23.25	100.25	9
Z02F-1-002	VERTICAL	TYPE 1	35.25	100.25	1
Z02F-1-003	VERTICAL	TYPE 1	23.25	112.25	2
Z02F-2-000	VERTICAL	TYPE 1	23.25	96.75	4
Z02F-2-001	VERTICAL	TYPE 1	23.25	100.25	10
Z02F-2-002	VERTICAL	TYPE 1	22.75	108.125	1
PANEL TOTAL					34

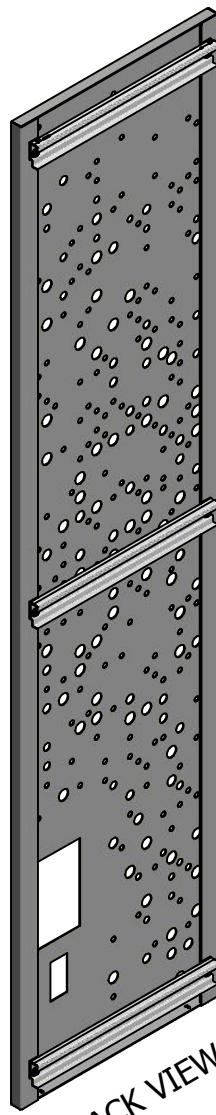**Z02F-1-001 (SHOWN)****\*HOLD FOR LIGHT FIXTURE APPROVED DRAWING**

BACK VIEW

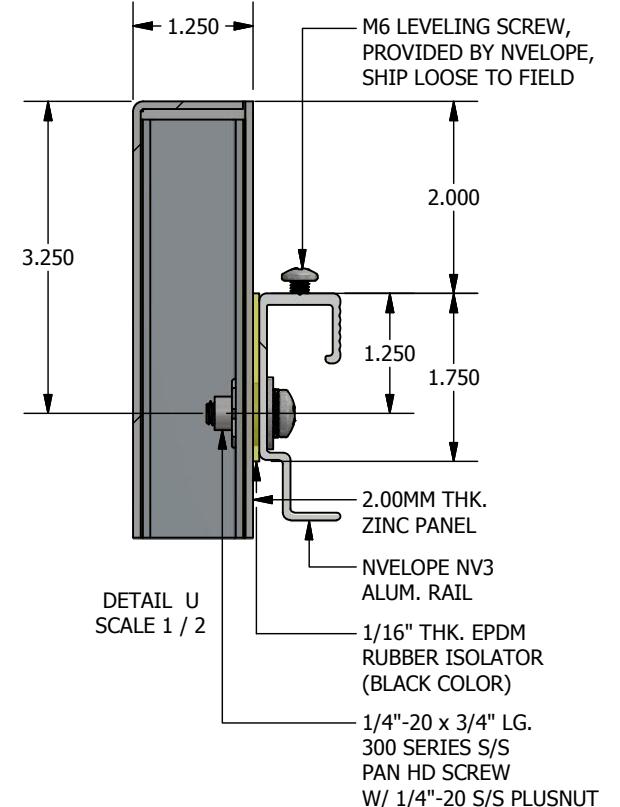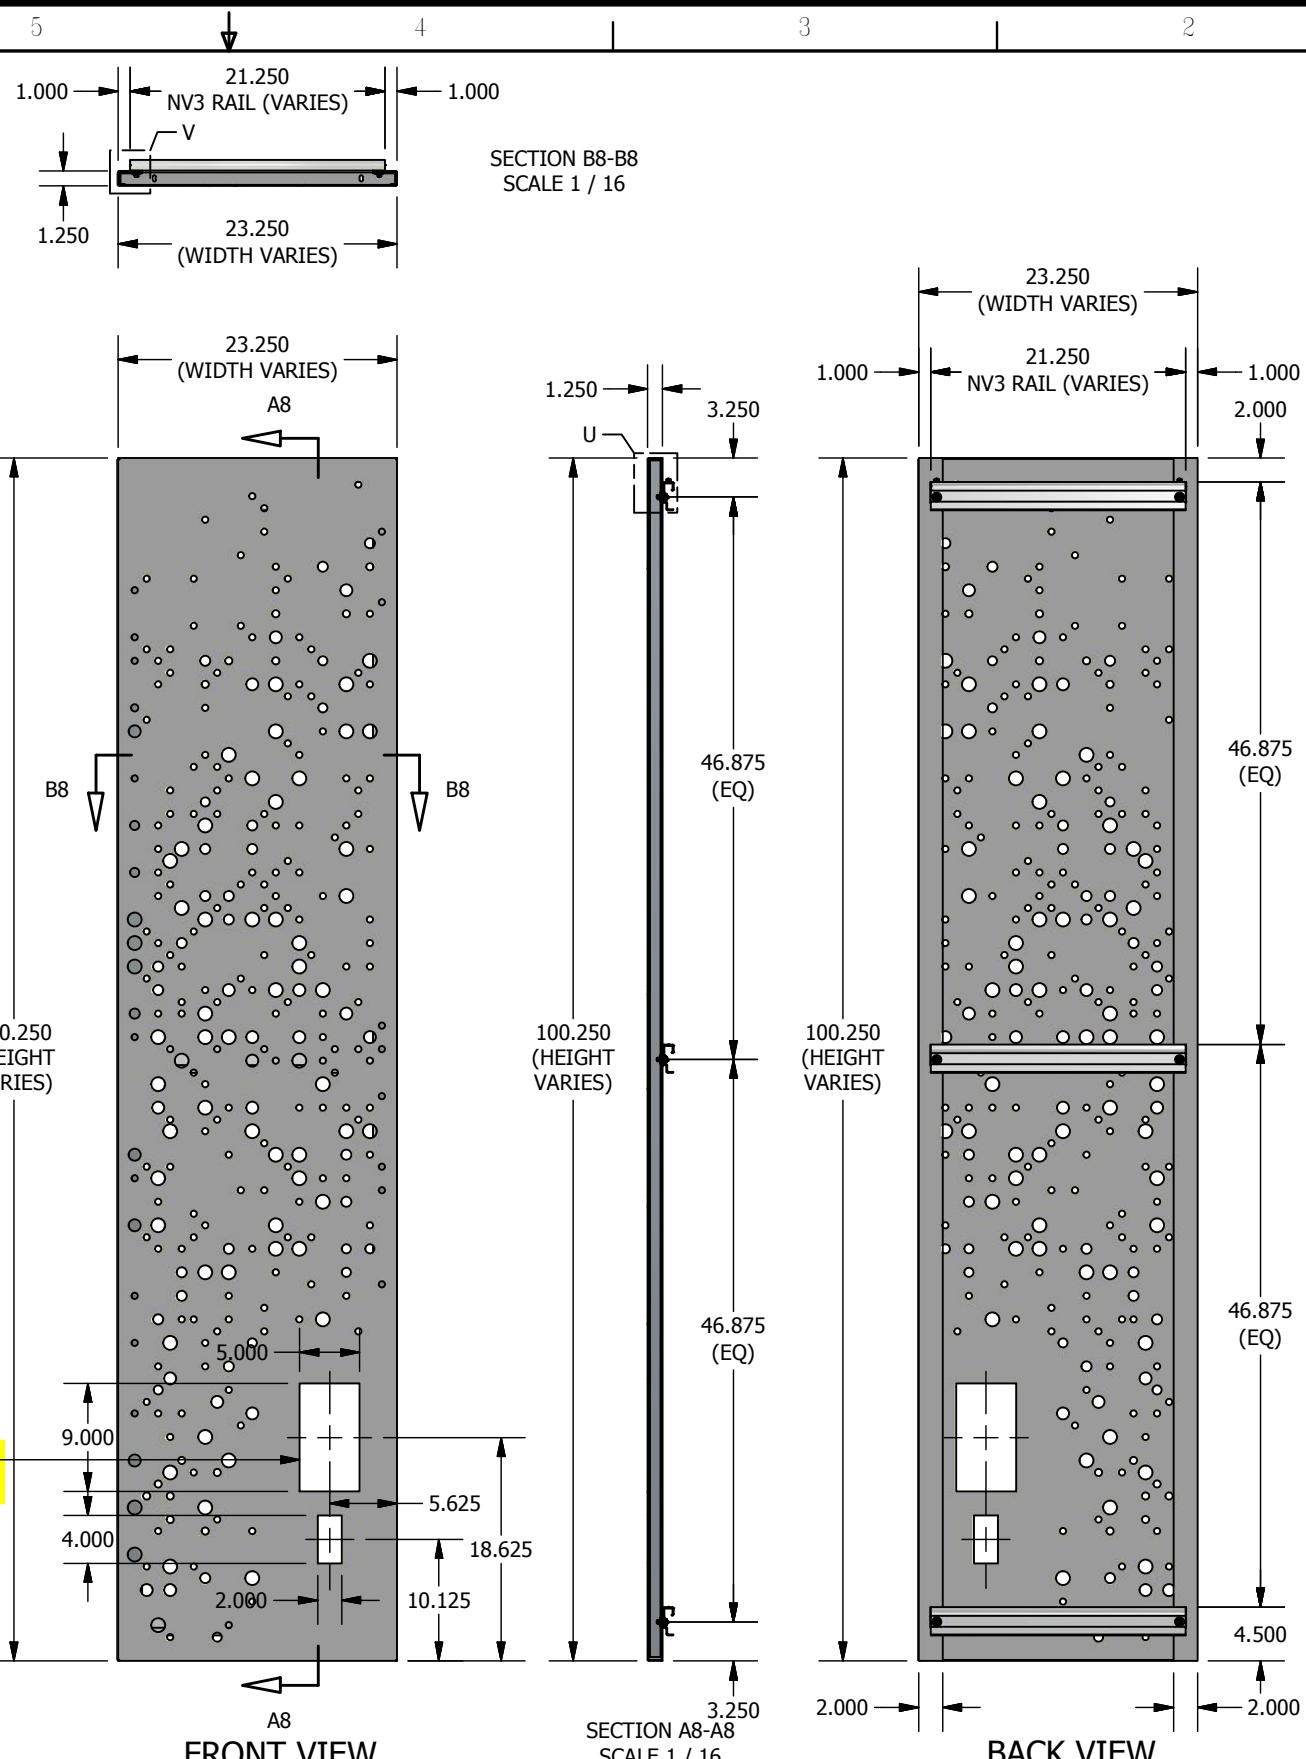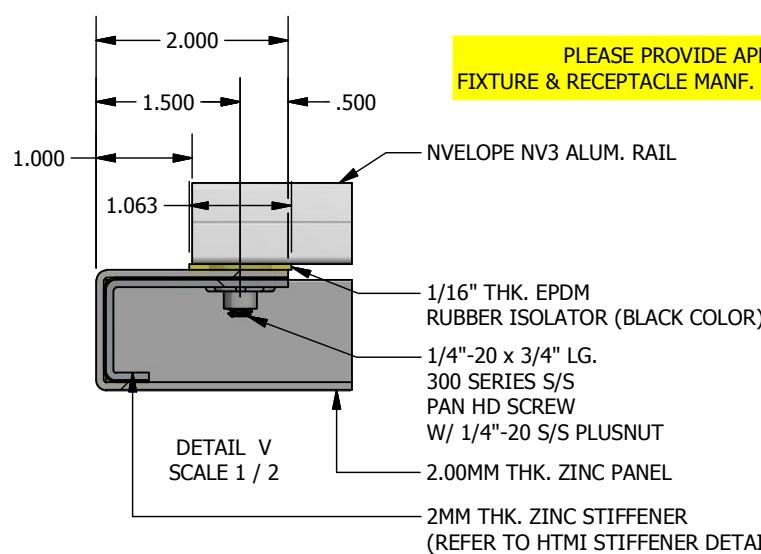PLEASE PROVIDE APPROVED LIGHT  
FIXTURE & RECEPTACLE MANF. CUT DRAWING

FRONT VIEW

BACK VIEW

PART TAG:	Z02F '2-FT' PANELS: PANEL ID PER TABLE	ISSUE DATE	REVISION
QT:	(QTY) PER TABLE	7/28/2016	A
MATERIAL:	2.00MM ZINC	SCALE	SHEET NUMBER
FINISH:	ZINC - NATURAL; ALUM. - BLACK ANOD.	(AS SHOWN)	11 / 37
FLAT FILE:			



ARCHITECTURAL METAL FABRICATION  
59-20 56TH AVE.  
MASPETH, NY 11378  
(718) 894-1212

**CONTRACTOR**

325 KENT CONSTRUCTION LLC

**ARCHITECT**

ISMAEL LEYVA

**PROJECT #**

DOMINO SITE E

**ITEM**

FAÇADE

**DRAWING**

16001\_ZINC PANEL TYPES

**DRAWN**      **CHECKED**

SP

8

7

6

5

4

3

2

1



## '3-FT' VERTICAL PANEL TABLE

PANEL ID	PANEL TYPE	BEND PROFILE	WIDTH (IN)	HEIGHT (IN)	PANEL TYPE (QTY)
Z03A-1-000	VERTICAL	TYPE 1	35.25	96.75	16
Z03A-1-001	VERTICAL	TYPE 1	35.25	100.25	243
Z03A-1-002	VERTICAL	TYPE 1	27.25	100.25	1
Z03A-1-003	VERTICAL	TYPE 1	35.625	100.25	2
Z03A-1-005	VERTICAL	TYPE 1	27.125	100.25	3
Z03A-1-006	VERTICAL	TYPE 1	35.25	108.125	1
Z03A-1-007	VERTICAL	TYPE 1	33.125	100.25	2
Z03A-1-008	VERTICAL	TYPE 1	32.75	108.125	1
Z03A-1-009	VERTICAL	TYPE 1	35.25	88.5625	4
Z03A-1-010	VERTICAL	TYPE 1	35.25	112.25	14
Z03A-1-011	VERTICAL	TYPE 1	35.25	131.25	2
Z03A-1-012	VERTICAL	TYPE 1	35.25	133.5	1
Z03A-1-013	VERTICAL	TYPE 1	35.25	129.75	2
Z03A-2-000	VERTICAL	TYPE 1	35.25	96.75	13
Z03A-2-001	VERTICAL	TYPE 1	35.25	100.25	230
Z03A-2-002	VERTICAL	TYPE 1	29.25	100.25	2
Z03A-2-004	VERTICAL	TYPE 1	27.125	100.25	1
Z03A-2-005	VERTICAL	TYPE 1	35.625	100.25	1
Z03A-2-007	VERTICAL	TYPE 1	35.25	108.125	3
Z03A-2-010	VERTICAL	TYPE 1	33.125	100.25	1
Z03A-2-011	VERTICAL	TYPE 1	35.25	112.25	18
Z03A-2-012	VERTICAL	TYPE 1	35.25	88.5625	2
Z03A-2-014	VERTICAL	TYPE 1	34.75	100.25	1
Z03A-2-015	VERTICAL	TYPE 1	33.625	100.25	1
Z03A-2-016	VERTICAL	TYPE 1	35.25	129.75	1
Z03A-3-001	VERTICAL	TYPE 1	35.25	100.25	3
Z03A-3-002	VERTICAL	TYPE 1	35.25	108.125	1
Z03A-3-003	VERTICAL	TYPE 1	35.25	112.25	1
Z03A-3-005	VERTICAL	TYPE 1	29	133.5	1
Z03A-3-006	VERTICAL	TYPE 1	32.25	133.5	1
Z03A-3-007	VERTICAL	TYPE 1	32.75	133.5	1
Z03A-3-008	VERTICAL	TYPE 1	35.25	133.5	1
Z03A-3-009	VERTICAL	TYPE 1	37.25	87.4375	1
Z03A-3-010	VERTICAL	TYPE 1	35.25	129.75	3
Z03A-4-001	VERTICAL	TYPE 1	35.25	108.125	1
Z03A-4-002	VERTICAL	TYPE 1	35.25	112.25	1
Z03A-4-003	VERTICAL	TYPE 1	35.25	133.75	1
Z03A-4-004	VERTICAL	TYPE 1	37.25	31.75	1
Z03A-4-005	VERTICAL	TYPE 1	35.25	133.5	1
Z03A-4-006	VERTICAL	TYPE 1	37.25	87.4375	1
Z03B-1-000	VERTICAL	TYPE 1	35.25	96.75	6
Z03B-1-001	VERTICAL	TYPE 1	39.1875	96.75	1
Z03B-1-002	VERTICAL	TYPE 1	28.9375	96.75	1
Z03B-1-003	VERTICAL	TYPE 1	35.25	100.25	66
Z03B-1-004	VERTICAL	TYPE 1	34.875	100.25	1
Z03B-1-005	VERTICAL	TYPE 1	35.25	108.125	1
Z03B-1-006	VERTICAL	TYPE 1	33.625	100.25	4
Z03B-1-007	VERTICAL	TYPE 1	35.625	100.25	1
Z03B-1-008	VERTICAL	TYPE 1	27.125	100.25	2
Z03B-1-009	VERTICAL	TYPE 1	35.25	112.25	5
Z03B-1-010	VERTICAL	TYPE 1	33.625	112.25	1
Z03B-1-011	VERTICAL	TYPE 1	29.25	120.125	1
Z03B-1-012	VERTICAL	TYPE 1	35.25	88.5625	1
Z03B-1-013	VERTICAL	TYPE 1	19.125	100.25	1
Z03B-1-014	VERTICAL	TYPE 1	37.0625	115.25	1
Z03B-1-015	VERTICAL	TYPE 1	37.25	115.25	2
Z03B-1-016	VERTICAL	TYPE 1	35.25	129.75	1
Z03B-1-017	VERTICAL	TYPE 1	16.25	129.75	1
Z03B-2-000	VERTICAL	TYPE 1	24.9375	96	1
Z03B-2-001	VERTICAL	TYPE 1	35.25	96.75	4
Z03B-2-002	VERTICAL	TYPE 1	33.25	99.5	1
Z03B-2-003	VERTICAL	TYPE 1	35.25	100.25	54
Z03B-2-005	VERTICAL	TYPE 1	35.25	108.125	1

PANEL ID	PANEL TYPE	BEND PROFILE	WIDTH (IN)	HEIGHT (IN)	PANEL TYPE (QTY)
Z03B-2-008	VERTICAL	TYPE 1	33.625	100.25	3
Z03B-2-009	VERTICAL	TYPE 1	31.625	100.25	1
Z03B-2-011	VERTICAL	TYPE 1	33.125	100.25	1
Z03B-2-012	VERTICAL	TYPE 1	31.6875	108.125	1
Z03B-2-014	VERTICAL	TYPE 1	35.25	112.25	6
Z03B-2-015	VERTICAL	TYPE 1	35	120.125	1
Z03B-2-017	VERTICAL	TYPE 1	33.625	112.25	1
Z03B-2-018	VERTICAL	TYPE 1	35.25	88.5625	1
Z03B-2-019	VERTICAL	TYPE 1	27.25	131.25	1
Z03B-2-020	VERTICAL	TYPE 1	35.25	131.25	1
Z03B-2-021	VERTICAL	TYPE 1	25.3125	133.5	1
Z03B-2-022	VERTICAL	TYPE 1	35.25	129.75	2
Z03B-3-000	VERTICAL	TYPE 1	35.25	96.75	1
Z03B-3-001	VERTICAL	TYPE 1	35.25	100.25	3
Z03B-3-002	VERTICAL	TYPE 1	37.25	24.125	1
Z03B-3-003	VERTICAL	TYPE 1	28.5	108.125	1
Z03B-3-005	VERTICAL	TYPE 1	30.5	108.125	1
Z03B-3-007	VERTICAL	TYPE 1	35.25	133.5	2
Z03B-3-008	VERTICAL	TYPE 1	35.25	133.5	1
Z03B-3-009	VERTICAL	TYPE 1	32.25	129.75	1
Z03B-4-000	VERTICAL	TYPE 1	35.25	96.75	1
Z03B-4-001	VERTICAL	TYPE 1	35.25	100.25	2
Z03B-4-002	VERTICAL	TYPE 1	33.125	100.25	1
Z03B-4-004	VERTICAL	TYPE 1	37	25.125	1
Z03B-4-005	VERTICAL	TYPE 1	37.25	31.75	1
Z03B-4-006	VERTICAL	TYPE 1	35.25	133.5	6
Z03B-4-007	VERTICAL	TYPE 1	31	133.5	1
Z03B-4-008	VERTICAL	TYPE 1	37.25	115.25	1
Z03C-1-000	VERTICAL	TYPE 1	35.25	96.75	4
Z03C-1-001	VERTICAL	TYPE 1	35.25	100.25	38
Z03C-1-002	VERTICAL	TYPE 1	33.125	100.25	1
Z03C-1-003	VERTICAL	TYPE 1	35.25	108.125	1
Z03C-1-005	VERTICAL	TYPE 1	35.25	112.25	5
Z03C-1-006	VERTICAL	TYPE 1	29.25	100.25	1
Z03C-1-007	VERTICAL	TYPE 1	35.25	131.25	1
Z03C-2-000	VERTICAL	TYPE 1	35.25	100.25	32
Z03C-2-001	VERTICAL	TYPE 1	28.625	100.25	1
Z03C-2-003	VERTICAL	TYPE 1	35.25	112.25	2
Z03C-2-004	VERTICAL	TYPE 1	31	133.5	1
Z03C-2-005	VERTICAL	TYPE 1	35.25	129.75	1
Z03C-3-000	VERTICAL	TYPE 1	35.25	96.75	1
Z03C-3-001	VERTICAL	TYPE 1	35.25	100.25	6
Z03C-3-002	VERTICAL	TYPE 1	35.25	108.125	1
Z03C-3-003	VERTICAL	TYPE 1	35.25	133.75	1
Z03C-3-004	VERTICAL	TYPE 1	35.25	133.5	3
Z03C-3-005	VERTICAL	TYPE 1	34.75	133.5	1
Z03C-3-006	VERTICAL	TYPE 1	29.25	133.5	1
Z03C-3-008	VERTICAL	TYPE 1	37.25	87.4375	2
Z03C-4-000	VERTICAL	TYPE 1	35.25	100.25	3
Z03C-4-001	VERTICAL	TYPE 1	35.25	108.125	1
Z03C-4-002	VERTICAL	TYPE 1</td			

8 7 6 5 4 3 2 1

**'3-FT' VERTICAL PANEL**  
**Z03A-1-001 (SHOWN)**

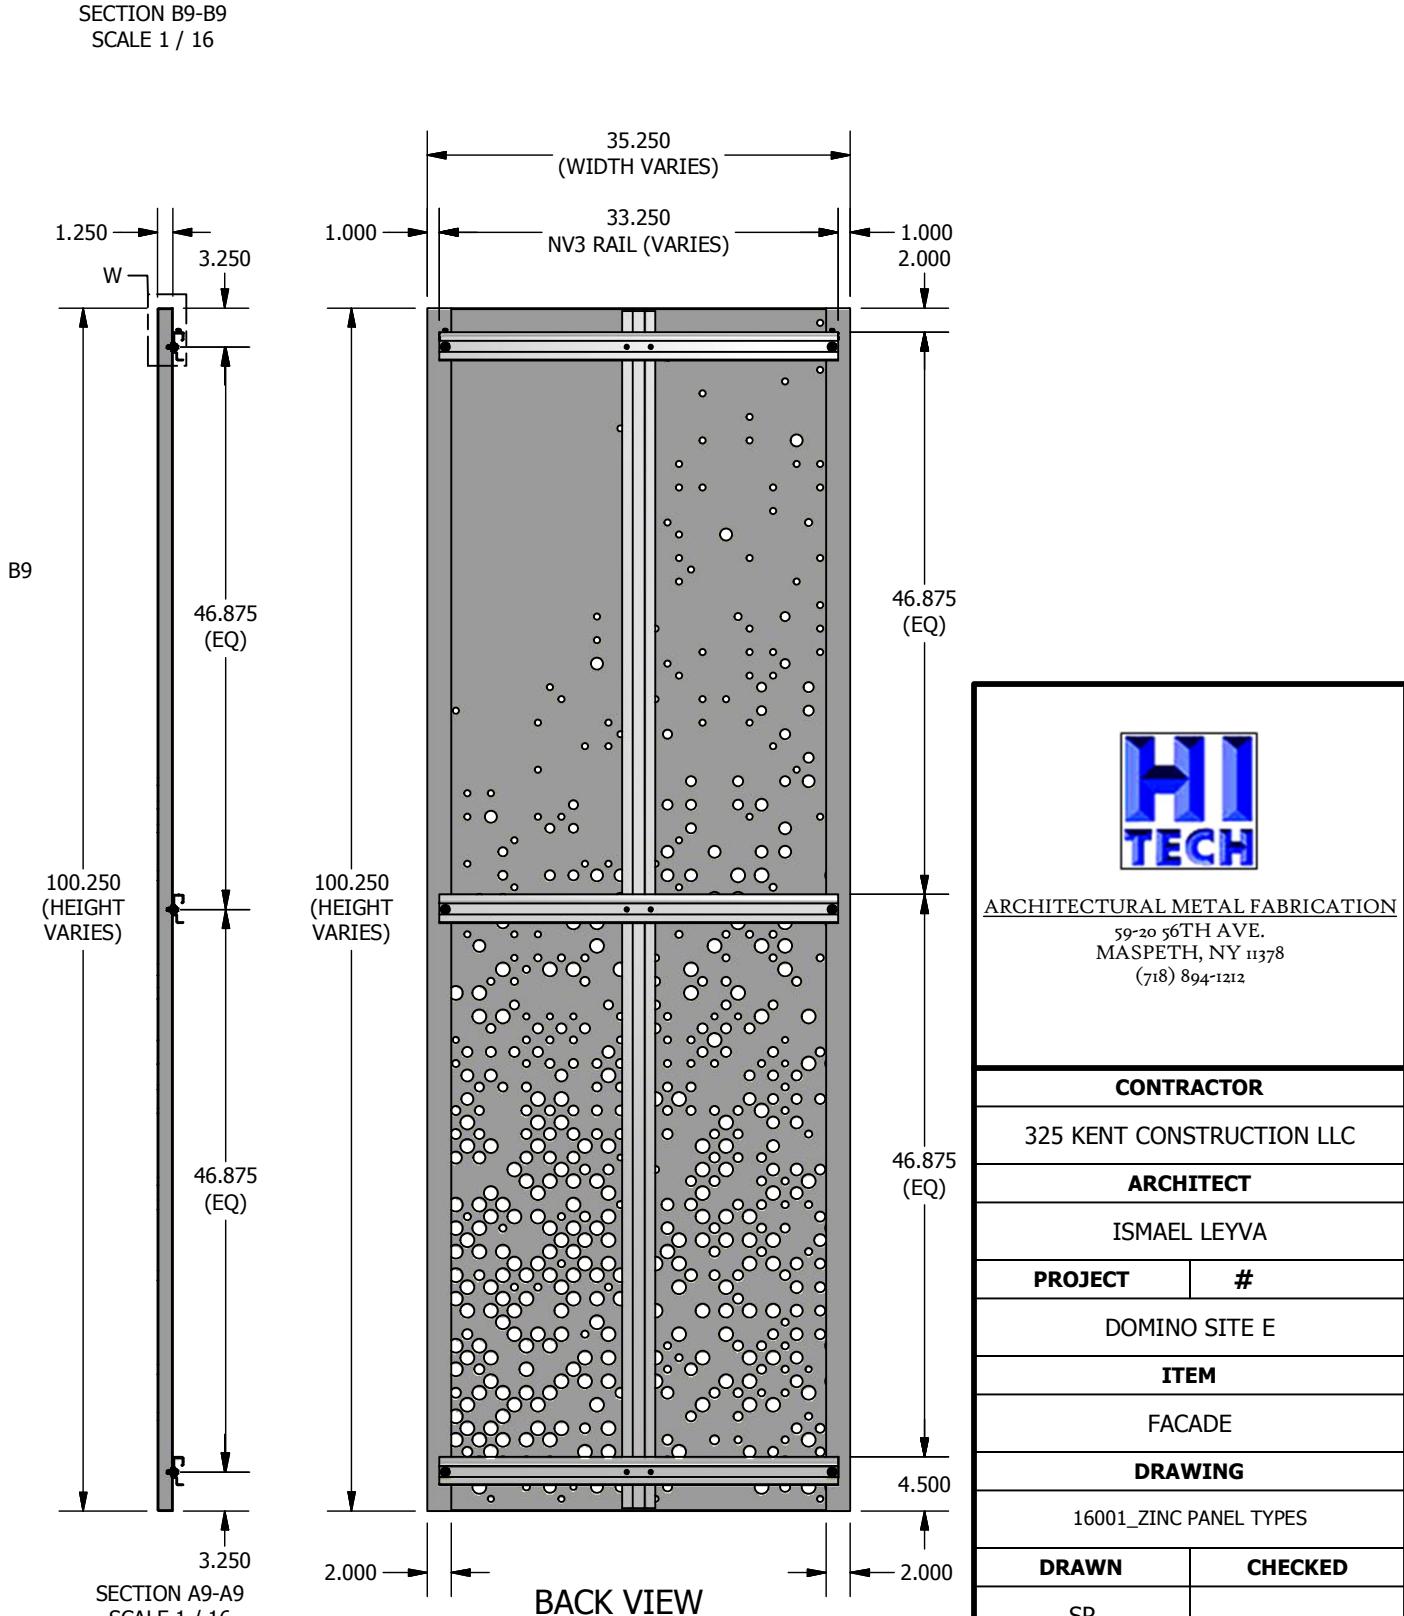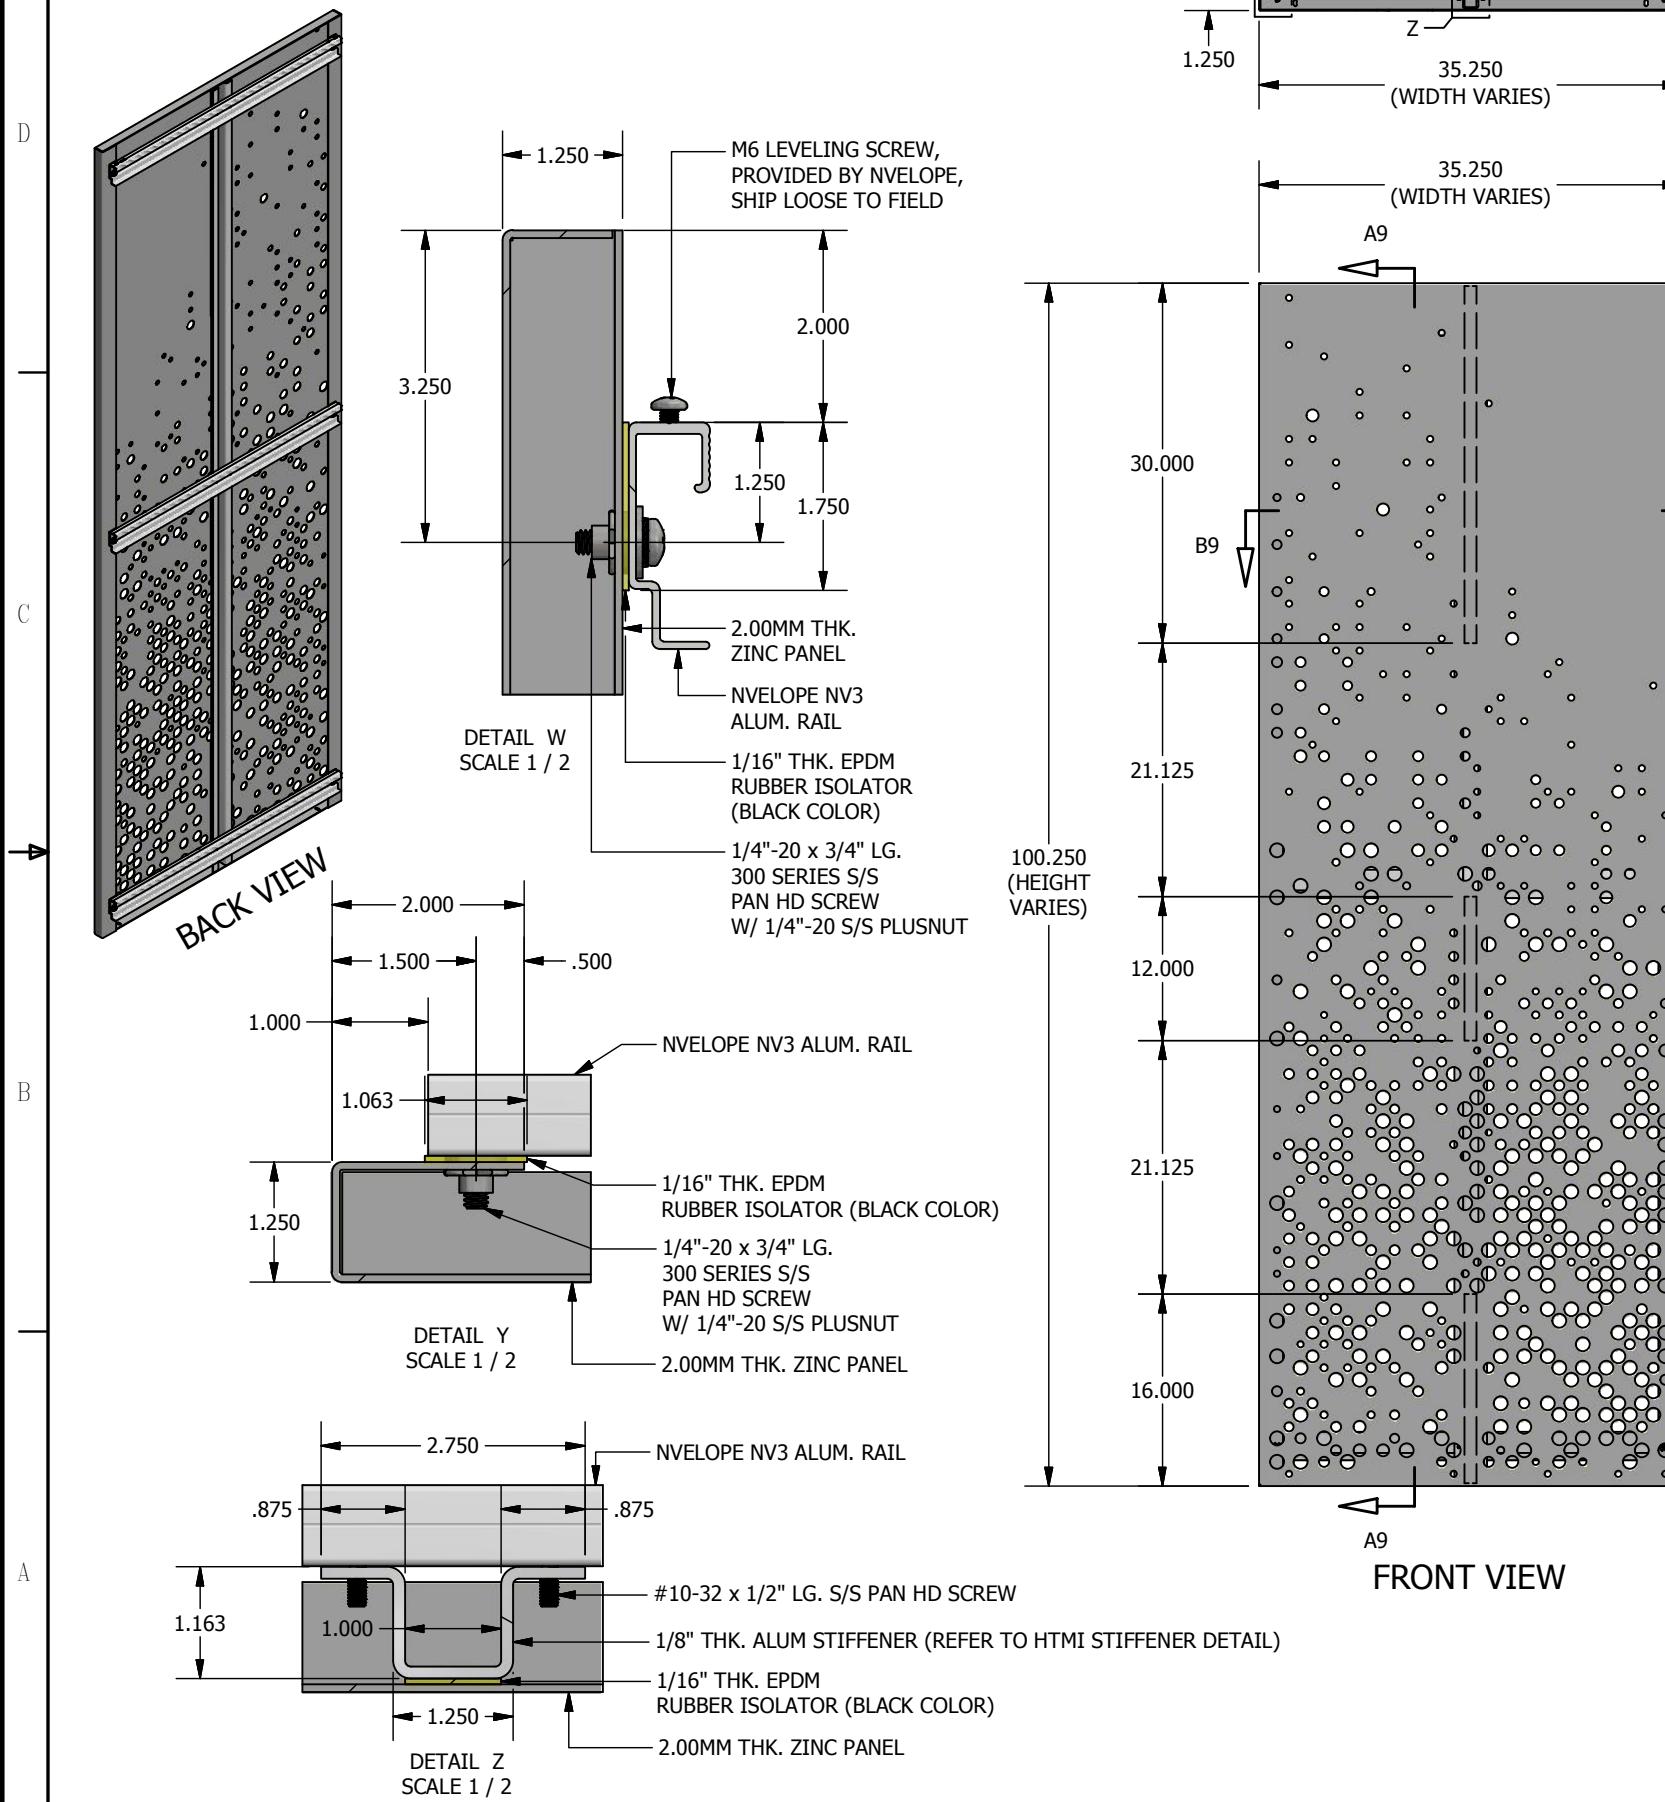

ARCHITECTURAL METAL FABRICATION  
59-20 56TH AVE.  
MASPETH, NY 11378  
(718) 894-1212

**CONTRACTOR**

325 KENT CONSTRUCTION LLC

**ARCHITECT**

ISMAEL LEYVA

**PROJECT #**

DOMINO SITE E

**ITEM**

FACADE

**DRAWING**

16001\_ZINC PANEL TYPES

<b>DRAWN</b>	<b>CHECKED</b>
SP	

<b>ISSUE DATE</b>	<b>REVISION</b>
7/28/2016	A
<b>SCALE</b>	<b>SHEET NUMBER</b>
(AS SHOWN)	13 / 37


PART TAG:	'3-FT' PANELS: PANEL ID PER TABLE
QT:	(QTY) PER TABLE (SHEET 12)
MATERIAL:	2.00MM ZINC
FINISH:	ZINC - NATURAL; ALUM. - BLACK ANOD.
FLAT FILE:	

8 7 6 5 4 3 2 1


PANEL ID	PANEL TYPE	BEND PROFILE	WIDTH (IN)	HEIGHT (IN)	PANEL TYPE (QTY)
Z03F-1-000	VERTICAL	TYPE 1	35.25	96.75	2
Z03F-1-001	VERTICAL	TYPE 1	35.25	100.25	6
Z03F-1-002	VERTICAL	TYPE 1	35.25	108.125	1
Z03F-2-000	VERTICAL	TYPE 1	35.25	96.75	2
Z03F-2-001	VERTICAL	TYPE 1	35.25	100.25	1
PANEL TOTAL					12

SECTION B10-B10  
SCALE 1 / 16**Z03F-1-001 (SHOWN)**


\*HOLD FOR LIGHT FIXTURE APPROVED DRAWING

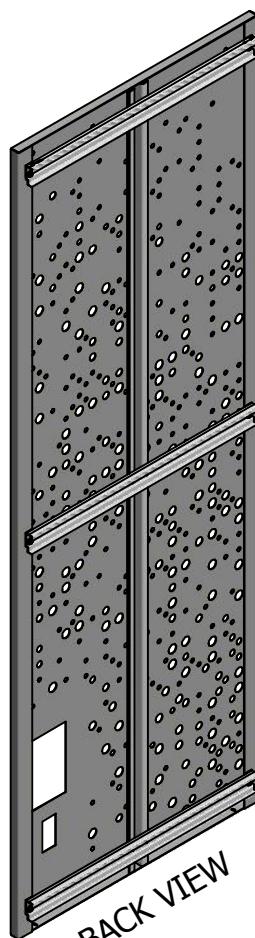



BACK VIEW

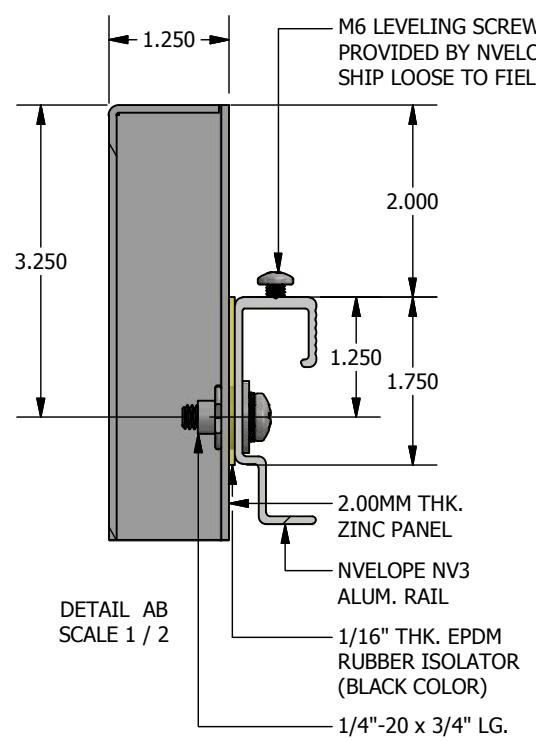DETAIL AB  
SCALE 1 / 2


- M6 LEVELING SCREW, PROVIDED BY NVELOPE, SHIP LOOSE TO FIELD
- 2.00MM THK. ZINC PANEL
- NVELOPE NV3 ALUM. RAIL
- 1/16" THK. EPDM RUBBER ISOLATOR (BLACK COLOR)
- 1/4"-20 x 3/4" LG. 300 SERIES S/S PAN HD SCREW W/ 1/4"-20 S/S PLUSNUT

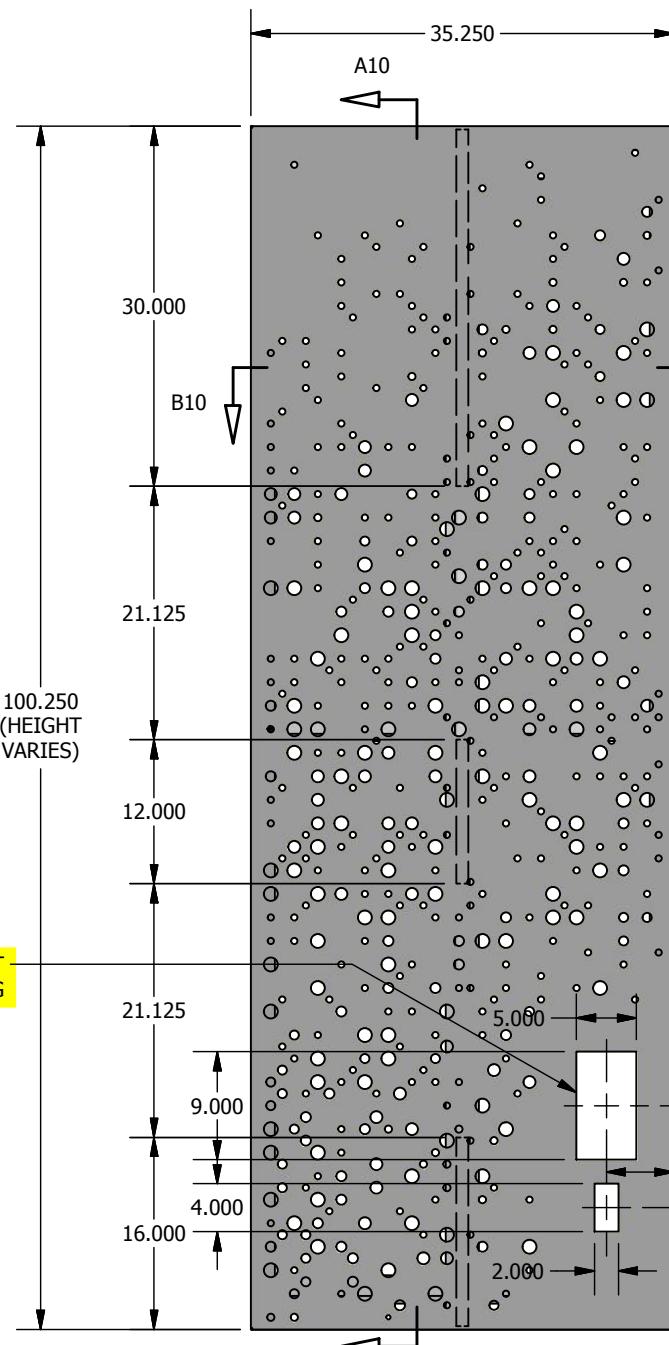


FRONT VIEW

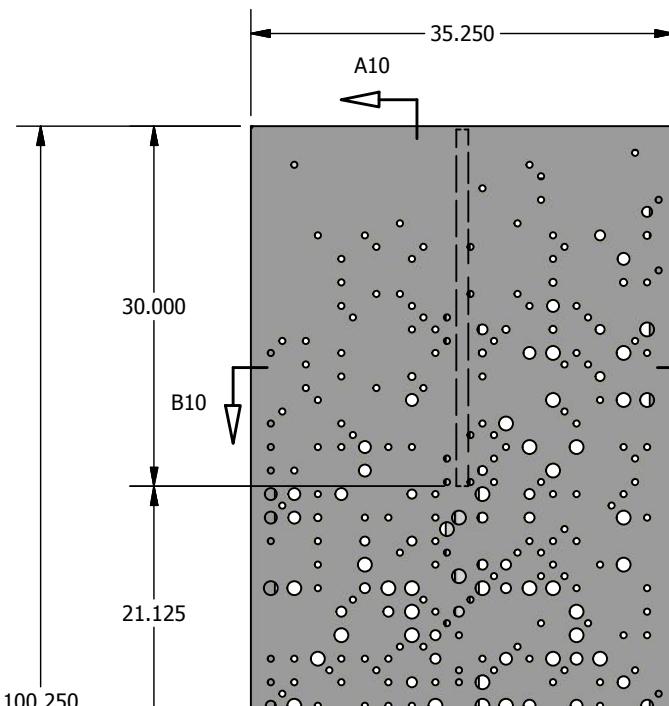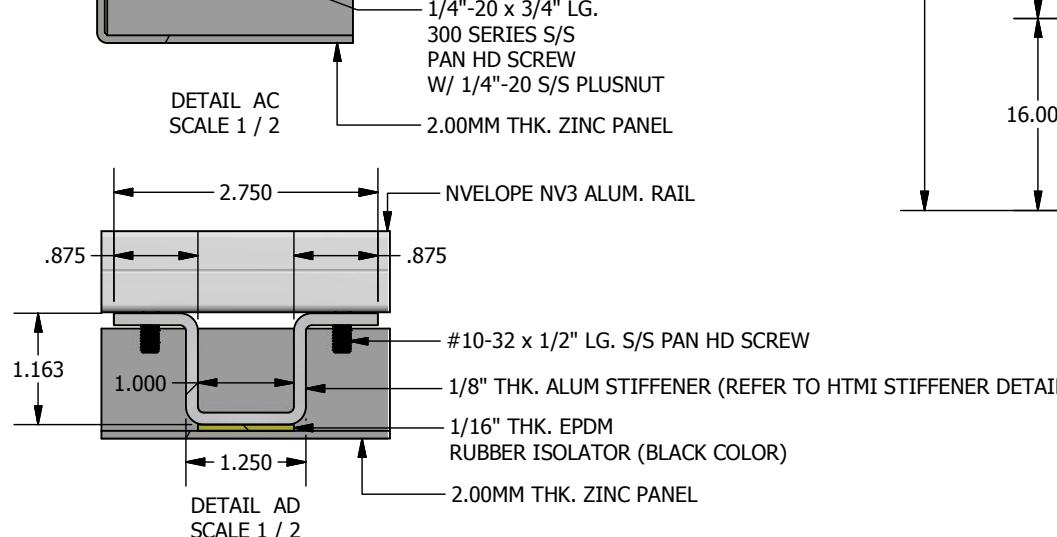SECTION A10-A10  
SCALE 1 / 16DETAIL AD  
SCALE 1 / 2

- #10-32 x 1/2" LG. S/S PAN HD SCREW
- 1/8" THK. ALUM STIFFENER (REFER TO HTMI STIFFENER DETAIL)
- 1/16" THK. EPDM RUBBER ISOLATOR (BLACK COLOR)
- 2.00MM THK. ZINC PANEL

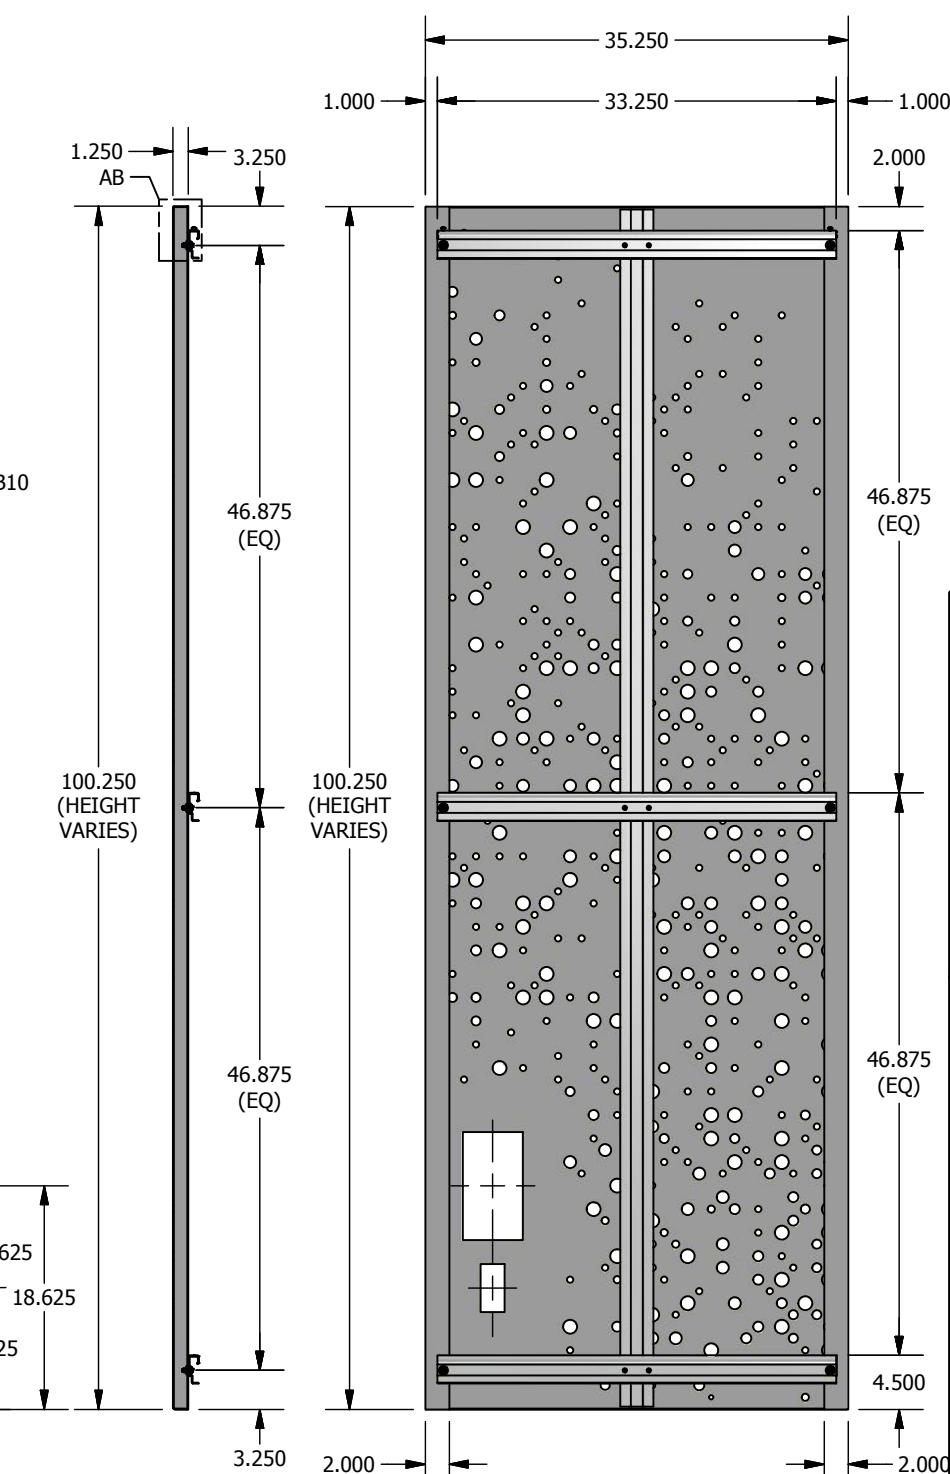

BACK VIEW

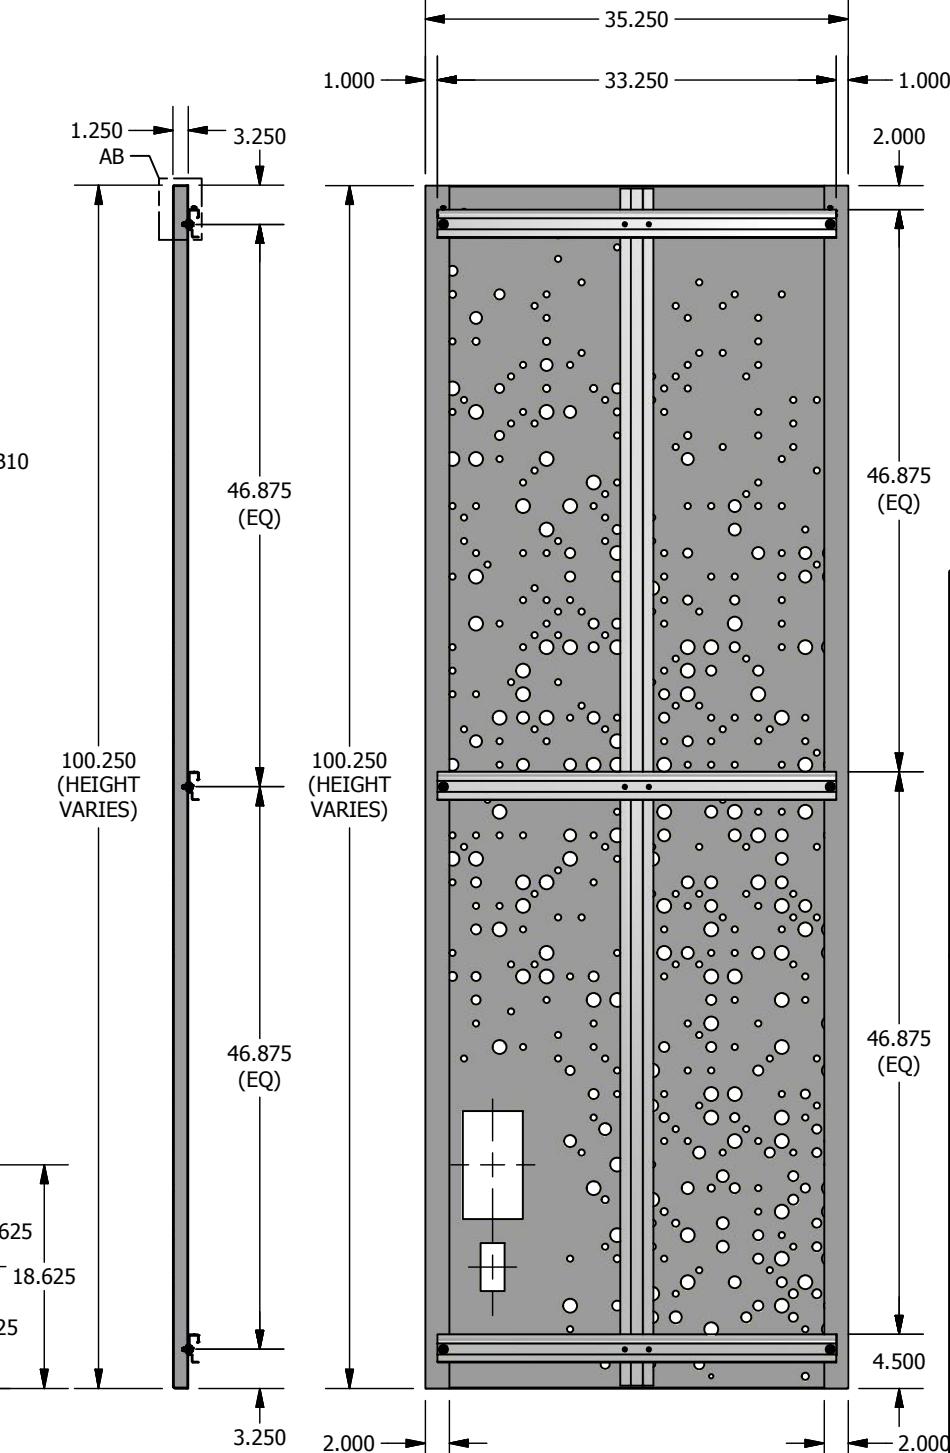

PART TAG:	Z03F '3-FT' PANELS: PANEL ID PER TABLE
QT:	(QTY) PER TABLE
MATERIAL:	2.00MM ZINC
FINISH:	ZINC - NATURAL; ALUM. - BLACK ANOD.
FLAT FILE:	



ARCHITECTURAL METAL FABRICATION  
59-20 56TH AVE.  
MASPETH, NY 11378  
(718) 894-1212

**CONTRACTOR**

325 KENT CONSTRUCTION LLC

**ARCHITECT**

ISMAEL LEYVA

**PROJECT #**

DOMINO SITE E

**ITEM**

FAÇADE

**DRAWING**

16001\_ZINC PANEL TYPES

**DRAWN**

SP

**CHECKED****ISSUE DATE**

7/28/2016

**REVISION**

A

**SCALE****SHEET NUMBER**

(AS SHOWN)

14 / 37

8 7 6 5 4 3 2 1

## CORNER LEFT VERTICAL PANEL TABLE

PANEL ID	PANEL TYPE	BEND PROFILE	WIDTH (IN)	HEIGHT (IN)	PANEL TYPE (QTY)
Z01B-3-012	VERTICAL	TYPE 1_CL	11.625	131.875	1
Z01B-3-014	VERTICAL	TYPE 1_CL	11.625	131.25	1
Z02A-1-004	VERTICAL	TYPE 1_CL	23.625	100.25	4
Z02A-1-007	VERTICAL	TYPE 1_CL	19.625	100.25	1
Z02A-1-008	VERTICAL	TYPE 1_CL	21.625	100.25	1
Z02A-1-013	VERTICAL	TYPE 1_CL	22.125	100.25	1
Z02A-1-014	VERTICAL	TYPE 1_CL	25.625	100.25	1
Z02A-1-019	VERTICAL	TYPE 1_CL	15.625	100.25	1
Z02A-1-025	VERTICAL	TYPE 1_CL	16.625	131.25	1
Z02A-1-033	VERTICAL	TYPE 1_CL	16.625	129.75	1
Z02A-2-007	VERTICAL	TYPE 1_CL	23.625	100.25	1
Z02A-2-020	VERTICAL	TYPE 1_CL	23.8125	100.25	1
Z02A-2-028	VERTICAL	TYPE 1_CL	23.625	129.75	1
Z02A-3-002	VERTICAL	TYPE 1_CL	23.625	100.25	1
Z02A-3-004	VERTICAL	TYPE 1_CL	21.125	108.125	1
Z02A-3-009	VERTICAL	TYPE 1_CL	21.875	133.75	1
Z02A-3-010	VERTICAL	TYPE 1_CL	21.625	131.25	1
Z02B-1-011	VERTICAL	TYPE 1_CL	27.625	112.25	1
Z02B-2-002	VERTICAL	TYPE 1_CL	23.625	100.25	2
Z02B-2-005	VERTICAL	TYPE 1_CL	21.625	100.25	1
Z02B-4-001	VERTICAL	TYPE 1_CL	23.625	100.25	1
Z02C-1-004	VERTICAL	TYPE 1_CL	23.625	108.125	1
Z02C-2-002	VERTICAL	TYPE 1_CL	23.625	100.25	3
Z02C-4-001	VERTICAL	TYPE 1_CL	22.125	108.125	1
Z03A-1-003	VERTICAL	TYPE 1_CL	35.625	100.25	1
Z03A-1-004	VERTICAL	TYPE 1_CL	28.125	100.25	1
Z03A-2-006	VERTICAL	TYPE 1_CL	27.625	100.25	1
Z03A-4-000	VERTICAL	TYPE 1_CL	35.625	100.25	1
Z03B-2-006	VERTICAL	TYPE 1_CL	29.625	100.25	2
Z03B-2-007	VERTICAL	TYPE 1_CL	36.125	100.25	1
Z03B-2-013	VERTICAL	TYPE 1_CL	35.625	88.5625	1
Z03B-2-016	VERTICAL	TYPE 1_CL	35.625	112.25	2
Z03B-3-006	VERTICAL	TYPE 1_CL	29.375	133.75	1
Z03B-4-003	VERTICAL	TYPE 1_CL	32.875	108.125	1
Z03B-4-009	VERTICAL	TYPE 1_CL	23.625	129.75	1
Z03C-1-004	VERTICAL	TYPE 1_CL	35.625	100.25	1
Z03C-3-007	VERTICAL	TYPE 1_CL	37.625	133.5	1
TOTAL PANEL					45



ARCHITECTURAL METAL FABRICATION

59-20 56TH AVE.  
MASPETH, NY 11378  
(718) 894-1212

CONTRACTOR

325 KENT CONSTRUCTION LLC

ARCHITECT

ISMAEL LEYVA

PROJECT	#
---------	---

DOMINO SITE E

ITEM

FAÇADE

DRAWING

16001\_ZINC PANEL TYPES

DRAWN	CHECKED
-------	---------

SP

ISSUE DATE	REVISION
------------	----------

7/28/2016

A


SCALE	SHEET NUMBER
-------	--------------

(AS SHOWN)





15 / 37

PART TAG:	
QT:	
MATERIAL:	
FINISH:	
FLAT FILE:	

8 7 6 5 4 3 2 1

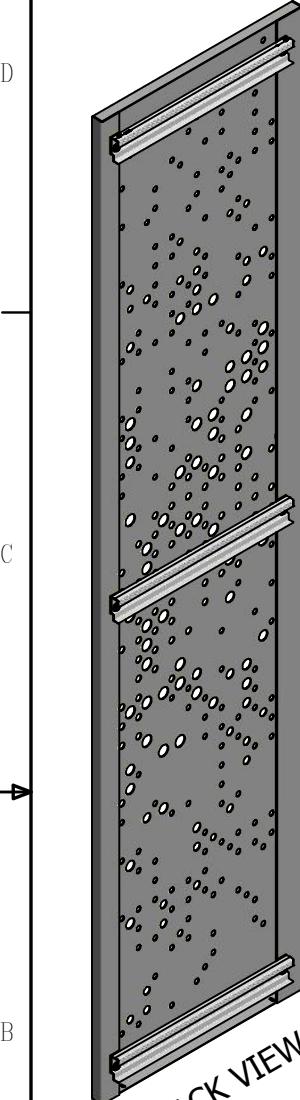**CORNER LEFT VERTICAL PANEL**  
**Z02A-1-004 (SHOWN)**


BACK VIEW

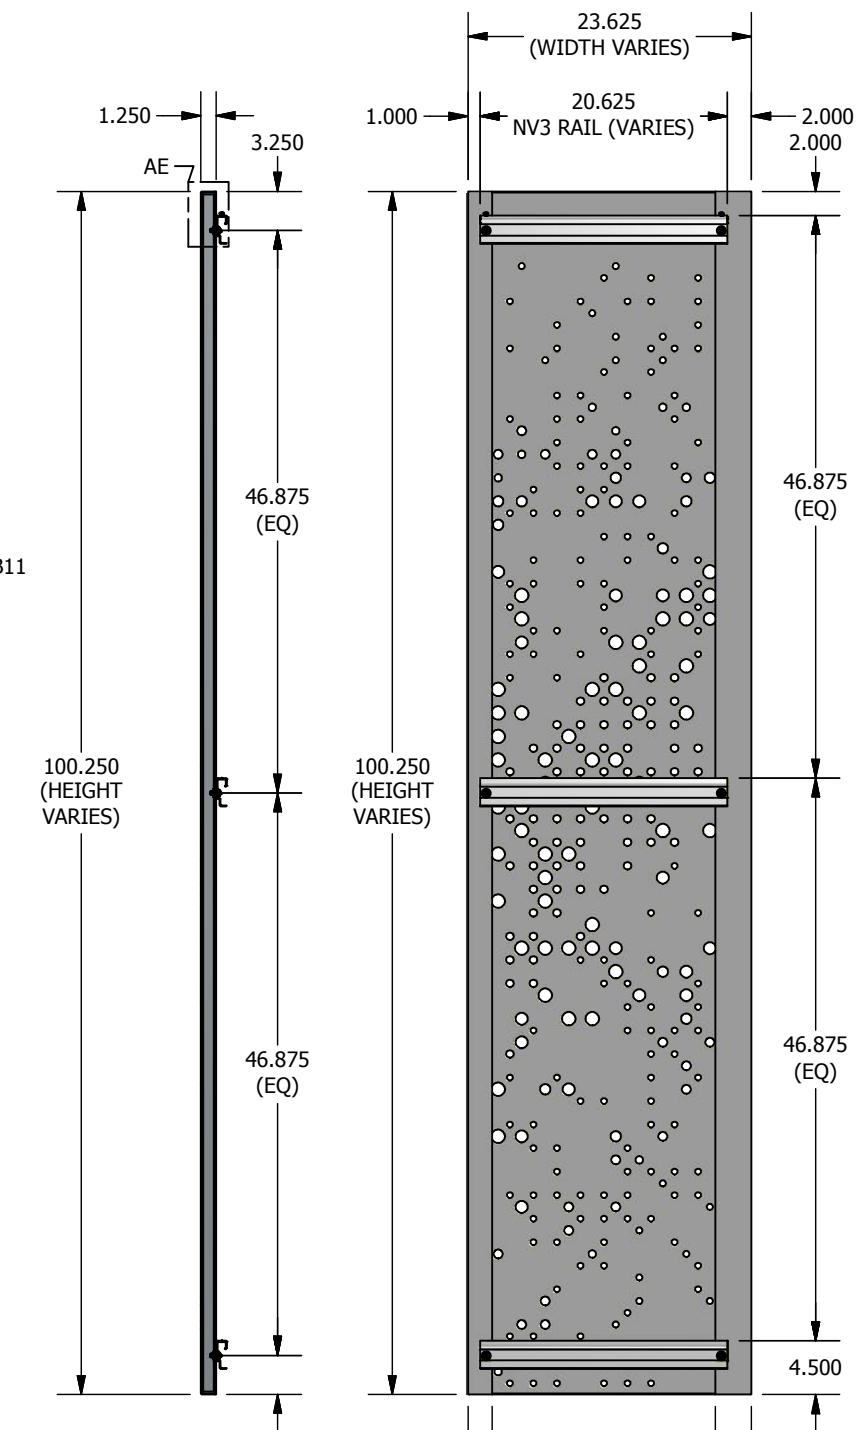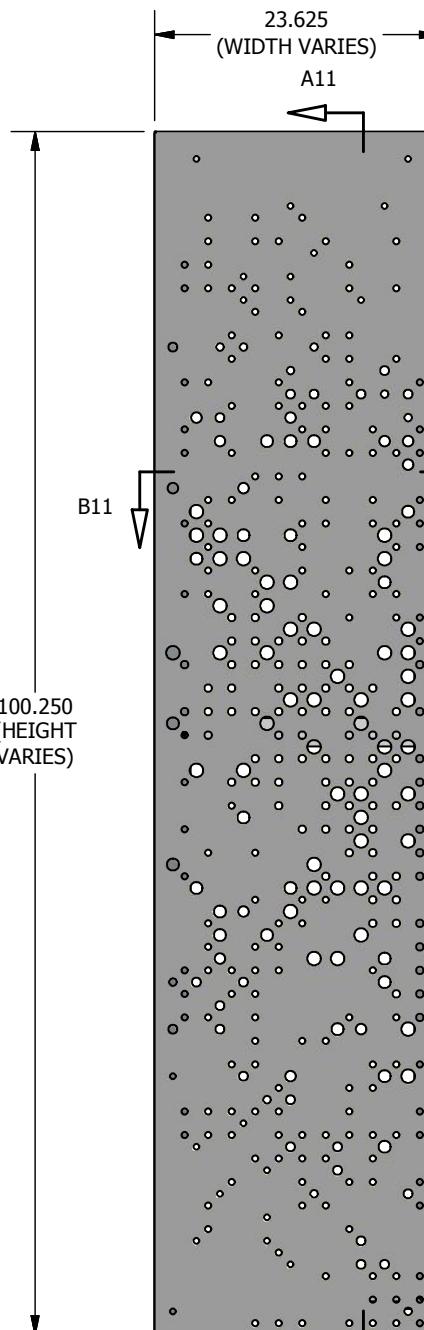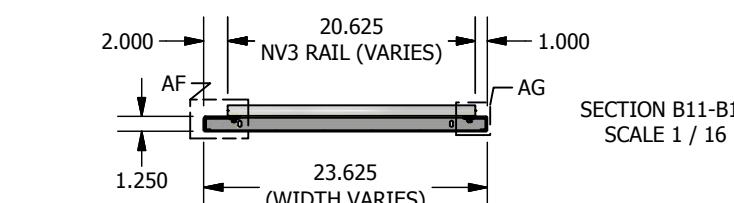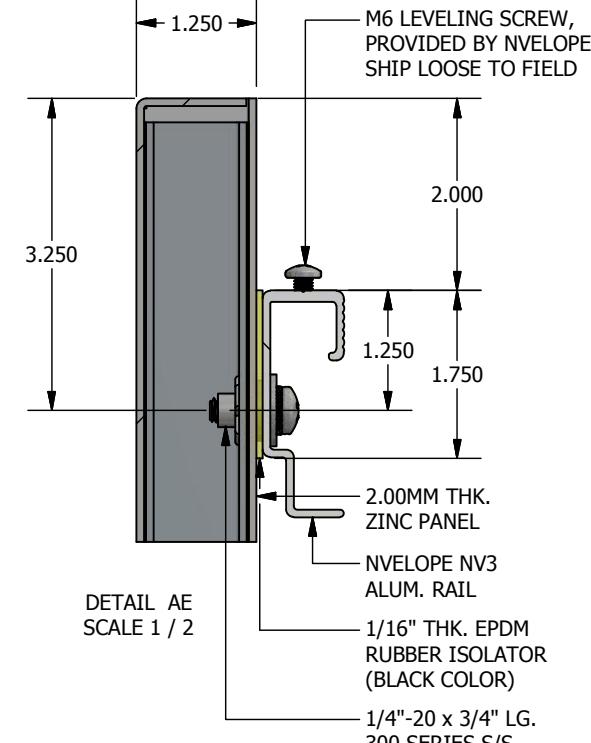

PART TAG:	CORNER LEFT 'VERTICAL' PANELS: PANEL ID PER TABLE		
QT:	(QTY) PER TABLE (SHEET 15)		
MATERIAL:	2.00MM ZINC		
FINISH:	ZINC - NATURAL; ALUM. - BLACK ANOD.		
FLAT FILE:	(AS SHOWN)		
ISSUE DATE	7/28/2016	REVISION	A
SCALE	16 / 37	SHEET NUMBER	



ARCHITECTURAL METAL FABRICATION  
59-20 56TH AVE.  
MASPETH, NY 11378  
(718) 894-1212

**CONTRACTOR**

325 KENT CONSTRUCTION LLC

**ARCHITECT**

ISMAEL LEYVA

**PROJECT #**

DOMINO SITE E

**ITEM**

FAÇADE

**DRAWING**

16001\_ZINC PANEL TYPES

**DRAWN CHECKED**

SP

8

7

6

5

4

3

2

1

## CORNER RIGHT VERTICAL PANEL TABLE

PANEL ID	PANEL TYPE	BEND PROFILE	WIDTH (IN)	HEIGHT (IN)	PANEL TYPE (QTY)
Z01B-1-009	VERTICAL	TYPE 1_CR	11.625	131.25	2
Z01B-3-006	VERTICAL	TYPE 1_CR	11.625	88.5625	1
Z01B-3-016	VERTICAL	TYPE 1_CR	14.625	133.5	1
Z02A-1-004	VERTICAL	TYPE 1_CR	23.625	100.25	1
Z02A-1-007	VERTICAL	TYPE 1_CR	19.625	100.25	1
Z02A-1-009	VERTICAL	TYPE 1_CR	21.125	100.25	1
Z02A-1-010	VERTICAL	TYPE 1_CR	24	100.25	1
Z02A-1-025	VERTICAL	TYPE 1_CR	16.625	131.25	1
Z02A-2-004	VERTICAL	TYPE 1_CR	21.625	100.25	2
Z02A-2-005	VERTICAL	TYPE 1_CR	23.125	100.25	1
Z02A-2-007	VERTICAL	TYPE 1_CR	23.625	100.25	4
Z02A-2-009	VERTICAL	TYPE 1_CR	18.625	100.25	1
Z02A-2-017	VERTICAL	TYPE 1_CR	23.3125	100.25	1
Z02A-2-019	VERTICAL	TYPE 1_CR	15.625	100.25	1
Z02A-2-022	VERTICAL	TYPE 1_CR	21.625	131.25	1
Z02A-2-025	VERTICAL	TYPE 1_CR	26.125	129.75	1
Z02A-2-026	VERTICAL	TYPE 1_CR	23.625	129.75	1
Z02A-2-028	VERTICAL	TYPE 1_CR	23.625	129.75	1
Z02A-3-003	VERTICAL	TYPE 1_CR	19.125	100.25	1
Z02A-3-005	VERTICAL	TYPE 1_CR	23.625	108.125	1
Z02A-3-012	VERTICAL	TYPE 1_CR	23.625	133.5	1
Z02A-4-007	VERTICAL	TYPE 1_CR	23.375	133.75	1
Z02A-4-008	VERTICAL	TYPE 1_CR	15.625	133.75	1
Z02B-1-016	VERTICAL	TYPE 1_CR	25.625	129.75	1
Z02B-2-002	VERTICAL	TYPE 1_CR	23.625	100.25	2
Z02B-4-001	VERTICAL	TYPE 1_CR	23.625	100.25	1
Z02C-1-003	VERTICAL	TYPE 1_CR	23.625	100.25	1
Z02C-1-008	VERTICAL	TYPE 1_CR	17.625	100.25	1
Z02C-2-002	VERTICAL	TYPE 1_CR	23.625	100.25	1
Z02C-2-005	VERTICAL	TYPE 1_CR	23.625	108.125	1
Z02C-3-001	VERTICAL	TYPE 1_CR	23.625	100.25	1
Z02C-4-002	VERTICAL	TYPE 1_CR	23.625	100.25	1
Z03A-2-003	VERTICAL	TYPE 1_CR	32.625	100.25	1
Z03A-2-008	VERTICAL	TYPE 1_CR	28.625	100.25	1
Z03A-2-009	VERTICAL	TYPE 1_CR	31.625	100.25	1
Z03A-2-013	VERTICAL	TYPE 1_CR	31.625	112.25	1
Z03A-3-004	VERTICAL	TYPE 1_CR	35.625	112.25	1
Z03B-1-007	VERTICAL	TYPE 1_CR	35.625	100.25	1
Z03B-2-004	VERTICAL	TYPE 1_CR	35.625	100.25	2
Z03B-2-010	VERTICAL	TYPE 1_CR	33.1875	108.125	1
Z03B-3-004	VERTICAL	TYPE 1_CR	34.375	108.125	1
Z03C-2-002	VERTICAL	TYPE 1_CR	27.625	112.25	1
PANEL TOTAL					49



ARCHITECTURAL METAL FABRICATION  
59-20 56TH AVE.  
MASPETH, NY 11378  
(718) 894-1212

### CONTRACTOR

325 KENT CONSTRUCTION LLC

### ARCHITECT

ISMAEL LEYVA

PROJECT	#
---------	---

DOMINO SITE E

### ITEM

### FAÇADE

### DRAWING

16001\_ZINC PANEL TYPES

DRAWN	CHECKED
-------	---------

SP

ISSUE DATE	REVISION
------------	----------

7/28/2016

A


SCALE	SHEET NUMBER
-------	--------------

FLAT FILE:




(AS SHOWN)	17 / 37
------------	---------

8 7 6 5 4 3 2 1















**CORNER RIGHT VERTICAL PANEL**  
**Z02A-1-004 (SHOWN)**

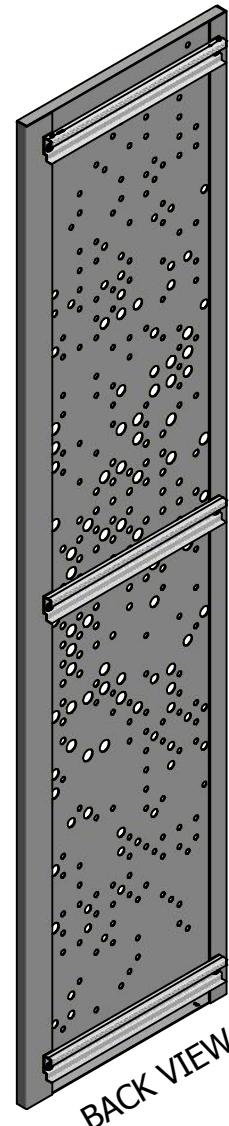

BACK VIEW

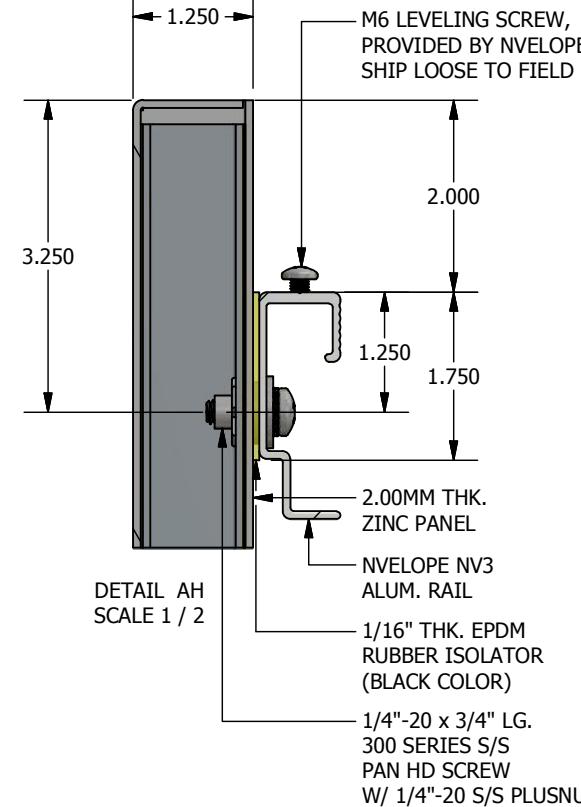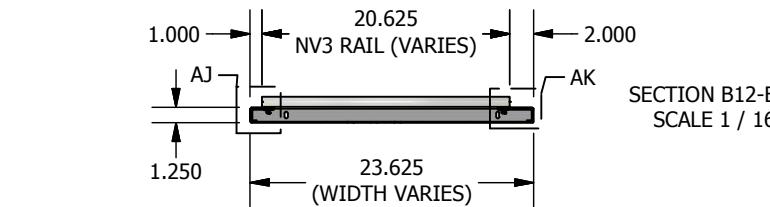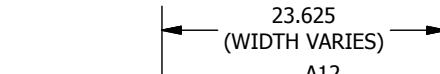DETAIL AH  
SCALE 1 / 2SECTION B12-B12  
SCALE 1 / 16

FRONT VIEW

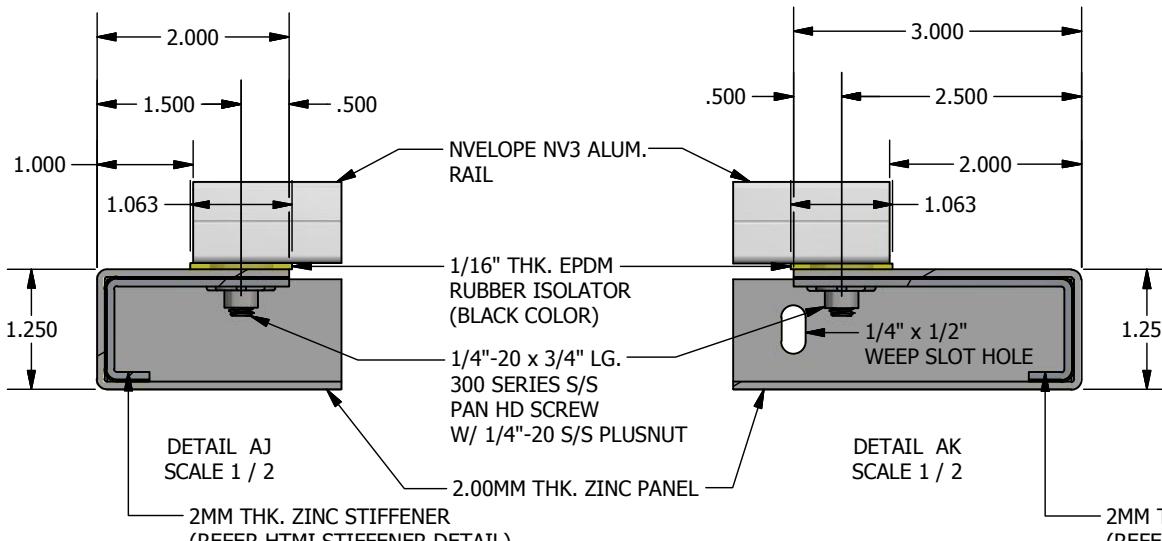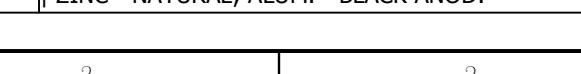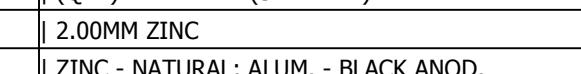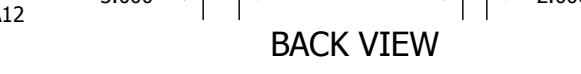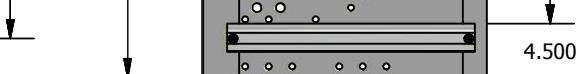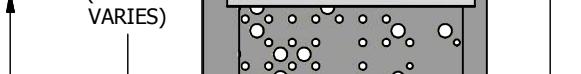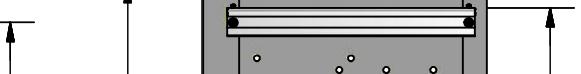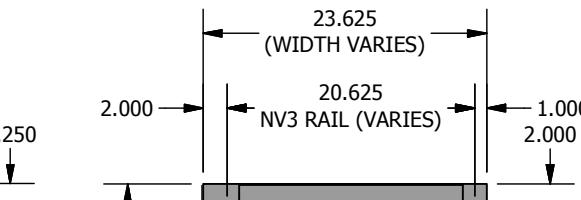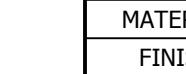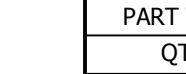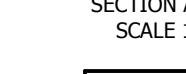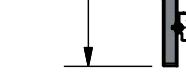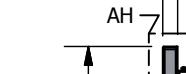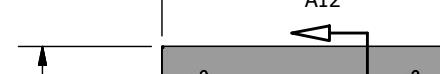DETAIL AK  
SCALE 1 / 2

**HT**  
**TECH**  
ARCHITECTURAL METAL FABRICATION  
59-20 56TH AVE.  
MASPETH, NY 11378  
(718) 894-1212

**CONTRACTOR**  
325 KENT CONSTRUCTION LLC

**ARCHITECT**  
ISMAEL LEYVA

**PROJECT #**  
DOMINO SITE E

**ITEM**  
FAÇADE

**DRAWING**  
16001\_ZINC PANEL TYPES

**DRAWN CHECKED**  
SP

**ISSUE DATE**  
7/28/2016

**REVISION**  
A

**SCALE**  
1

**SHEET NUMBER**  
18 / 37

PART TAG:	CORNER RIGHT 'VERTICAL' PANELS: PANEL ID PER TABLE
QT:	(QTY) PER TABLE (SHEET 17)
MATERIAL:	2.00MM ZINC
FINISH:	ZINC - NATURAL; ALUM. - BLACK ANOD.
FLAT FILE:	(AS SHOWN)

8 7 6 5 4 3 2 1

## BAND PANEL TABLE

PANEL ID	PANEL TYPE	BEND PROFILE	WIDTH (IN)	HEIGHT (IN)	PANEL TYPE (QTY)
Z000-1-011	BAND	TYPE 2	119.625	27.25	59
Z000-1-012	BAND	TYPE 2	119.25	27.25	1021
Z000-1-013	BAND	TYPE 2	56.875	27.25	2
Z000-1-014	BAND	TYPE 2	57.0625	27.25	2
Z000-1-038	BAND	TYPE 2	79.75	27.25	1
Z000-1-040	BAND	TYPE 2	108.25	27.25	1
Z000-1-041	BAND	TYPE 2	103.1875	27.25	1
Z000-1-042	BAND	TYPE 2	27.3125	27.25	1
Z000-1-044	BAND	TYPE 2	63.625	27.25	4
Z000-1-045	BAND	TYPE 2	40.625	27.25	2
Z000-1-046	BAND	TYPE 2	74.6875	27.25	1
Z000-1-047	BAND	TYPE 2	111.75	27.25	1
Z000-1-072	BAND	TYPE 2	29.125	27.25	1
Z000-1-074	BAND	TYPE 2	39.25	27.25	1
Z000-1-075	BAND	TYPE 2	83.125	27.25	1
Z000-1-076	BAND	TYPE 2	48.75	27.25	1
Z000-1-077	BAND	TYPE 2	17.125	27.25	1
Z000-1-078	BAND	TYPE 2	62.1875	27.25	1
Z000-1-079	BAND	TYPE 2	56.3125	27.25	1
Z000-1-081	BAND	TYPE 2	60.125	27.25	1
Z000-1-203	BAND	TYPE 2	111.125	27.25	1
Z000-1-204	BAND	TYPE 2	118.625	27.25	1
Z000-1-206	BAND	TYPE 2	66.125	27.25	1
Z000-1-207	BAND	TYPE 2	60.8125	27.25	1
Z000-1-209	BAND	TYPE 2	68.125	27.25	2
Z000-1-210	BAND	TYPE 2	87.25	27.25	3
Z000-1-211	BAND	TYPE 2	33.625	27.25	2
Z000-1-213	BAND	TYPE 2	113.3125	27.25	1
Z000-1-214	BAND	TYPE 2	68.1875	27.25	1
Z000-1-215	BAND	TYPE 2	115.625	27.25	10
Z000-1-232	BAND	TYPE 2	12.625	27.25	1
Z000-1-234	BAND	TYPE 2	62.125	27.25	1
Z000-1-237	BAND	TYPE 2	111.625	27.25	1
Z000-1-239	BAND	TYPE 2	121.25	27.25	1
Z000-1-240	BAND	TYPE 2	117.25	27.25	1
Z000-1-341	BAND	TYPE 2	57.625	27.25	7
Z000-1-343	BAND	TYPE 2	32.3125	27.25	1
Z000-1-344	BAND	TYPE 2	26.125	27.25	1
Z000-1-345	BAND	TYPE 2	44.3125	27.25	1
Z000-1-347	BAND	TYPE 2	102.125	27.25	2
Z000-1-348	BAND	TYPE 2	27.125	27.25	2
Z000-1-350	BAND	TYPE 2	40.3125	27.25	1
Z000-1-351	BAND	TYPE 2	33.0625	27.25	1
Z000-1-352	BAND	TYPE 2	45.125	27.25	1
Z000-1-360	BAND	TYPE 2	11.125	27.25	1

## BALCONY BAND PANEL TABLE

PANEL ID	PANEL TYPE	BEND PROFILE	WIDTH (IN)	HEIGHT (IN)	PANEL TYPE (QTY)
Z000-1-001	BALCONY BAND	TYPE 2	59.75	27.25	15
Z000-1-002	BALCONY BAND	TYPE 2	61	27.25	30
Z000-1-003	BALCONY BAND	TYPE 2	61.25	27.25	42
Z000-1-082	BALCONY BAND	TYPE 2	60.25	27.25	8
PANEL TOTAL					95

\*BALCONY BAND PANELS HOLD FOR FURTHER COORDINATION

PANEL ID	PANEL TYPE	BEND PROFILE	WIDTH (IN)	HEIGHT (IN)	PANEL TYPE (QTY)
Z000-1-361	BAND	TYPE 2	70.25	27.25	1
Z000-1-362	BAND	TYPE 2	72.75	27.25	1
Z000-1-402	BAND	TYPE 2	30.125	27.25	1
Z000-1-403	BAND	TYPE 2	73.9375	27.25	1
Z000-1-404	BAND	TYPE 2	85.125	27.25	1
Z000-1-407	BAND	TYPE 2	38	27.25	1
Z000-1-408	BAND	TYPE 2	8.875	27.25	1
Z000-1-409	BAND	TYPE 2	35.5	27.25	1
Z000-1-442	BAND	TYPE 2	119.25	23.375	10
Z000-1-443	BAND	TYPE 2	119.75	23.375	2
Z000-1-444	BAND	TYPE 2	49.625	27.25	1
Z000-1-445	BAND	TYPE 2	70.75	27.25	1
Z000-1-480	BAND	TYPE 2	48.8125	27.25	1
Z000-1-481	BAND	TYPE 2	49.6875	27.25	1
Z000-1-482	BAND	TYPE 2	65.75	27.25	1
Z000-1-484	BAND	TYPE 2	59.625	27.25	1
Z000-1-485	BAND	TYPE 2	118.125	27.25	1
Z000-1-486	BAND	TYPE 2	86.75	27.25	1
Z000-1-487	BAND	TYPE 2	55.3125	27.25	1
Z000-1-510	BAND	TYPE 2	61.125	27.25	1
Z000-1-511	BAND	TYPE 2	51.75	27.25	1
Z000-1-512	BAND	TYPE 2	118.75	27.25	2
Z000-1-513	BAND	TYPE 2	113.625	27.25	1
Z000-1-561	BAND	TYPE 2	119.25	38.25	51
Z000-1-562	BAND	TYPE 2	119.625	38.25	3
Z000-1-563	BAND	TYPE 2	44.125	38.25	2
Z000-1-564	BAND	TYPE 2	70.75	38.25	1
Z000-1-565	BAND	TYPE 2	37.625	38.25	2
Z000-1-567	BAND	TYPE 2	86.125	38.25	2
Z000-1-568	BAND	TYPE 2	57.625	38.25	1
Z000-1-569	BAND	TYPE 2	57.25	38.25	1
Z000-1-571	BAND	TYPE 2	71	38.25	1
Z000-1-596	BAND	TYPE 2	119.75	27.25	1
Z000-1-597	BAND	TYPE 2	23.5625	27.25	1
Z000-1-599	BAND	TYPE 2	11.5625	27.25	1
Z000-1-600	BAND	TYPE 2	21.125	27.25	1
Z000-1-602	BAND	TYPE 2	35.625	27.25	1
Z000-1-604	BAND	TYPE 2	103.125	27.25	1
Z000-1-606	BAND	TYPE 2	22.25	27.25	2
Z000-1-607	BAND	TYPE 2	101.25	27.25	2
Z000-1-609	BAND	TYPE 2	22.625	27.25	6
Z000-1-613	BAND	TYPE 2	119.25	27.25	1
PANEL TOTAL					1265







## BAND PANEL (WITH CUTOUT) TABLE NOTE: CANNOT RELEASE DUE TO CUTOUTS

PANEL ID	PANEL TYPE	BEND PROFILE	WIDTH (IN)	HEIGHT (IN)	PANEL TYPE (QTY)
Z000-1-012	BAND	TYPE 2_CO	119.25	27.25	78
Z000-1-037	BAND	TYPE 2_CO	38.75	27.25	1
Z000-1-039	BAND	TYPE 2_CO	130.25	27.25	1
Z000-1-239	BAND	TYPE 2_CO	121.25	27.25	2
Z000-1-240	BAND	TYPE 2_CO	117.25	27.25	2
PANEL TOTAL					84

\*PANELS NEED NOTCHES (BALCONY BAND), HOLD FOR FURTHER COORDINATION

PART TAG:	
QT:	
MATERIAL:	
FINISH:	
FLAT FILE:	
ISSUE DATE	REVISION
7/28	

**BAND/BALCONY BAND PANEL**  
**Z000-1-012 (SHOWN)**

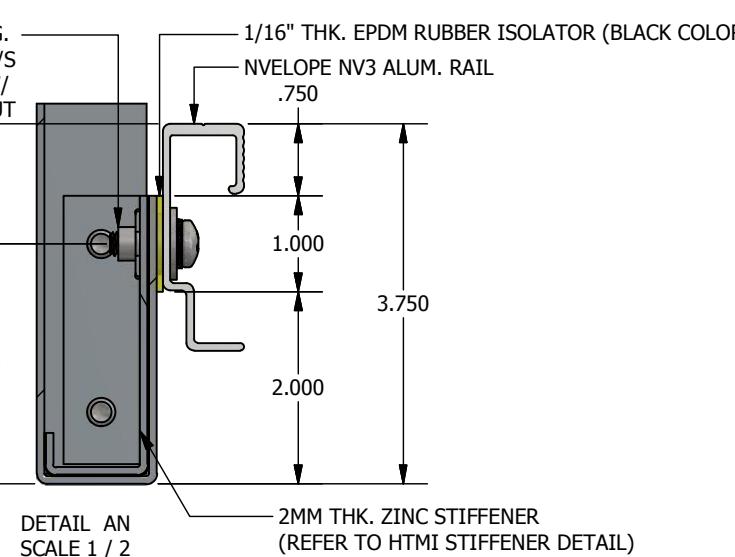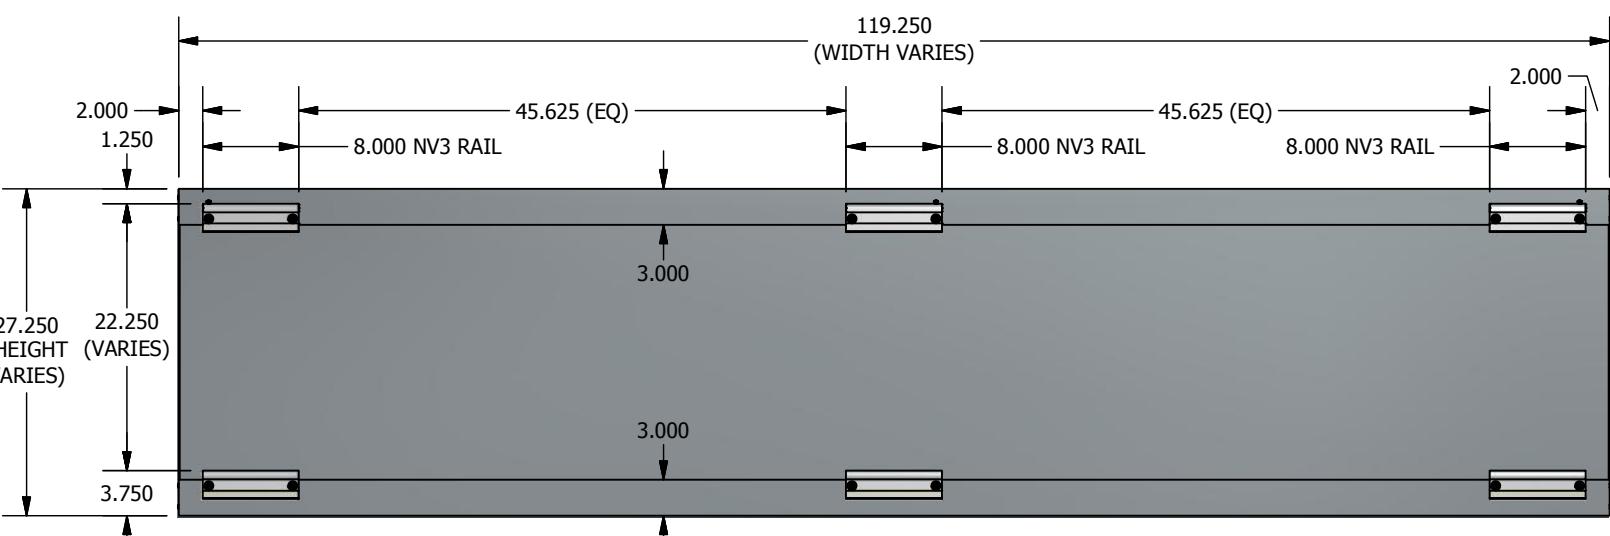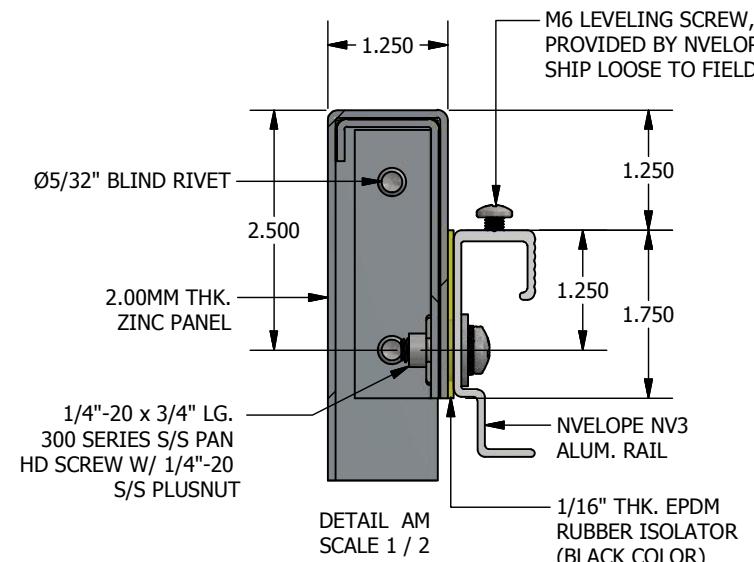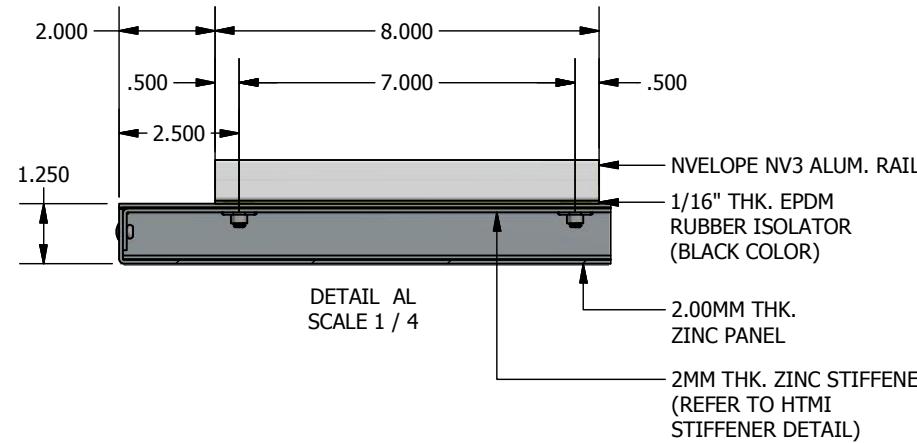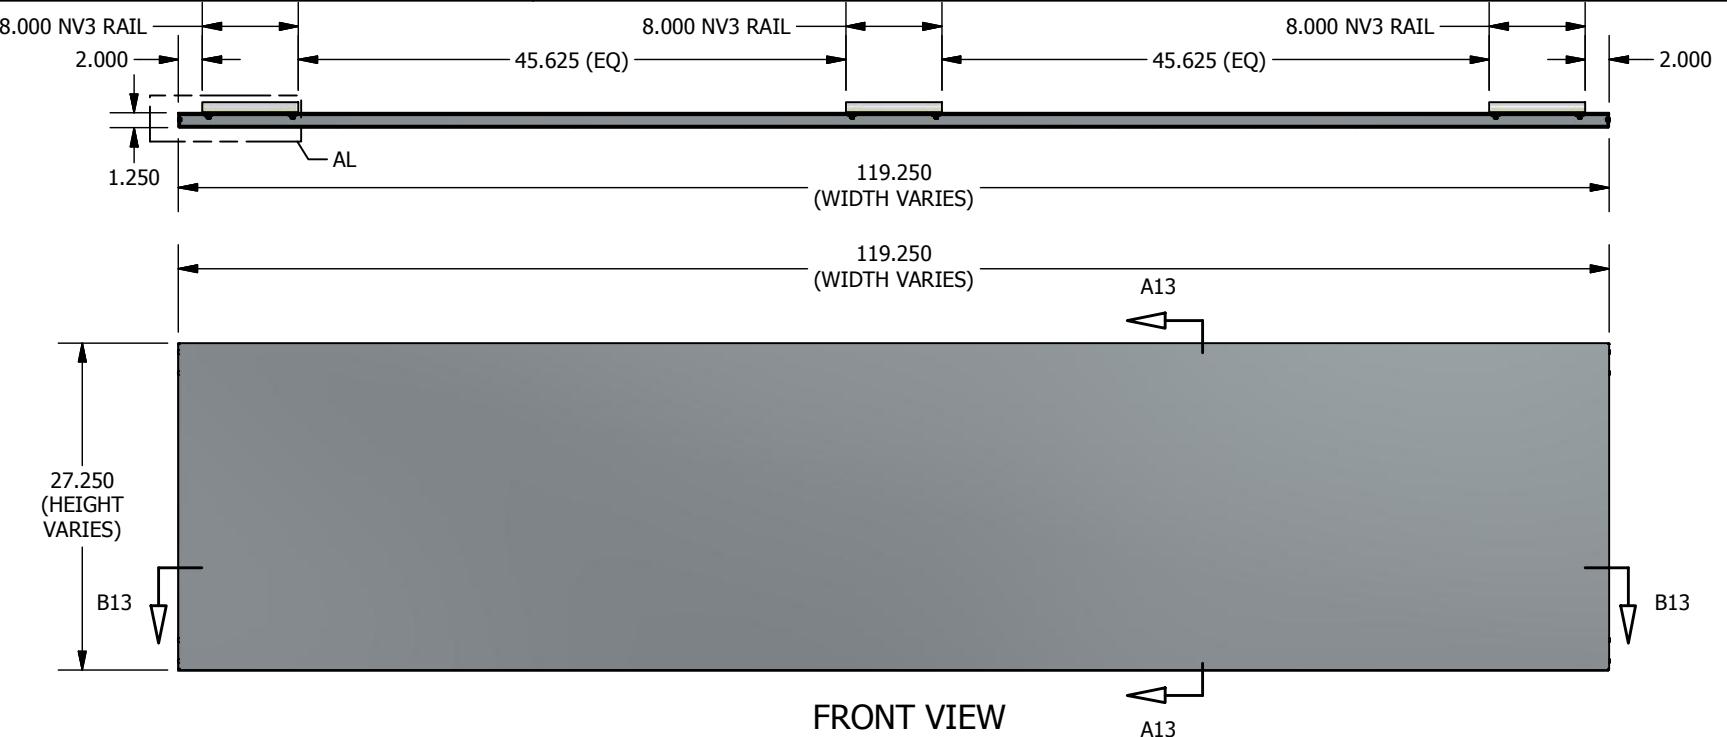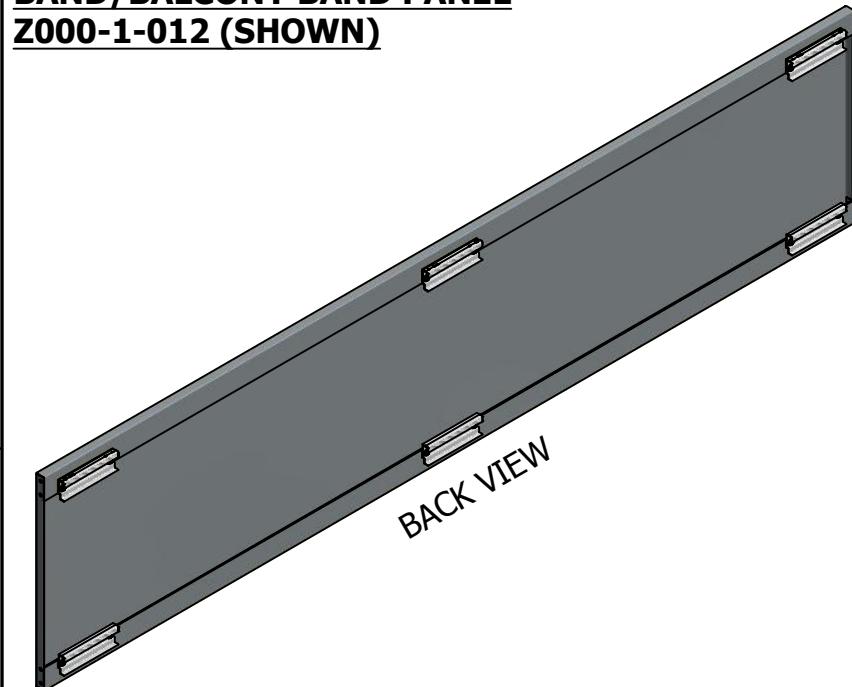

PART TAG:	'BAND/BALCONY BAND' PANELS: PANEL ID PER TABLE	ISSUE DATE	REVISION
QT:	(QTY) PER TABLE (SHEET 19)	7/28/2016	A
MATERIAL:	2.00MM ZINC	SCALE	SHEET NUMBER
FINISH:	ZINC - NATURAL; ALUM. - BLACK ANOD.	(AS SHOWN)	20 / 37
FLAT FILE:			



ARCHITECTURAL METAL FABRICATION  
59-20 56TH AVE.  
MASPETH, NY 11378  
(718) 894-1212

**CONTRACTOR**

325 KENT CONSTRUCTION LLC

**ARCHITECT**

ISMAEL LEYVA

**PROJECT #**  
DOMINO SITE E

**ITEM**

FAÇADE

**DRAWING**

16001\_ZINC PANEL TYPES

**DRAWN CHECKED**

SP

E

ISSUE DATE

7/28/2016

A

REVISION

A

SCALE

SHEET NUMBER

20 / 37

## LEFT CORNER BAND PANEL TABLE

PANEL ID	PANEL TYPE	BEND PROFILE	WIDTH (IN)	HEIGHT (IN)	PANEL TYPE (QTY)
Z000-1-011	BAND	TYPE 2_CL	119.625	27.25	30
Z000-1-036	BAND	TYPE 2_CL	119.125	27.25	11
Z000-1-043	BAND	TYPE 2_CL	47.625	27.25	1
Z000-1-073	BAND	TYPE 2_CL	79.125	27.25	1
Z000-1-081	BAND	TYPE 2_CL	60.125	27.25	1
Z000-1-205	BAND	TYPE 2_CL	99.125	27.25	1
Z000-1-212	BAND	TYPE 2_CL	44.9375	27.25	1
Z000-1-233	BAND	TYPE 2_CL	67.625	27.25	1
Z000-1-236	BAND	TYPE 2_CL	23.125	27.25	1
Z000-1-340	BAND	TYPE 2_CL	83.625	27.25	1
Z000-1-342	BAND	TYPE 2_CL	81.625	27.25	1
Z000-1-344	BAND	TYPE 2_CL	26.125	27.25	1
Z000-1-349	BAND	TYPE 2_CL	37.8125	27.25	1
Z000-1-359	BAND	TYPE 2_CL	48.125	27.25	1
Z000-1-401	BAND	TYPE 2_CL	12.75	27.25	1
Z000-1-406	BAND	TYPE 2_CL	28.9375	27.25	1
Z000-1-479	BAND	TYPE 2_CL	22.3125	27.25	1
Z000-1-484	BAND	TYPE 2_CL	59.625	27.25	1
Z000-1-560	BAND	TYPE 2_CL	119.125	38.25	1
Z000-1-562	BAND	TYPE 2_CL	119.625	38.25	2
Z000-1-566	BAND	TYPE 2_CL	83.625	38.25	1
Z000-1-570	BAND	TYPE 2_CL	83.375	38.25	1
Z000-1-608	BAND	TYPE 2_CL	101.625	27.25	3
PANEL TOTAL					65



ARCHITECTURAL METAL FABRICATION  
59-20 56TH AVE.  
MASPETH, NY 11378  
(718) 894-1212

### CONTRACTOR

325 KENT CONSTRUCTION LLC

### ARCHITECT

ISMAEL LEYVA

PROJECT	#
---------	---

DOMINO SITE E

### ITEM

FAÇADE

### DRAWING

16001\_ZINC PANEL TYPES

DRAWN	CHECKED
-------	---------

SP

ISSUE DATE	REVISION
------------	----------


7/28/2016	A
-----------	---

SCALE	SHEET NUMBER
-------	--------------


(AS SHOWN)	21 / 37
------------	---------

PART TAG:	
QT:	
MATERIAL:	
FINISH:	
FLAT FILE:	


**LEFT CORNER BAND PANEL  
Z000-1-011 (SHOWN)**

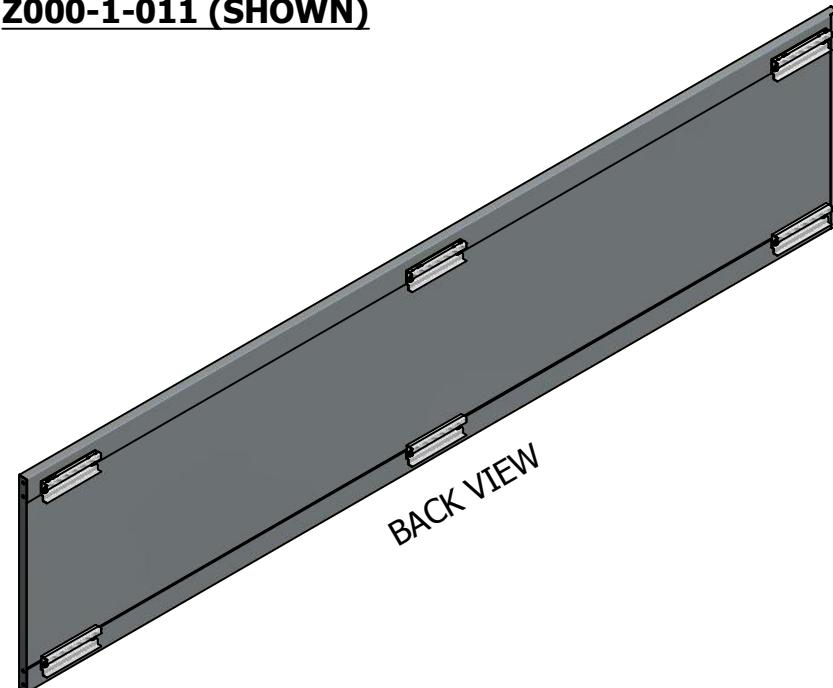

BACK VIEW

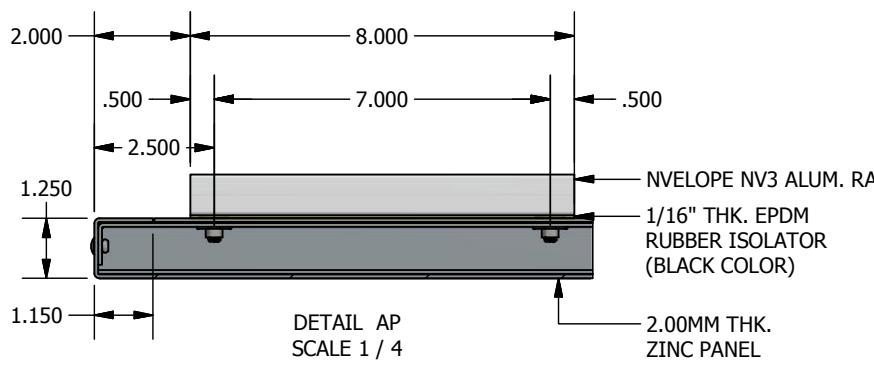


DETAIL AP  
SCALE 1 / 4

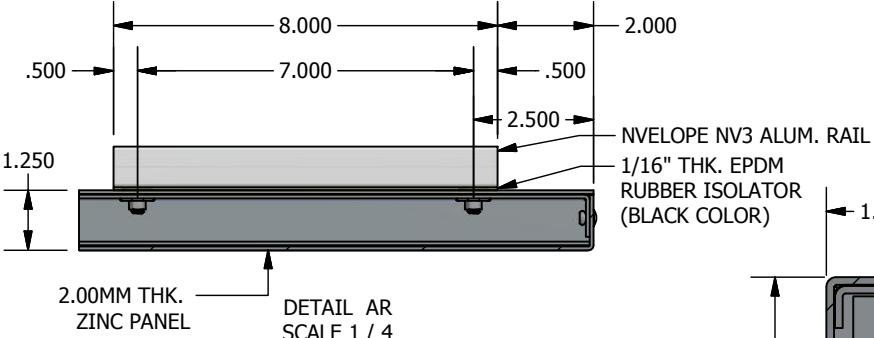


DETAIL AR  
SCALE 1 / 4

2MM THK. Z  
(REFER TO HTMI STI)

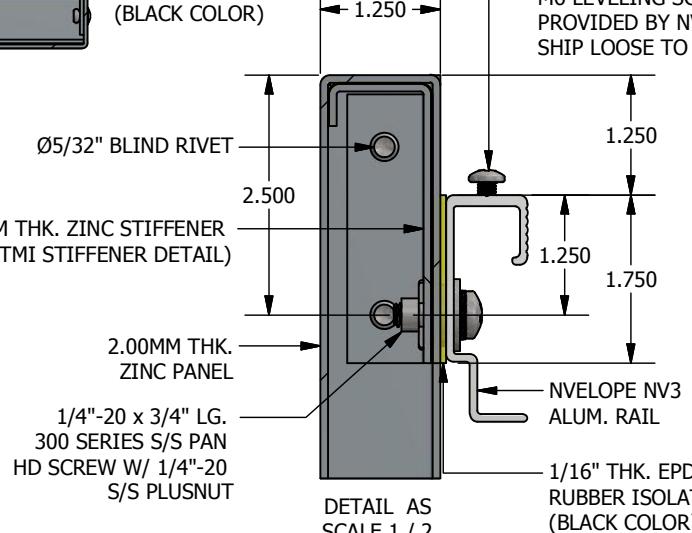


DETA  
SCAL

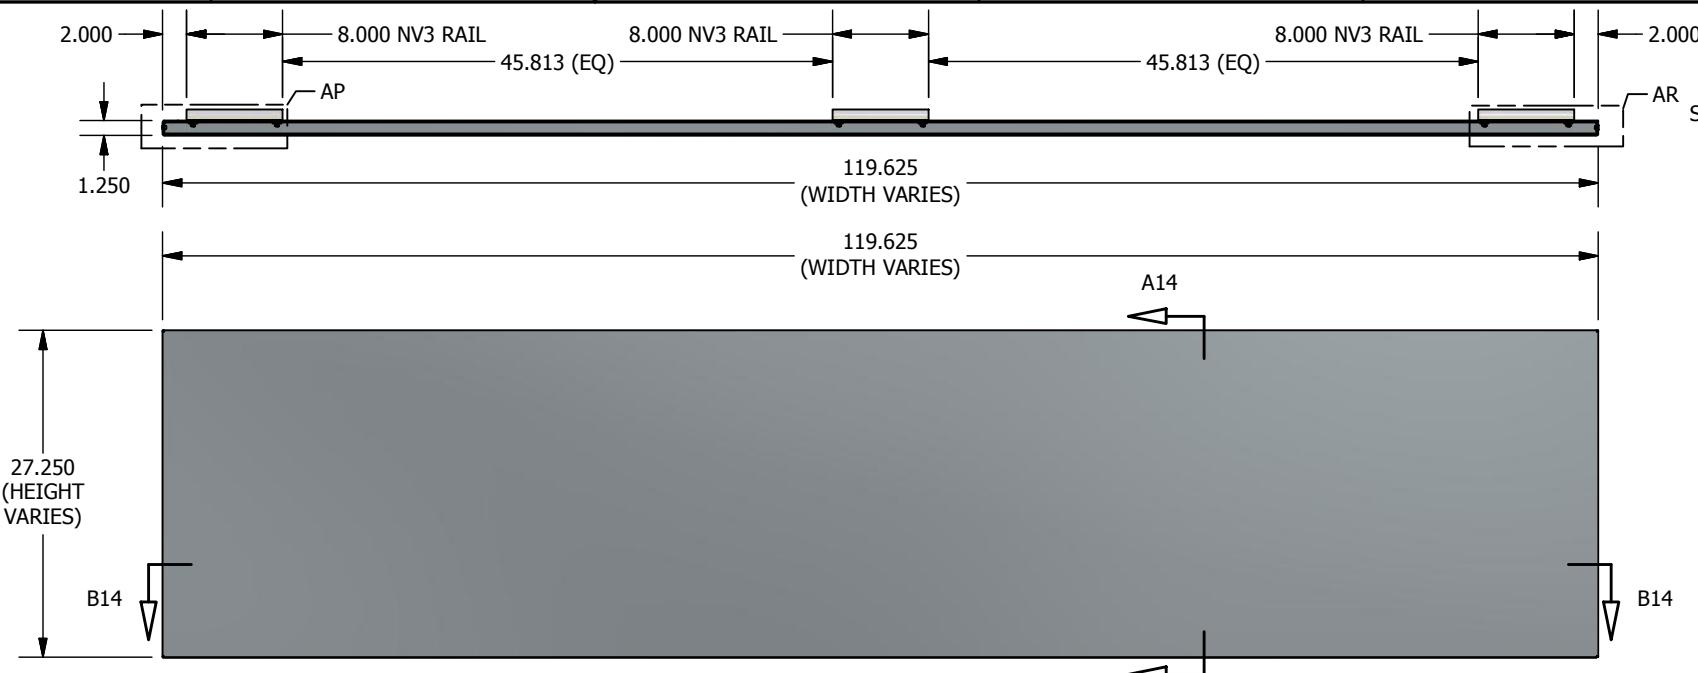


FRONT VIEW

A14

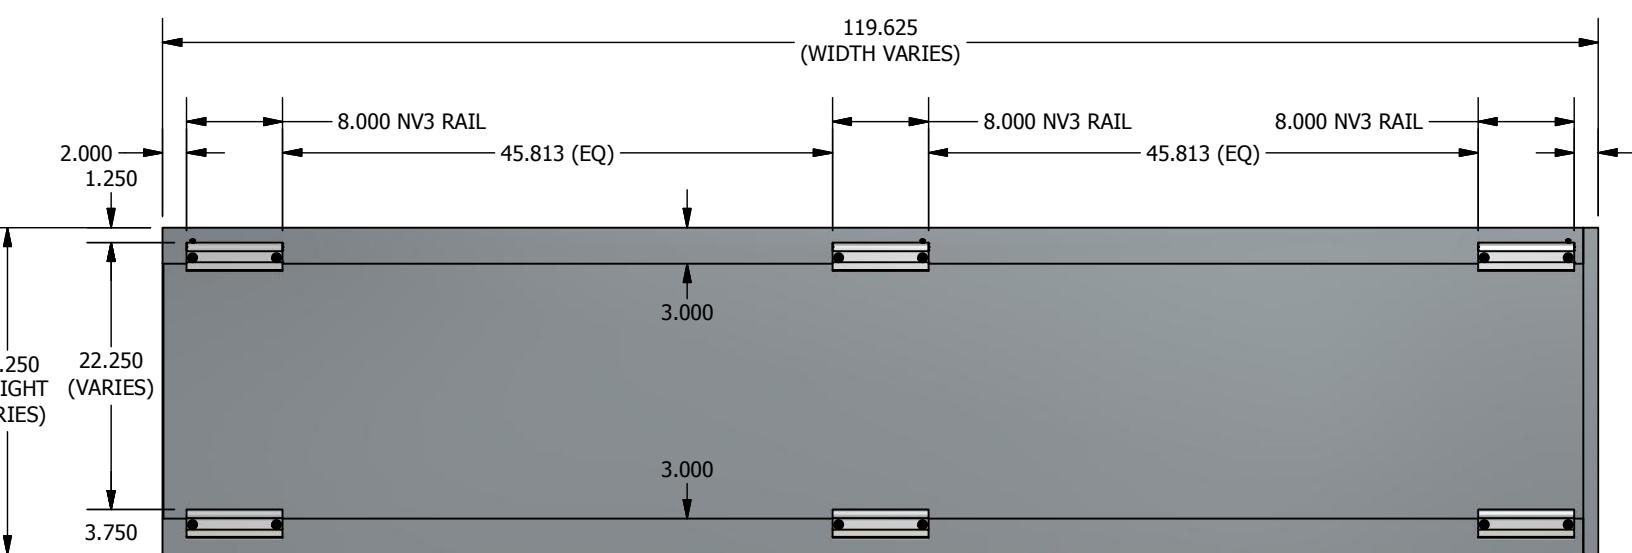

**BACK VIEW**

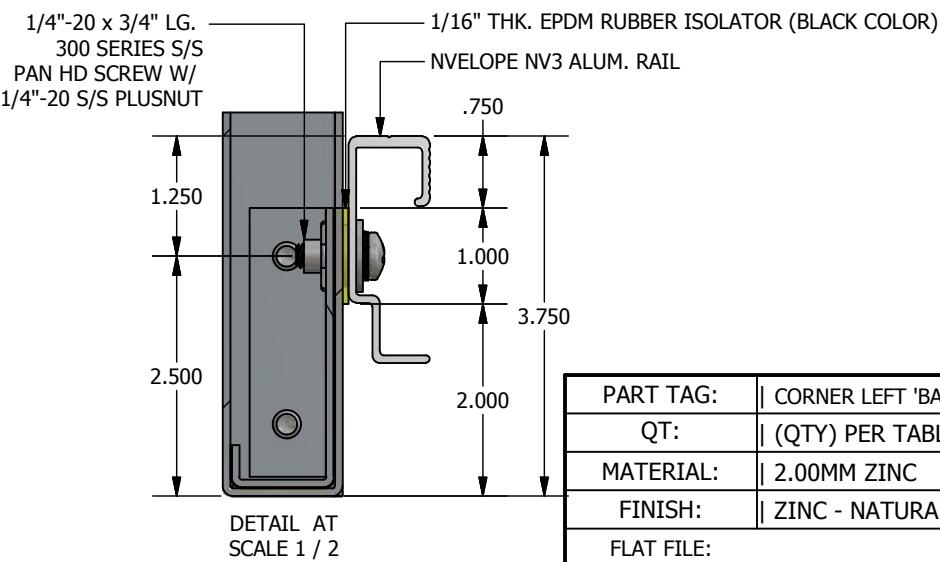

DETAIL  
SCALE 1

PART TAG:	CORNER LEFT 'BAND' PANELS: PANEL ID PER TABLE
QT:	(QTY) PER TABLE (SHEET 21)
MATERIAL:	2.00MM ZINC
FINISH:	ZINC - NATURAL; ALUM. - BLACK ANOD.
FLAT FILE:	



ARCHITECTURAL METAL FABRICATION  
59-20 56TH AVE.  
MASPETH, NY 11378  
(718) 804-1212

CONTRACTOR

325 KENT CONSTRUCTION LLC

---

ARCHITECT

**ECT** | #

---

**ITEM**

---

DRAWING

16001\_ZINC PANEL TYPES

1

**ISSUE DATE**      **REV.**

2016

**SCALE**

22

## RIGHT CORNER BAND PANEL TABLE

PANEL ID	PANEL TYPE	BEND PROFILE	WIDTH (IN)	HEIGHT (IN)	PANEL TYPE (QTY)
Z000-1-011	BAND	TYPE 2_CR	119.625	27.25	27
Z000-1-036	BAND	TYPE 2_CR	119.125	27.25	7
Z000-1-043	BAND	TYPE 2_CR	47.625	27.25	2
Z000-1-080	BAND	TYPE 2_CR	69.625	27.25	1
Z000-1-208	BAND	TYPE 2_CR	42.5	27.25	1
Z000-1-235	BAND	TYPE 2_CR	51.125	27.25	1
Z000-1-238	BAND	TYPE 2_CR	95.625	27.25	1
Z000-1-340	BAND	TYPE 2_CR	83.625	27.25	1
Z000-1-342	BAND	TYPE 2_CR	81.625	27.25	1
Z000-1-346	BAND	TYPE 2_CR	33.5625	27.25	1
Z000-1-353	BAND	TYPE 2_CR	41.125	27.25	1
Z000-1-405	BAND	TYPE 2_CR	29.9375	27.25	1
Z000-1-410	BAND	TYPE 2_CR	49.125	27.25	1
Z000-1-483	BAND	TYPE 2_CR	39.625	27.25	1
Z000-1-488	BAND	TYPE 2_CR	22.4375	27.25	1
Z000-1-562	BAND	TYPE 2_CR	119.625	38.25	3
Z000-1-566	BAND	TYPE 2_CR	83.625	38.25	2
Z000-1-598	BAND	TYPE 2_CR	89.625	27.25	1
Z000-1-601	BAND	TYPE 2_CR	12.625	27.25	1
Z000-1-603	BAND	TYPE 2_CR	76.625	27.25	1
Z000-1-608	BAND	TYPE 2_CR	101.625	27.25	3
PANEL TOTAL					59



ARCHITECTURAL METAL FABRICATION  
59-20 56TH AVE.  
MASPETH, NY 11378  
(718) 894-1212

### CONTRACTOR

325 KENT CONSTRUCTION LLC

### ARCHITECT

ISMAEL LEYVA

PROJECT	#
---------	---

DOMINO SITE E

### ITEM

FAÇADE

### DRAWING

16001\_ZINC PANEL TYPES

DRAWN	CHECKED
-------	---------

SP

ISSUE DATE	REVISION
------------	----------

7/28/2016	A
-----------	---

SCALE	SHEET NUMBER
-------	--------------


(AS SHOWN)	23 / 37
------------	---------

PART TAG:	
QT:	
MATERIAL:	
FINISH:	
FLAT FILE:	








PANEL ID	PANEL TYPE	BEND PROFILE	WIDTH (IN)	HEIGHT (IN)	PANEL TYPE (QTY)
Z09A-1-000	PTAC/SILL	TYPE 3	41.25	32.5	19
Z09A-1-001	PTAC/SILL	TYPE 3	41.25	24	204
Z09A-2-000	PTAC/SILL	TYPE 3	41.25	32.5	21
Z09A-2-001	PTAC/SILL	TYPE 3	41.25	24	200
Z10A-1-000	PTAC/SILL	TYPE 3	53.25	24	194
Z10A-2-000	PTAC/SILL	TYPE 3	53.25	24	177
PANEL TOTAL					815

**Z10A-1-000 (SHOWN)**

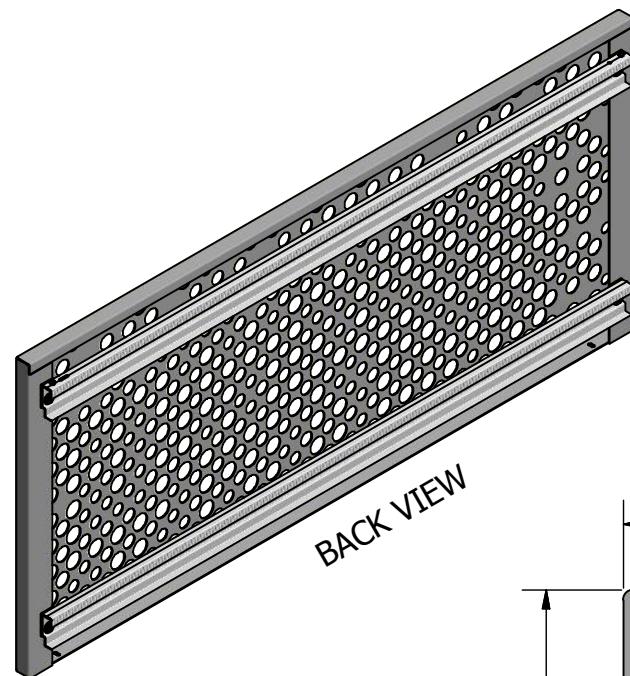


BACK VIEW

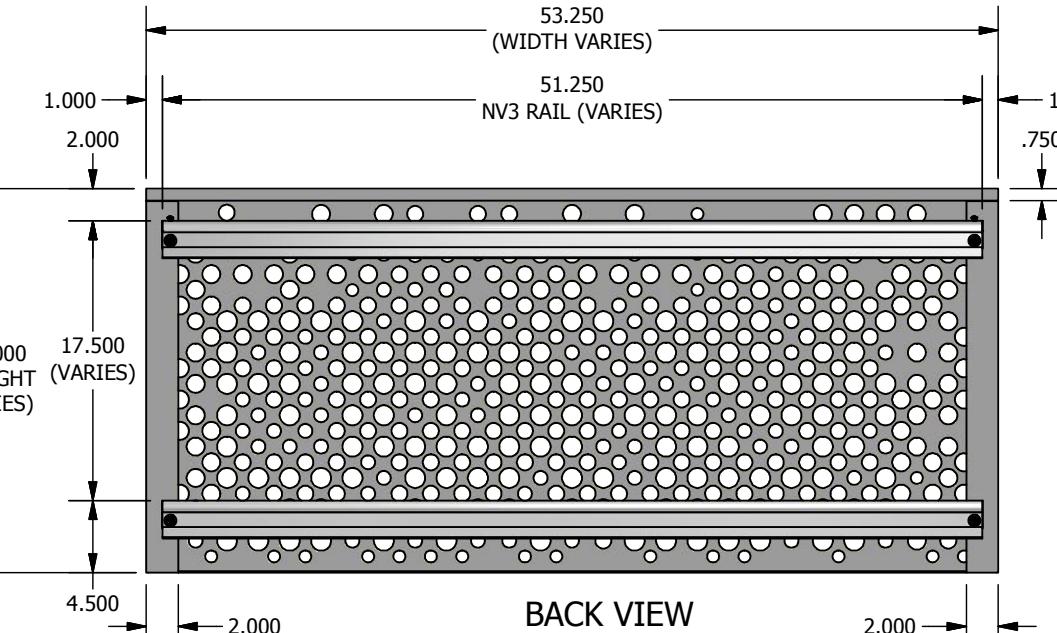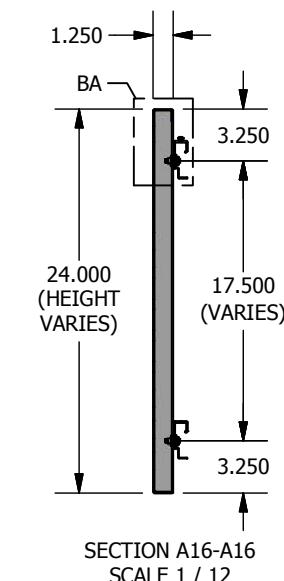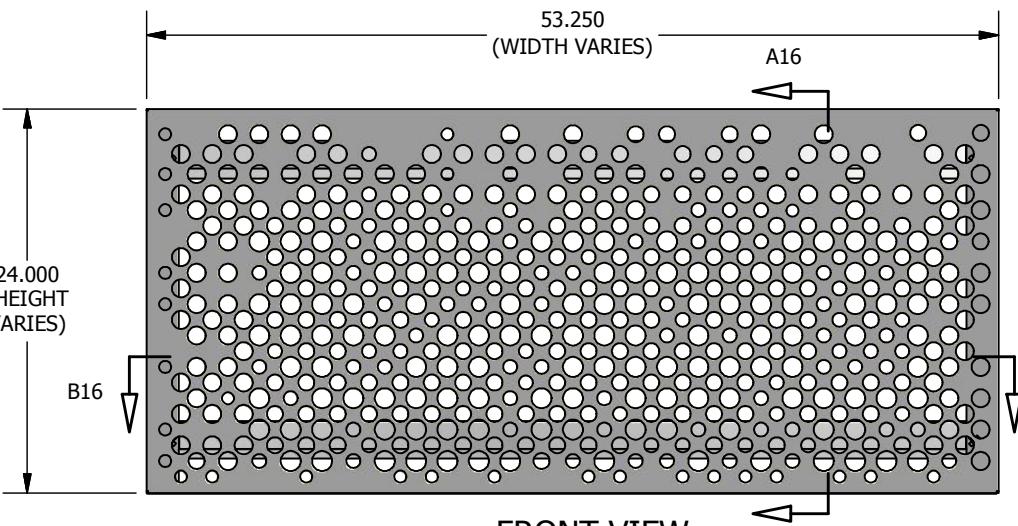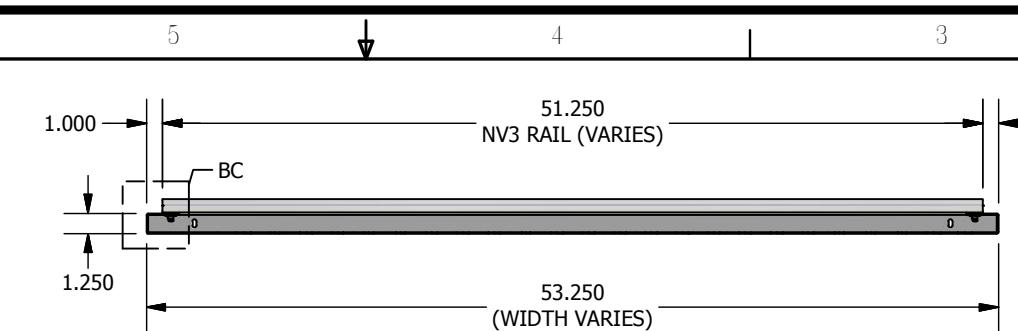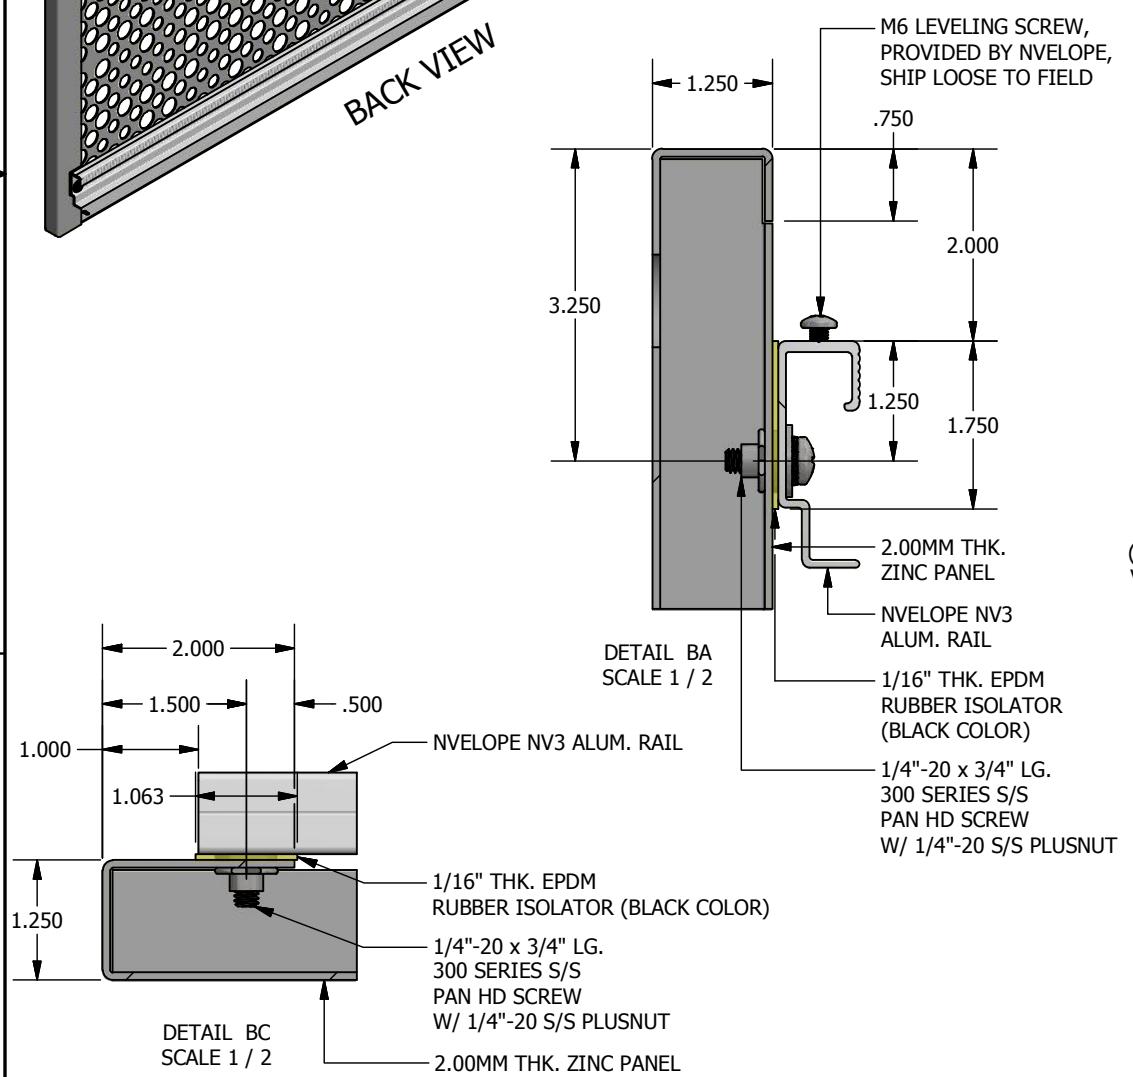


PART TAG:	'PTAC' PANELS: PANEL ID PER TABLE	ISSUE DATE	REVISION
QT:	(QTY) PER TABLE	7/28/2016	A
MATERIAL:	2.00MM ZINC	SCALE	SHEET NUMBER
FINISH:	ZINC - NATURAL; ALUM. - BLACK ANOD.	(AS SHOWN)	25 / 37
FLAT FILE:			

PANEL ID	PANEL TYPE	BEND PROFILE	WIDTH (IN)	HEIGHT (IN)	PANEL TYPE (QTY)
Z02D-1-000	PTAC/SILL	TYPE 3	23.25	24	19
PANEL TOTAL					19

**Z02D-1-000 (SHOWN)**

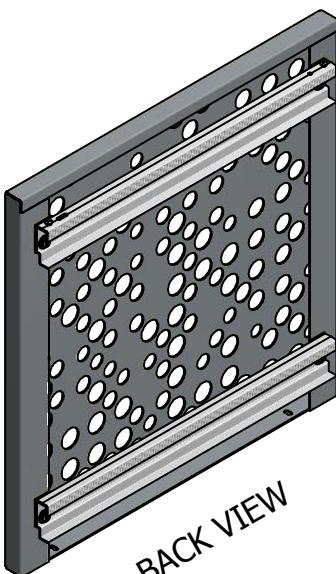


BACK VIEW

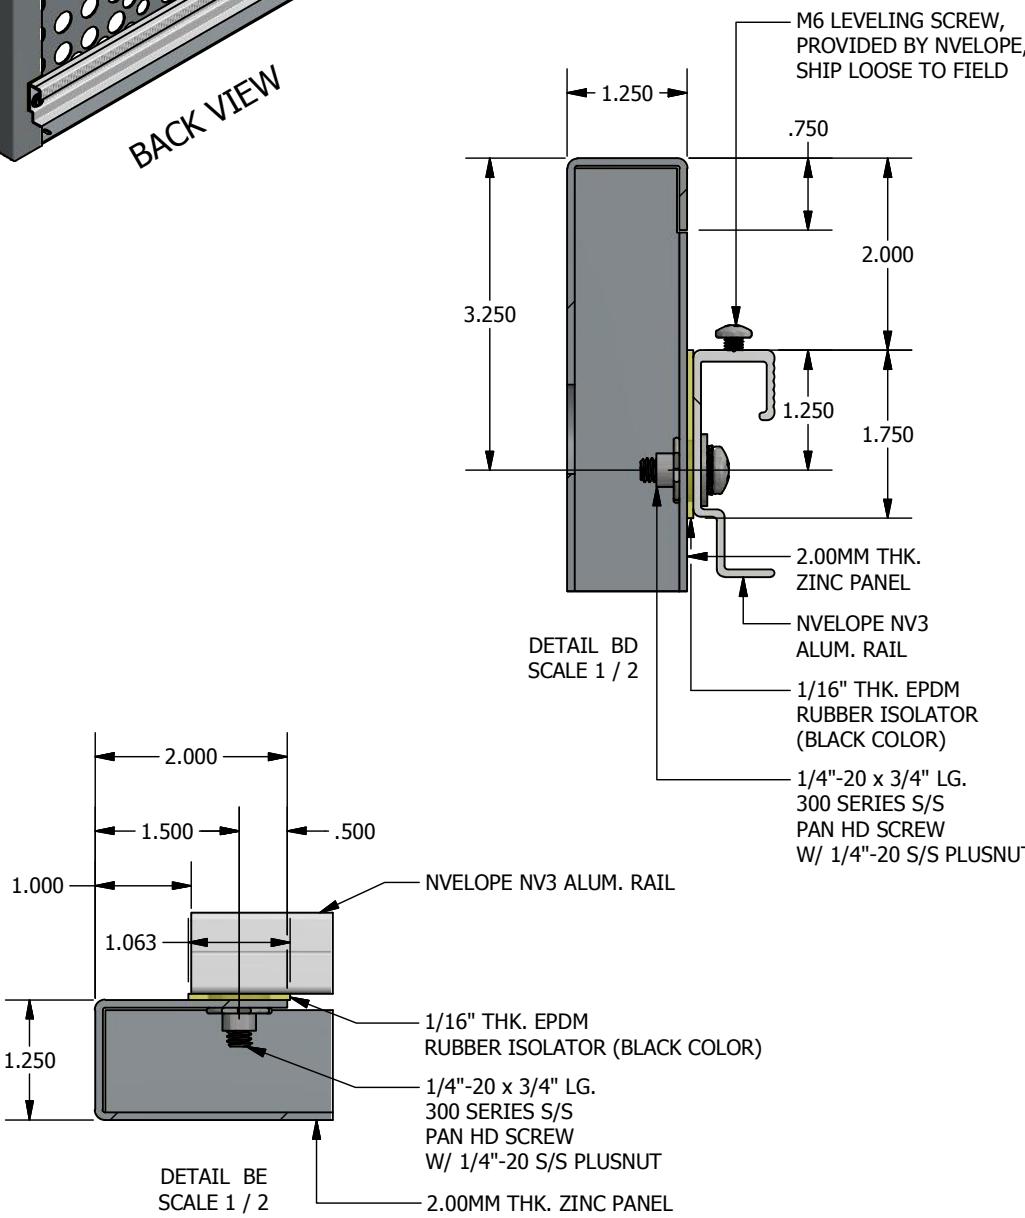

DETAIL  
SCALE 1

1

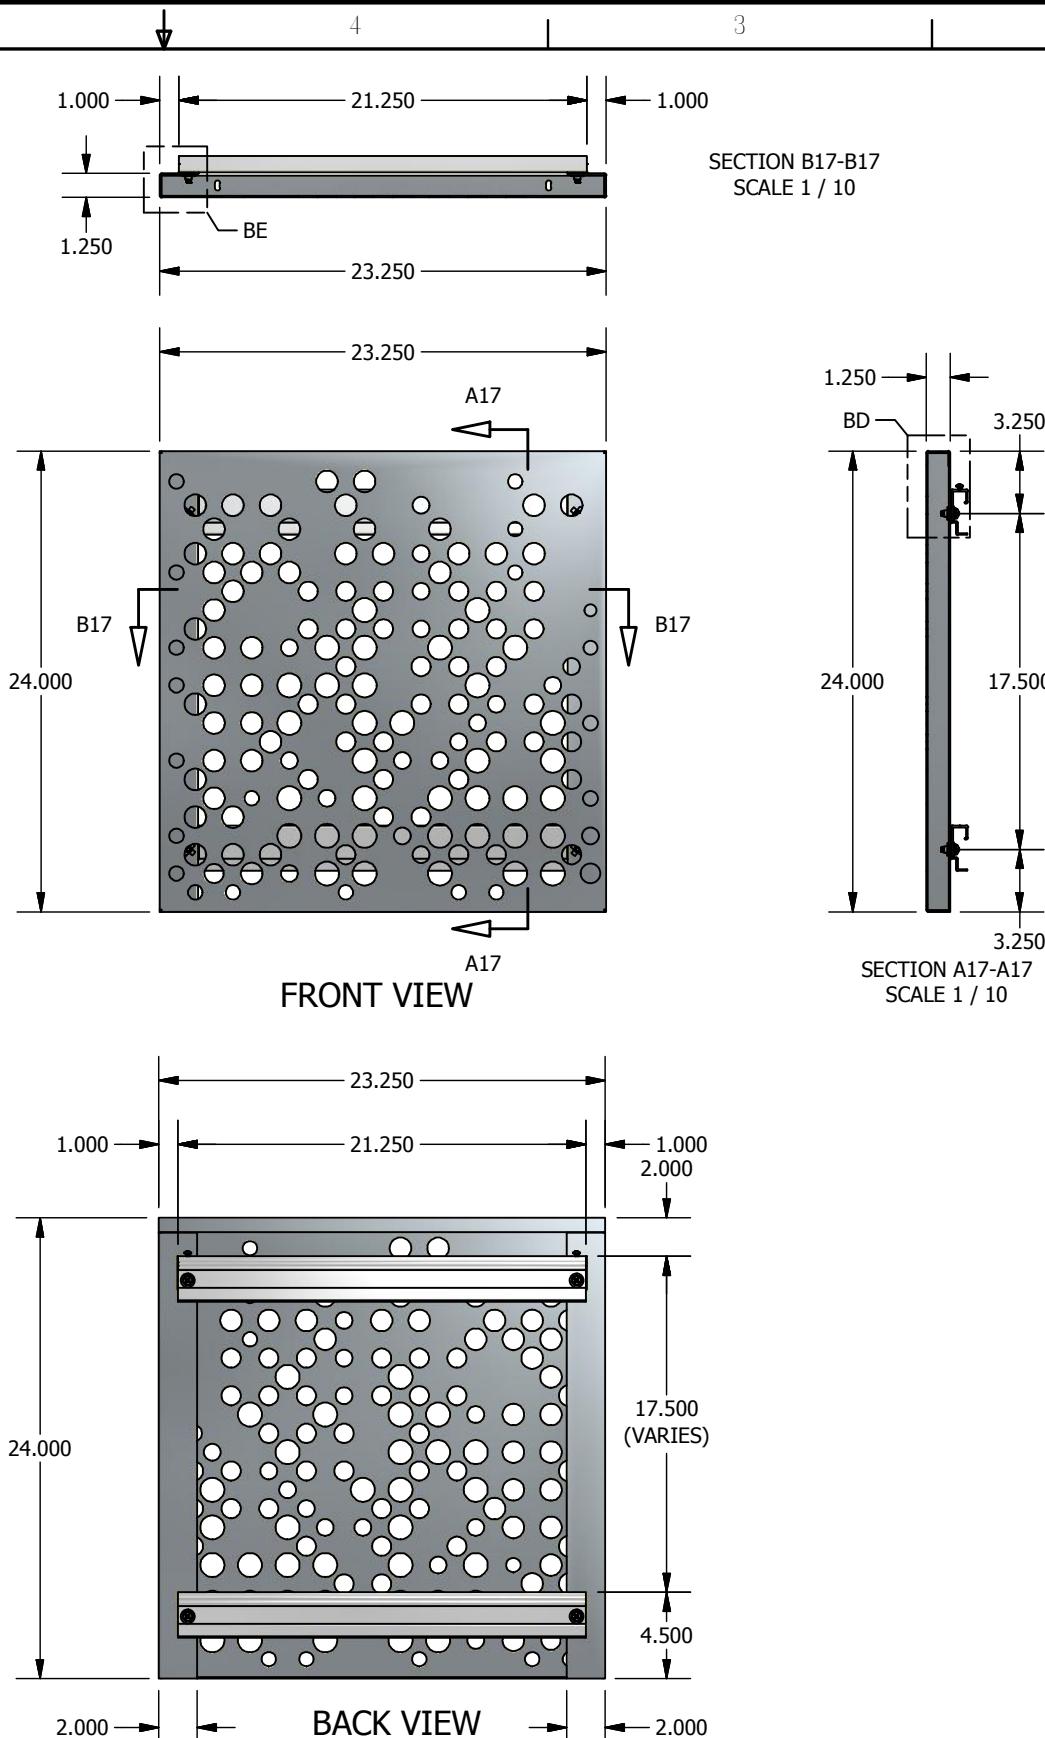

SECTION A17-A  
SCALE 1:10



ARCHITECTURAL METAL FABRICATION  
59<sup>20</sup> 56TH AVE.  
MASPETH, NY 11378  
(718) 844-1332

59-20 56TH AVE.  
MASPETH, NY 11378  
(718) 824-1512

---

CONTINUATION

325 KENT CONSTRUCTION LLC

---

ARCHITECT

TSMAEL LEVVA

**PROJECT** #

DOMINO ST

---

ITEM

FACADE

---

DRAWING

001\_ZINC PAN

WN

SP

**DATE**

7/28/2016 | A


LE

(AS SHOWN) | 26 / 37




1

8 7 6 5 4 3 2 1

PANEL ID	PANEL TYPE	BEND PROFILE	WIDTH (IN)	HEIGHT (IN)	PANEL TYPE (QTY)
Z000-1-000	HEAD	TYPE 3A	37.25	11.8125	22
Z000-1-010	HEAD	TYPE 3A	37.25	23.8125	20
Z000-1-390	HEAD	TYPE 3A	37.25	35.8125	1
PANEL TOTAL					43

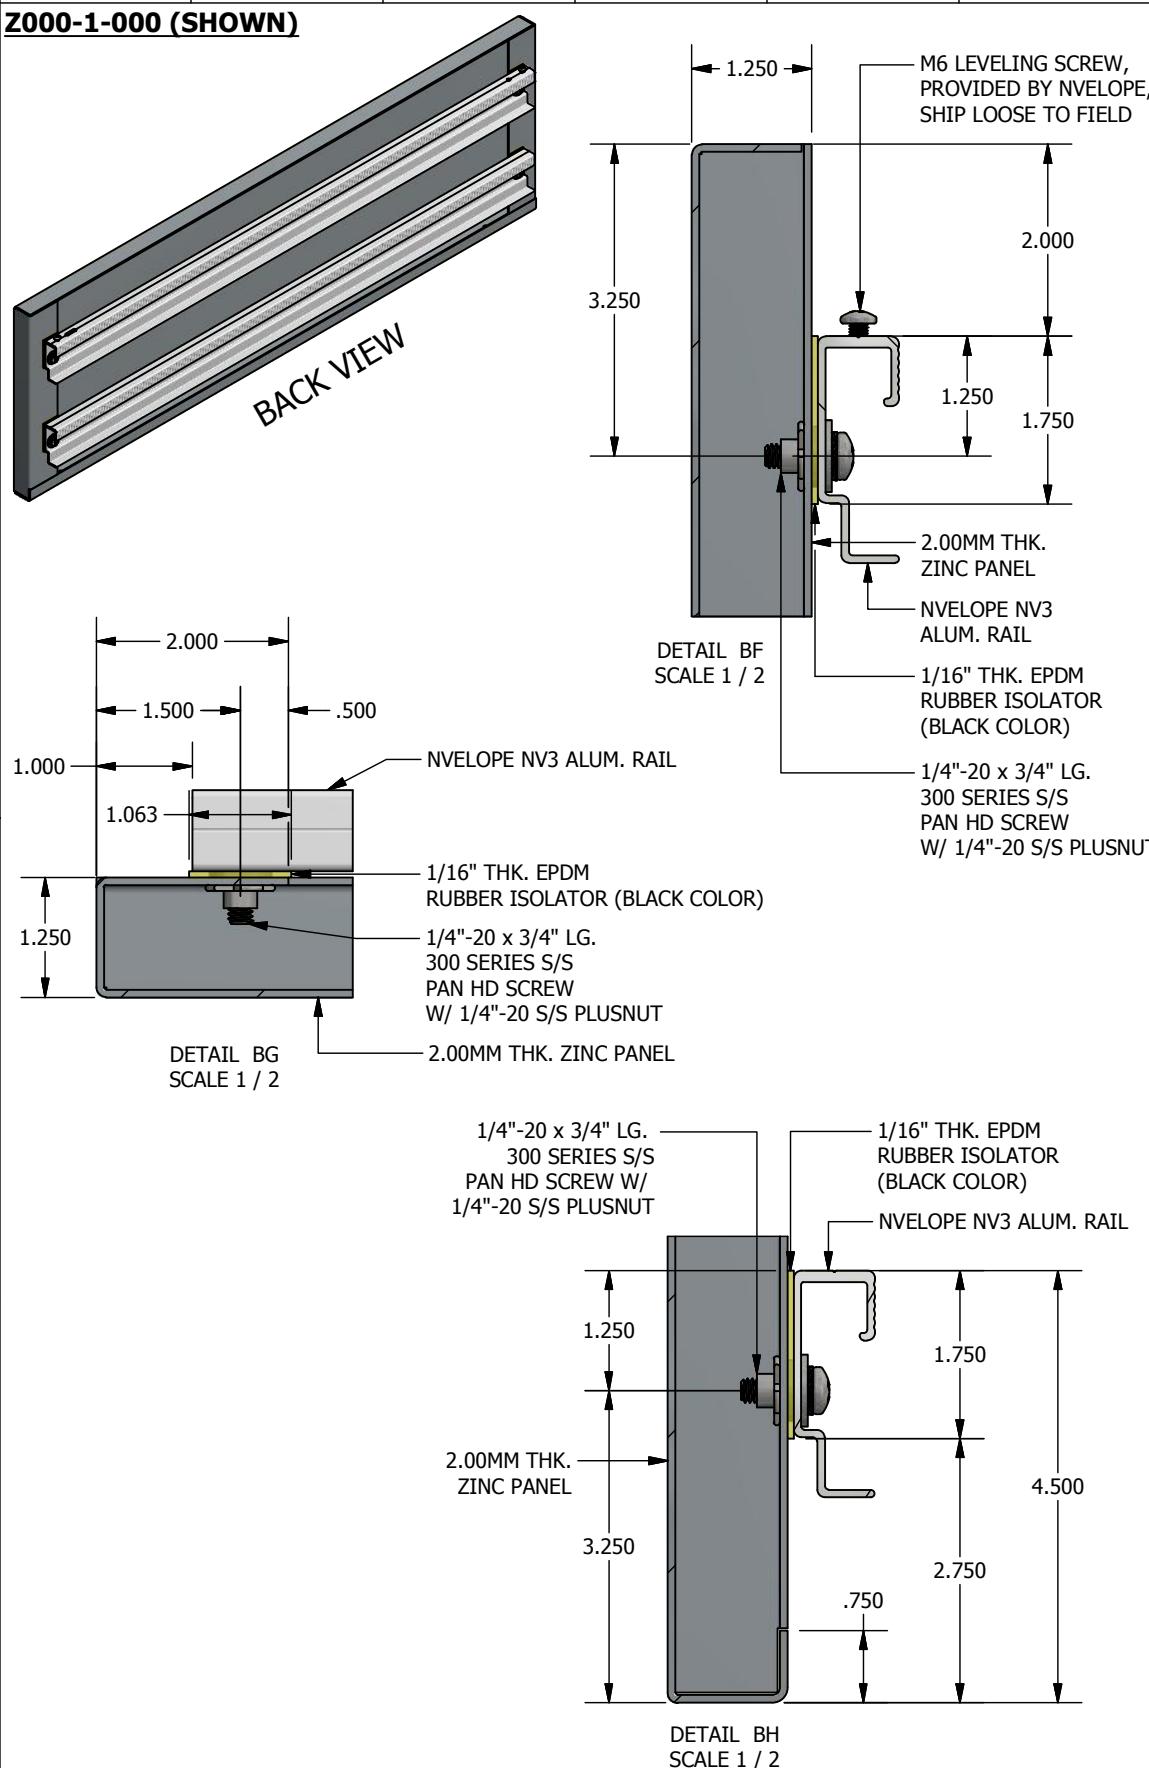**Z000-1-000 (SHOWN)**

\*PLEASE CONFIRM IF Z000-1-390 IS PERFORATED OR NON-PERFORATED

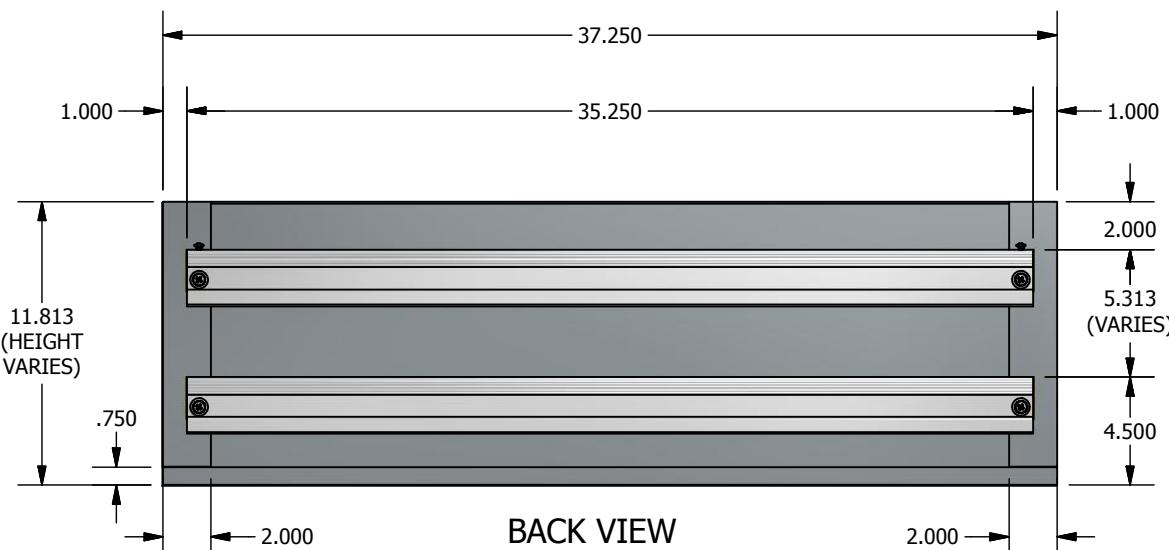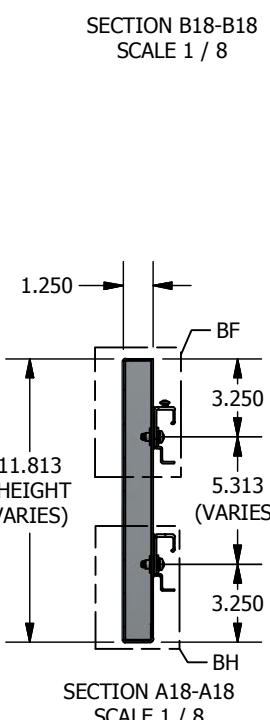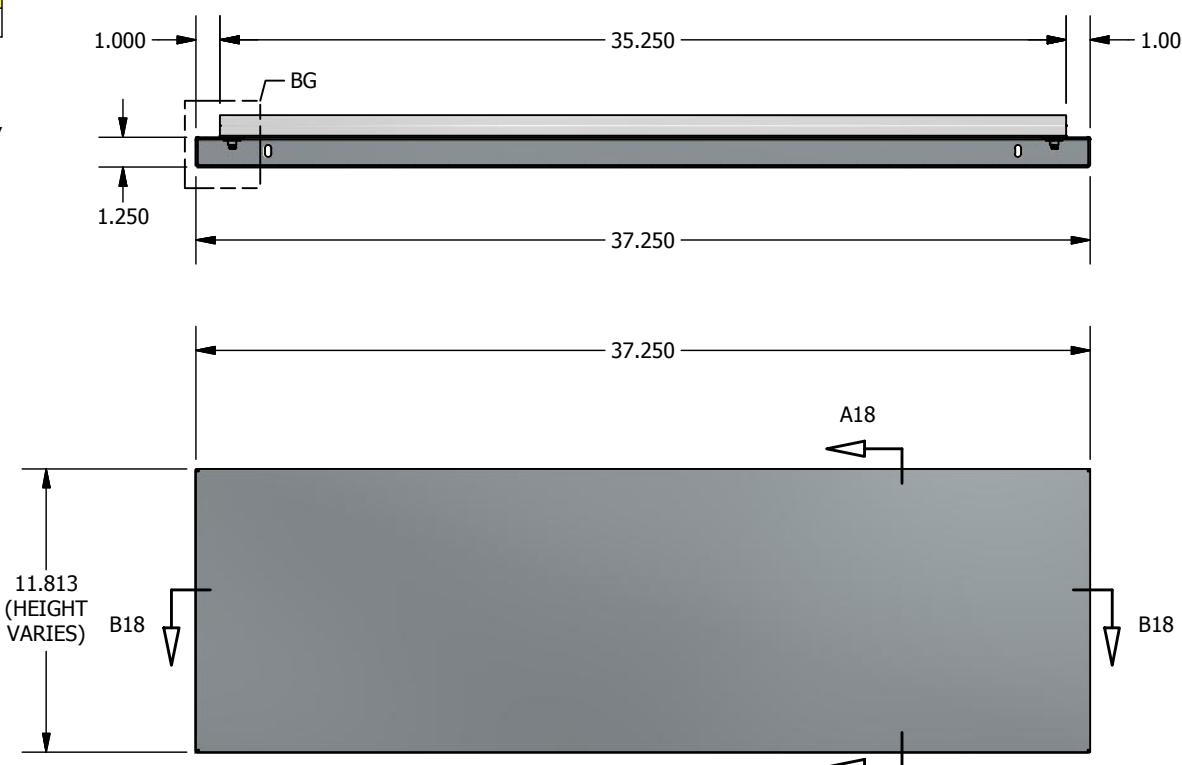

PART TAG:	Z000 'HEAD' PANELS: PANEL ID PER TABLE	ISSUE DATE	REVISION
QT:	(QTY) PER TABLE	7/28/2016	A
MATERIAL:	2.00MM ZINC	SCALE	SHEET NUMBER
FINISH:	ZINC - NATURAL; ALUM. - BLACK ANOD.	(AS SHOWN)	27 / 37
FLAT FILE:			



ARCHITECTURAL METAL FABRICATION  
59-20 56TH AVE.  
MASPETH, NY 11378  
(718) 894-1212

CONTRACTOR

325 KENT CONSTRUCTION LLC

ARCHITECT

ISMAEL LEYVA

PROJECT #

DOMINO SITE E

ITEM

FAÇADE

DRAWING

16001\_ZINC PANEL TYPES


DRAWN

SP

CHECKED


8 7 6 5 4 3 2 1

PANEL ID	PANEL TYPE	BEND PROFILE	WIDTH (IN)	HEIGHT (IN)	PANEL TYPE (QTY)
Z000-1-435	HEAD	TYPE 3A	47.25	6.25	5
Z000-1-436	HEAD	TYPE 3A	53.25	6.25	10
Z000-1-437	HEAD	TYPE 3A	23.25	6.25	9
Z000-1-440	HEAD	TYPE 3A	41.25	6.25	11
PANEL TOTAL					35


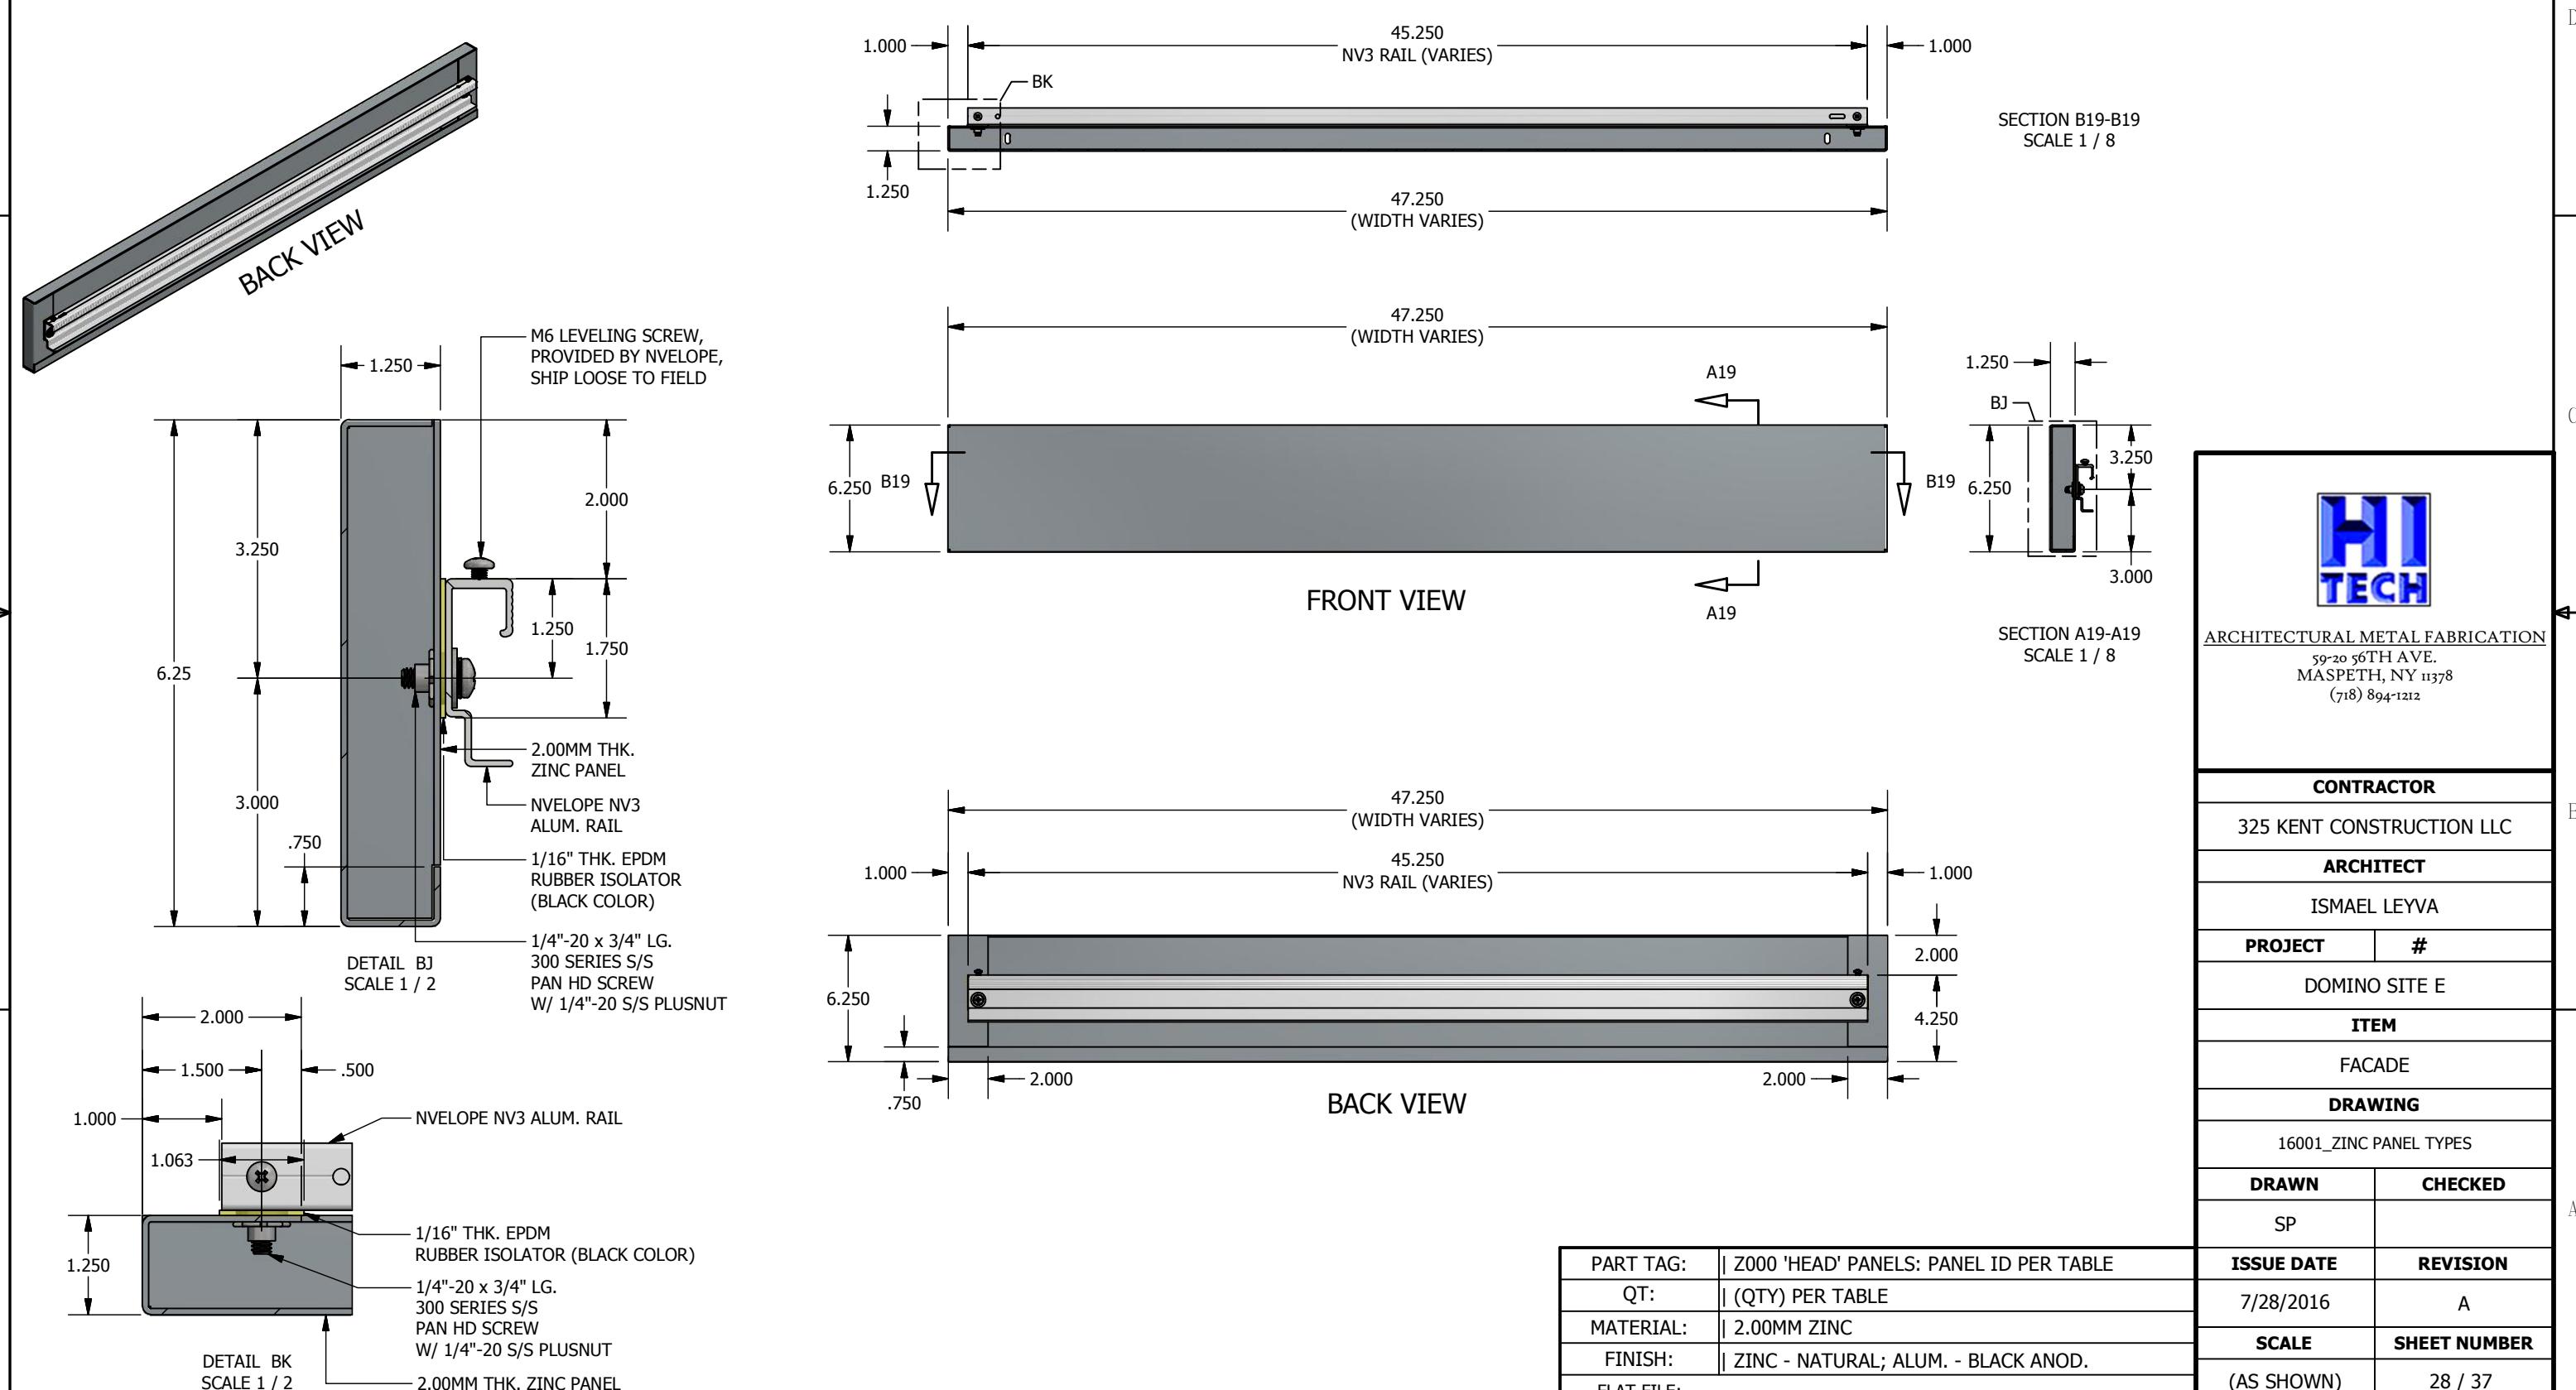
**Z000-1-435 (SHOWN)**

8 7 6 5 4 3 2 1

PANEL ID	PANEL TYPE	BEND PROFILE	WIDTH (IN)	HEIGHT (IN)	PANEL TYPE (QTY)
Z08A-1-000	HEAD	TYPE 3A	37.25	11.8125	1
Z08A-1-001	HEAD	TYPE 3A	37.25	23.8125	6
Z08A-2-000	HEAD	TYPE 3A	37.25	11.8125	7
Z08A-2-001	HEAD	TYPE 3A	37.25	23.8125	10
Z08A-2-002	HEAD	TYPE 3A	37.25	35.8125	1
PANEL TOTAL					25

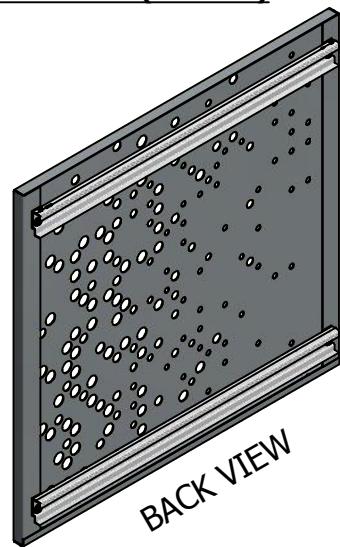**Z08A-2-002 (SHOWN)**

BACK VIEW

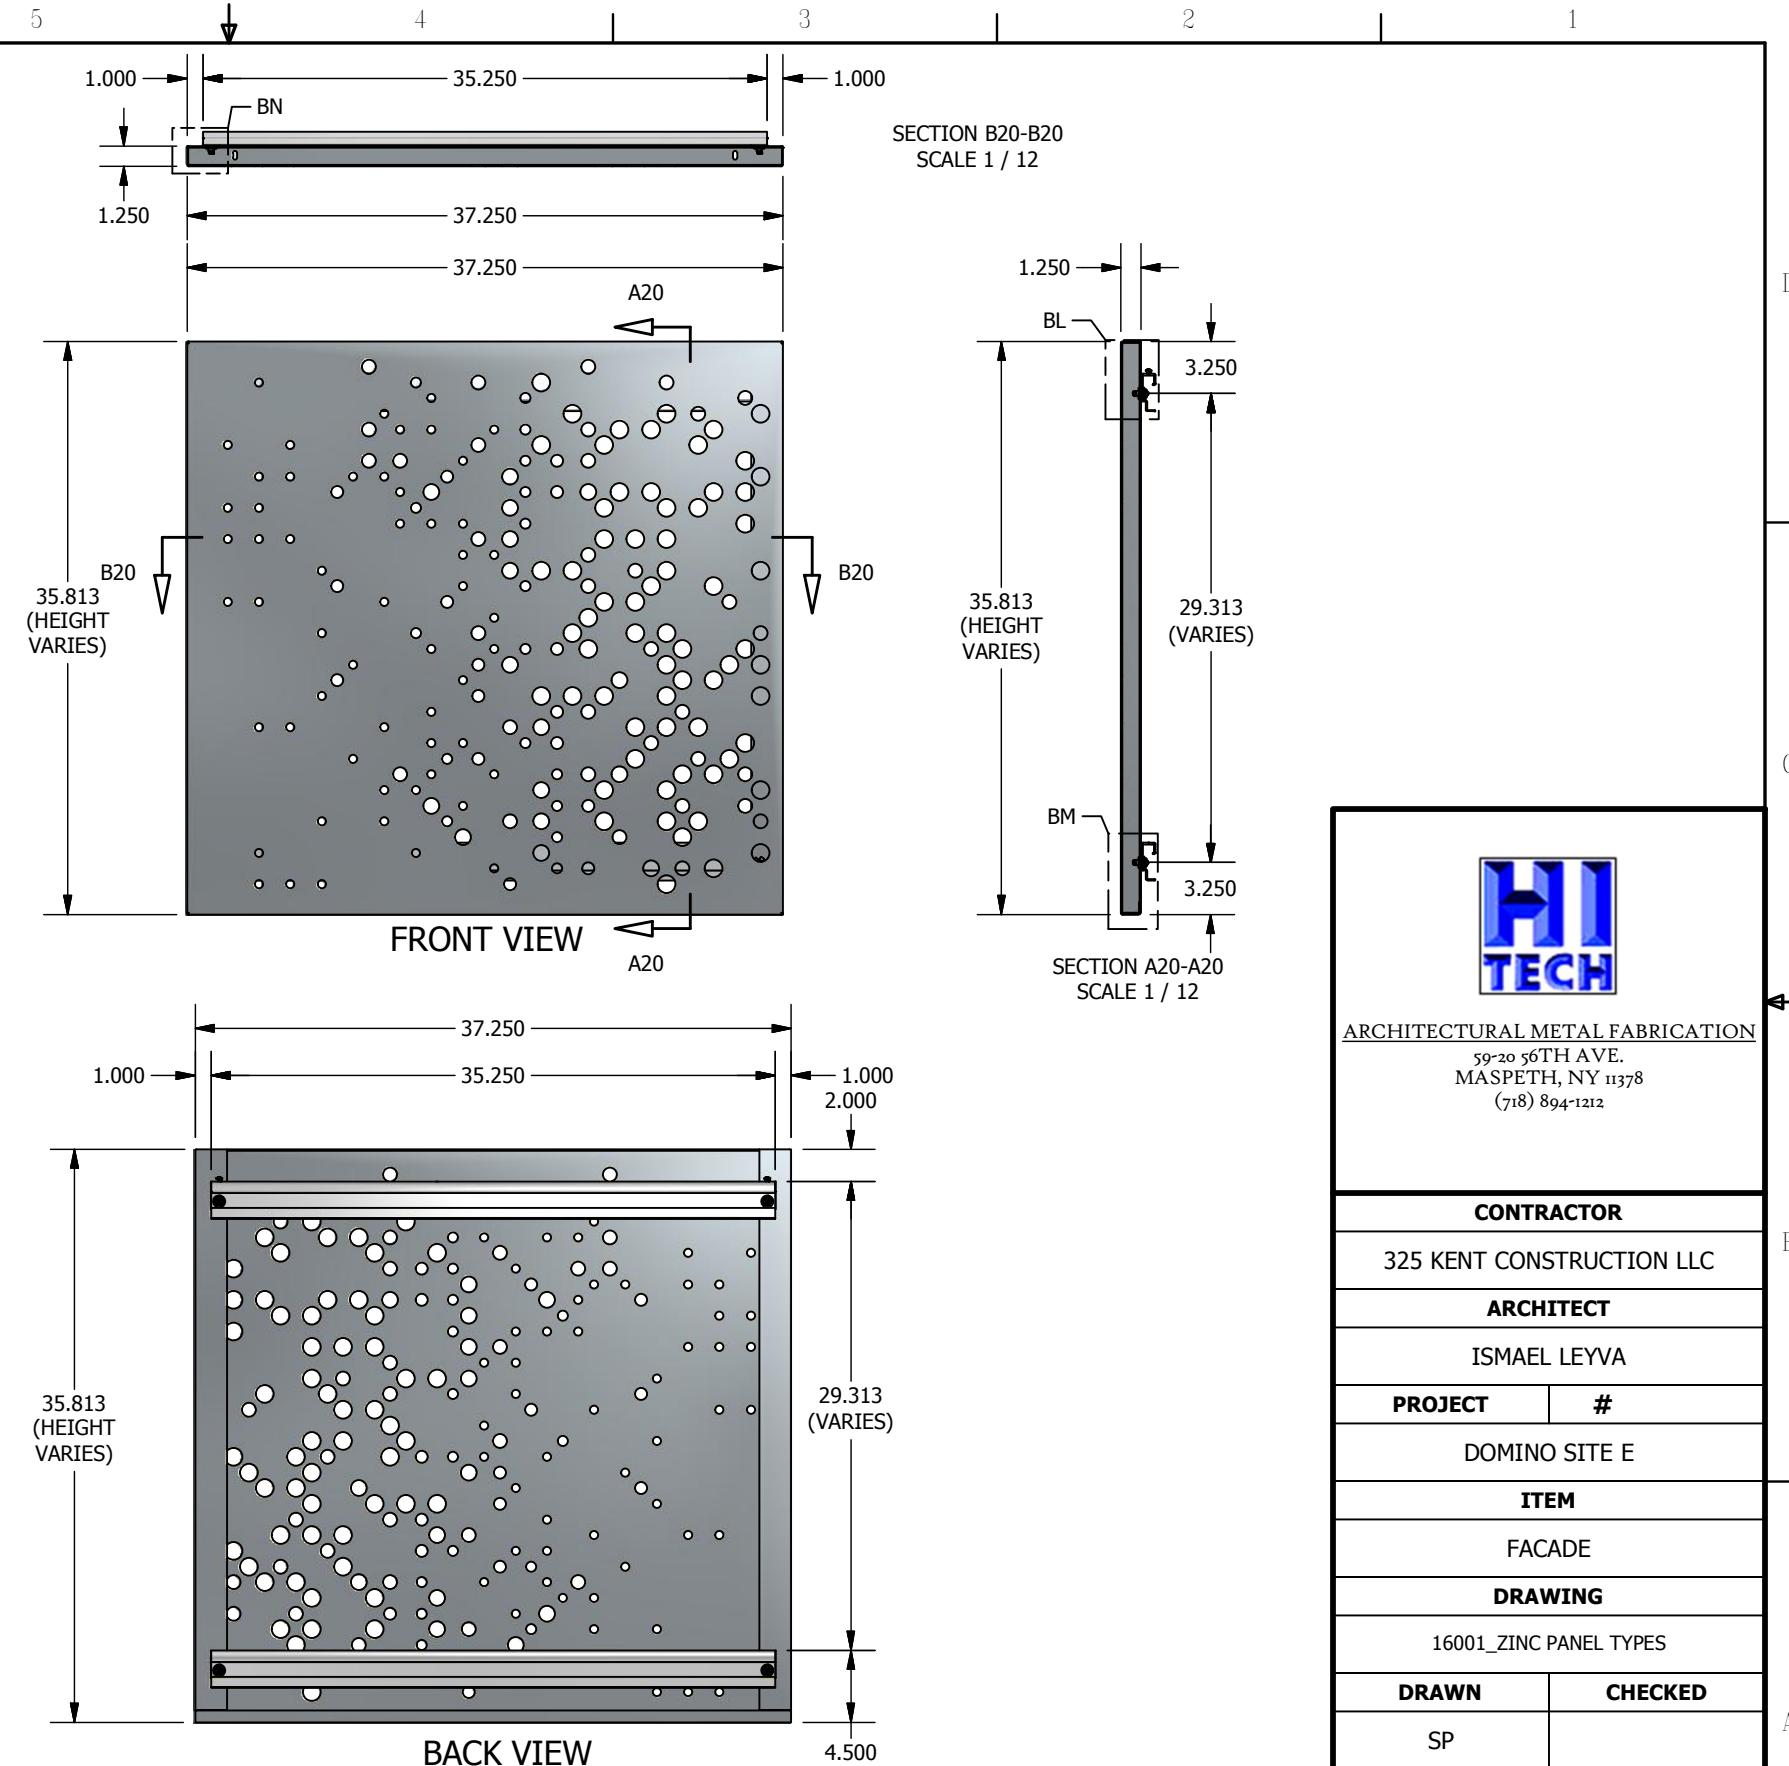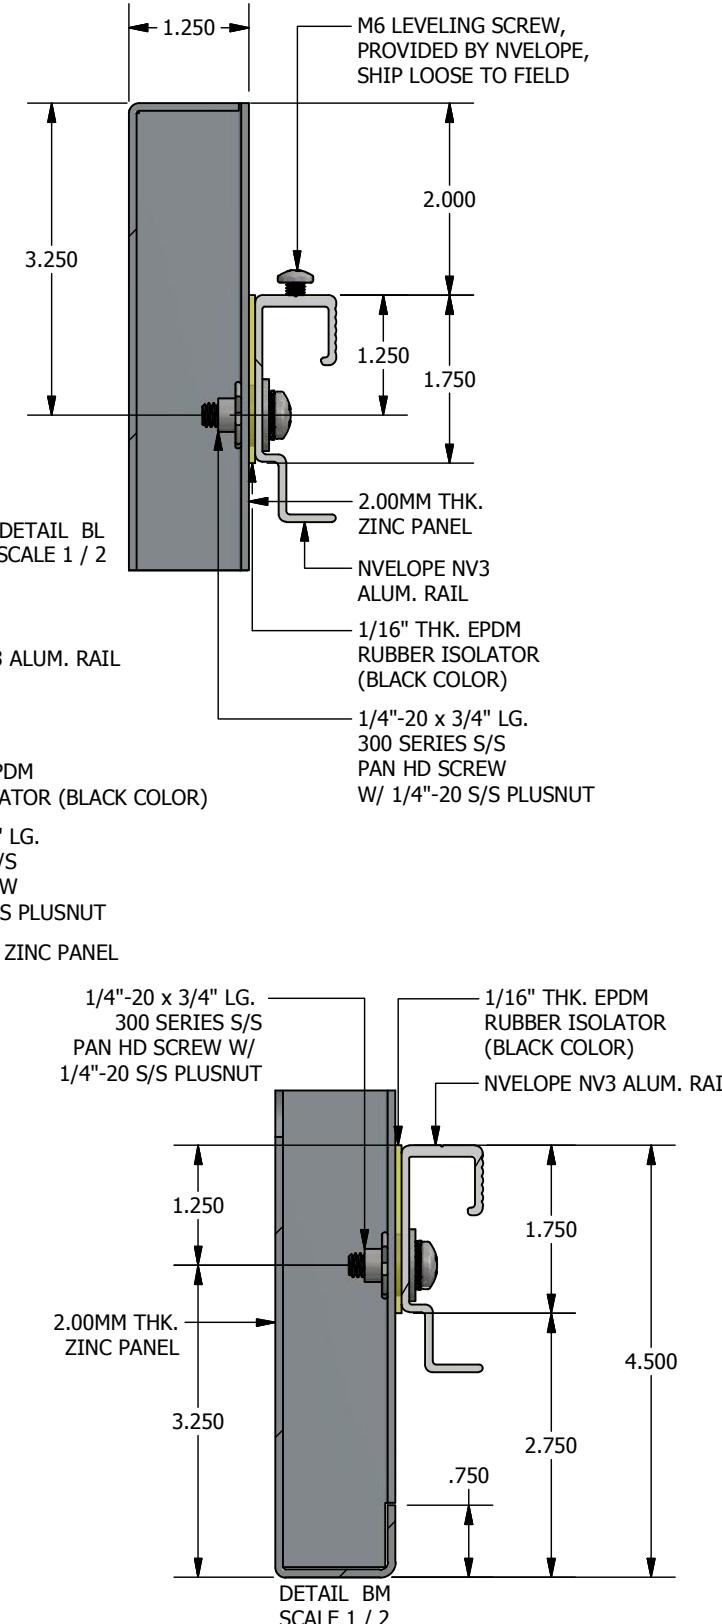

PART TAG:	Z08A 'HEAD' PANELS: PANEL ID PER TABLE	ISSUE DATE	
QT:	(QTY) PER TABLE	REVISION	A
MATERIAL:	2.00MM ZINC	7/28/2016	
FINISH:	ZINC - NATURAL; ALUM. - BLACK ANOD.	SCALE	
FLAT FILE:	(AS SHOWN)	SHEET NUMBER	29 / 37



ARCHITECTURAL METAL FABRICATION  
59-20 56TH AVE.  
MASPETH, NY 11378  
(718) 894-1212

**CONTRACTOR**

325 KENT CONSTRUCTION LLC

**ARCHITECT**

ISMAEL LEYVA

**PROJECT #**

DOMINO SITE E

**ITEM**

FAÇADE

**DRAWING**

16001\_ZINC PANEL TYPES

**DRAWN CHECKED**

SP

REVISION

A

SCALE

SHEET NUMBER


29 / 37

PANEL ID	PANEL TYPE	BEND PROFILE	WIDTH (IN)	HEIGHT (IN)	PANEL TYPE (QTY)
Z06A-1-001	RAILING	TYPE 4	71.25	36.125	1
Z06A-1-002	RAILING	TYPE 4	70.875	36.125	1
Z06A-1-003	RAILING	TYPE 4	62.5625	36.125	1
Z06A-1-004	RAILING	TYPE 4	71.25	36.125	1
TOTAL PANEL					4


**Z06A-1-001 (SHOWN)**




BACK VIEW

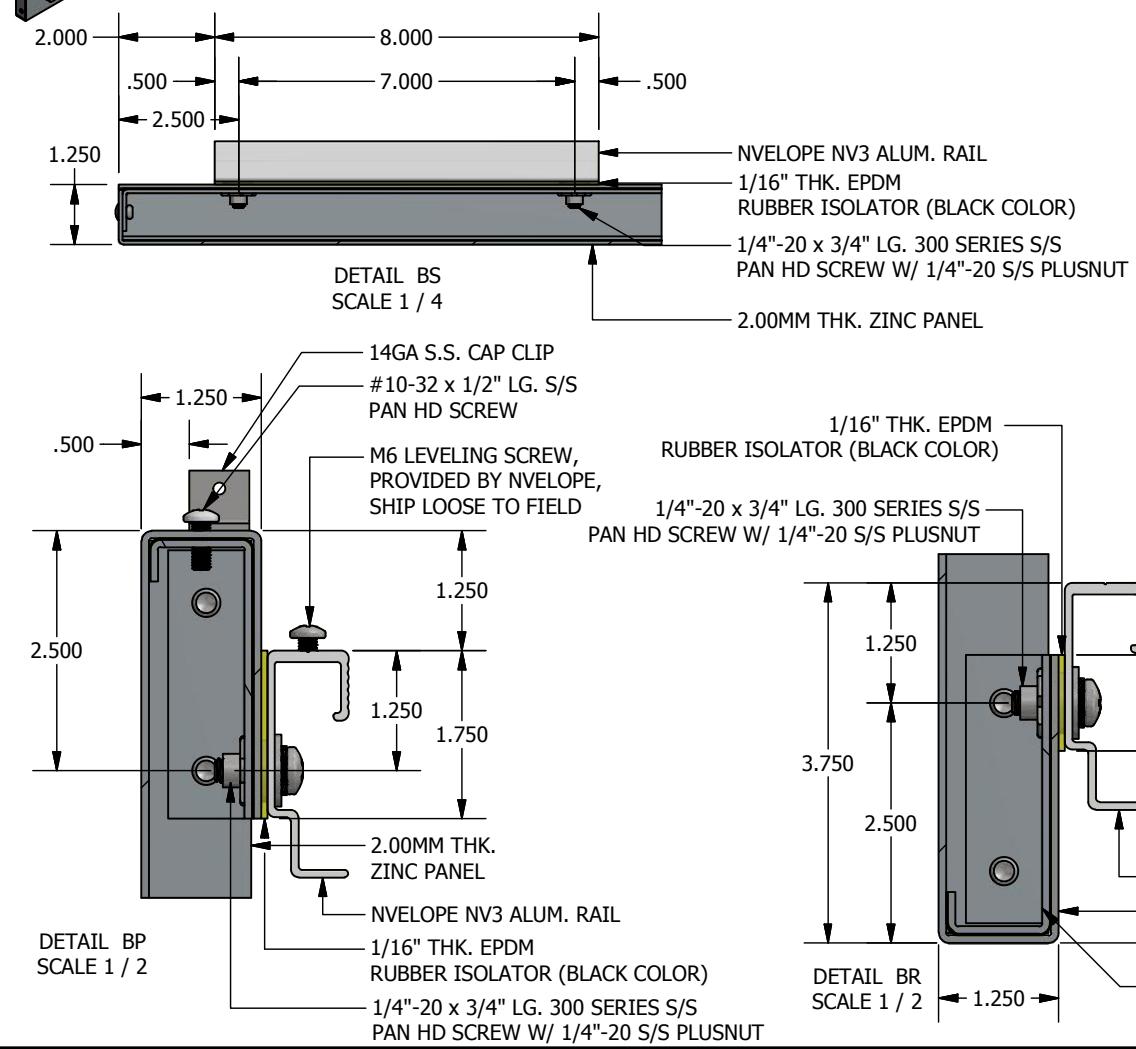


DETAIL B  
SCALE 1 / 2

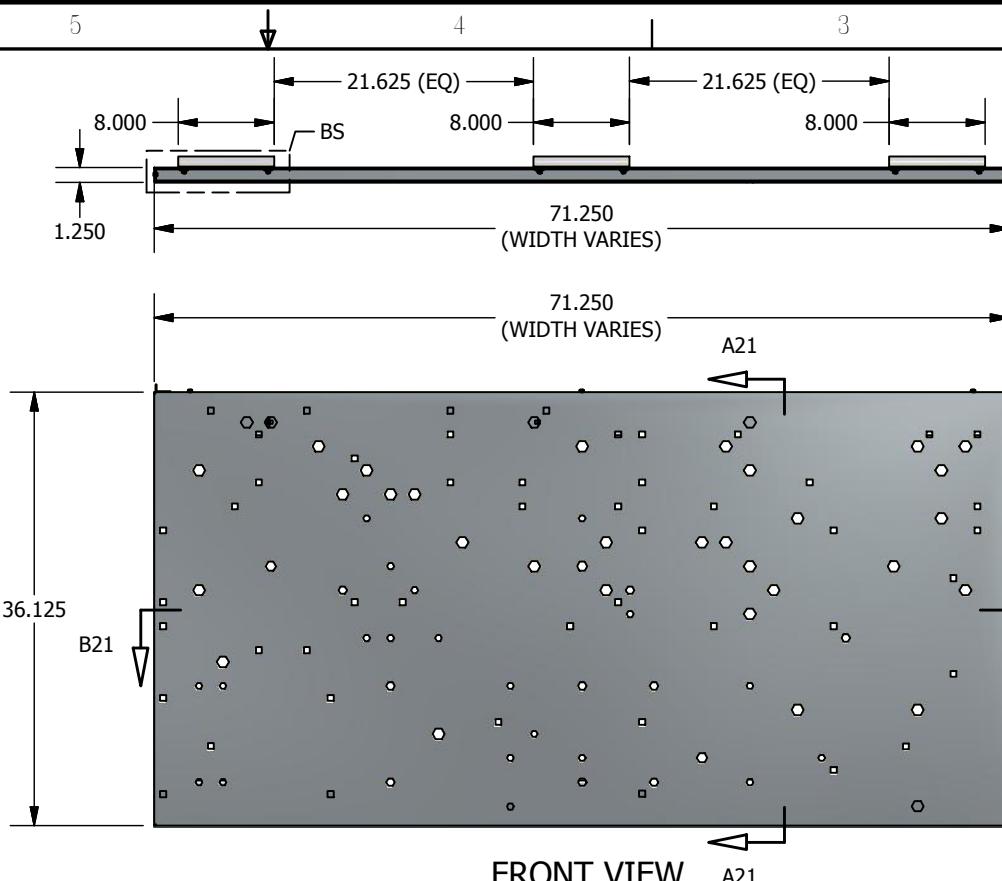

SECTION B21-B21  
SCALE 1 / 16

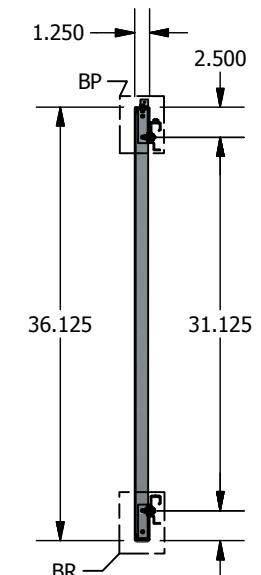

SECTION A21-A21  
SCALE 1 / 16

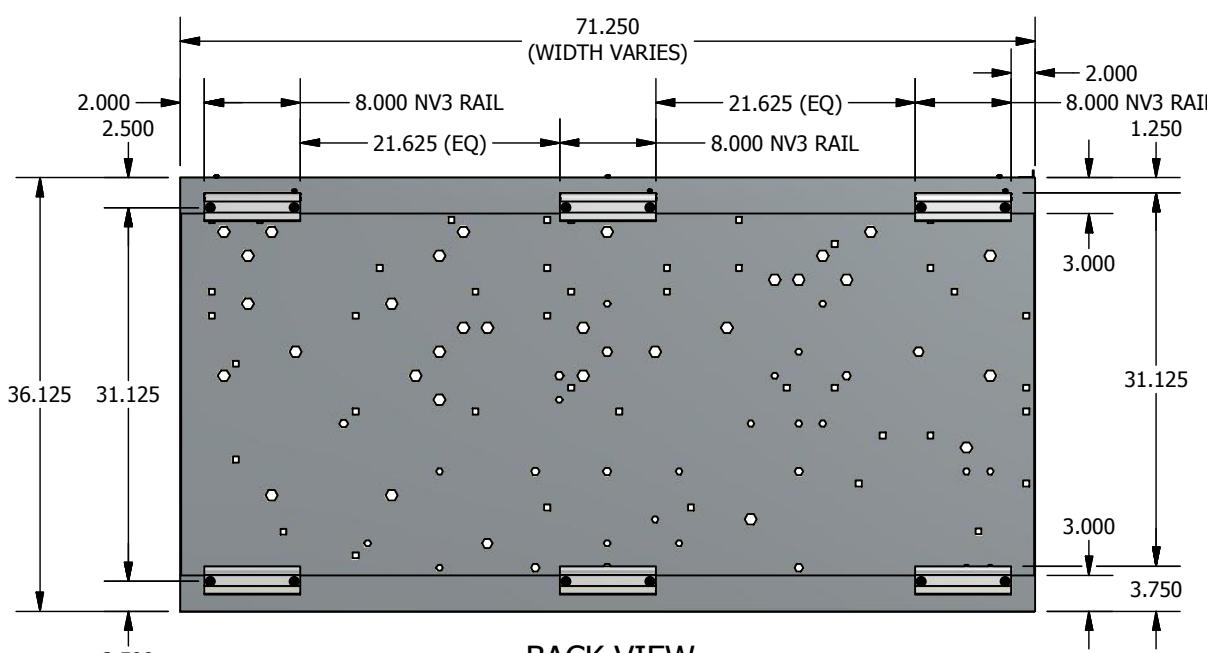


BACK VIEW

PART TAG:	'RAILING' PANELS: PANEL ID PER TABLE	ISSUE DATE	REVISION
QT:	(QTY) PER TABLE	7/28/2016	A
MATERIAL:	2.00MM ZINC	SCALE	SHEET NUMBER
FINISH:	ZINC - NATURAL; ALUM. - BLACK ANOD.	(AS SHOWN)	30 / 37
FLAT FILE:			


8 7 6 5 4 3 2 1

PANEL ID	PANEL TYPE	BEND PROFILE	WIDTH (IN)	HEIGHT (IN)	PANEL TYPE (QTY)
Z06A-1-000	RAILING	TYPE 4_CL	71.625	36.125	1
PANEL TOTAL					1

### Z06A-1-000 (SHOWN)

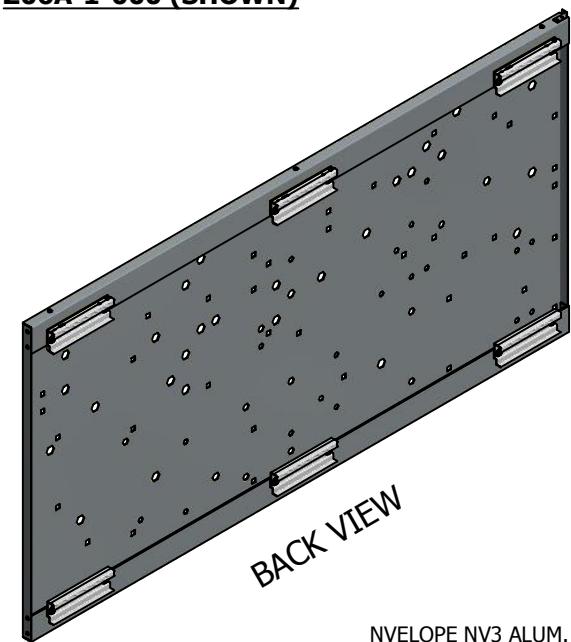

BACK VIEW

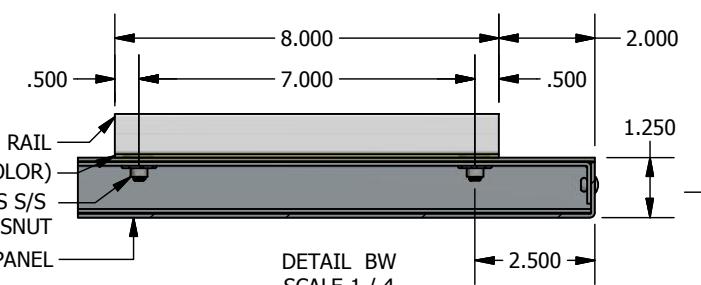


DETAIL BW  
SCALE 1 / 4





B22

PANEL ID	PANEL TYPE	BEND PROFILE	WIDTH (IN)	HEIGHT (IN)	PANEL TYPE (QTY)
Z06A-1-005	RAILING	TYPE 4_CR	71.625	36.125	1
TOTAL PANEL					1


**Z06A-1-005 (SHOWN)**

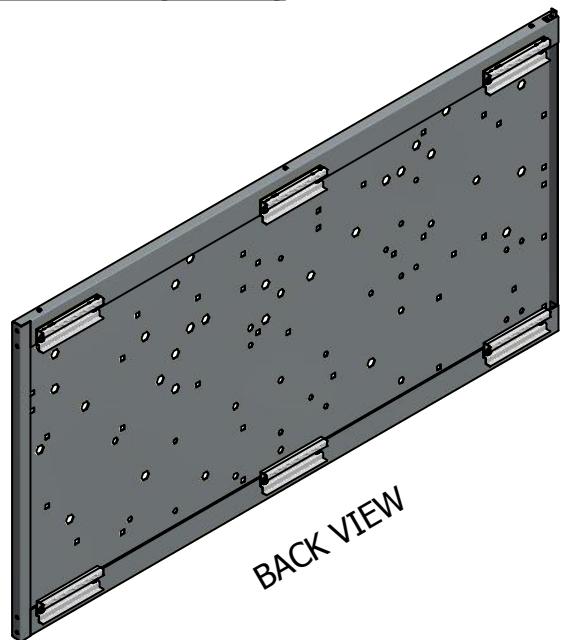


BACK VIEW

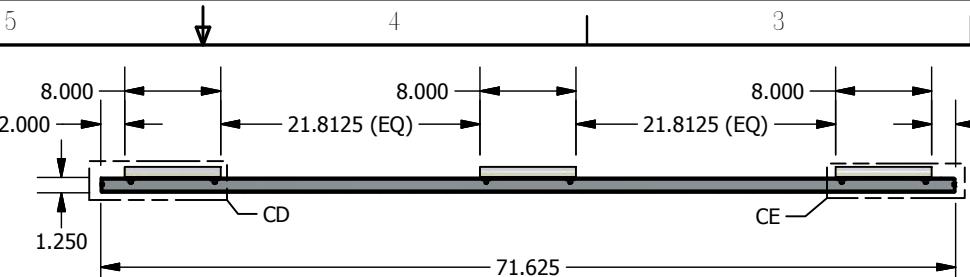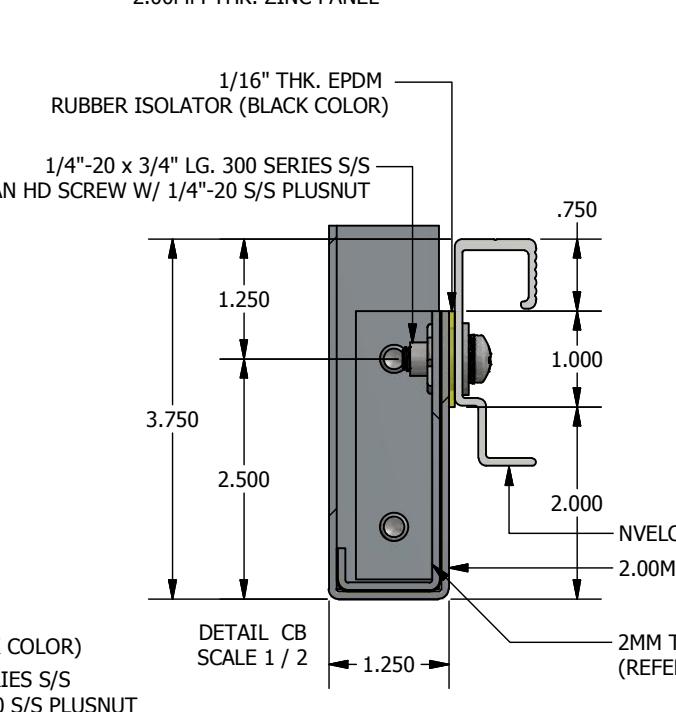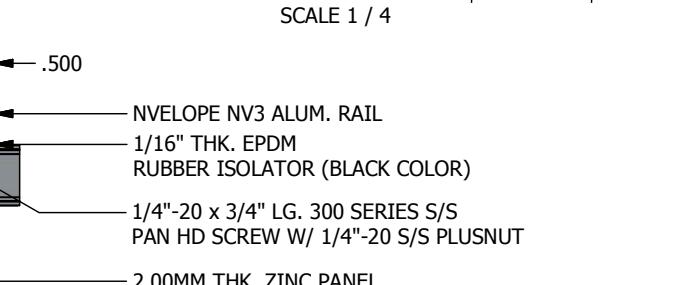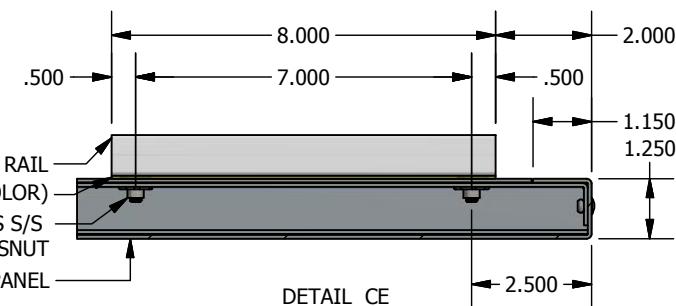


SECTION B23-B23  
SCALE 1 / 16

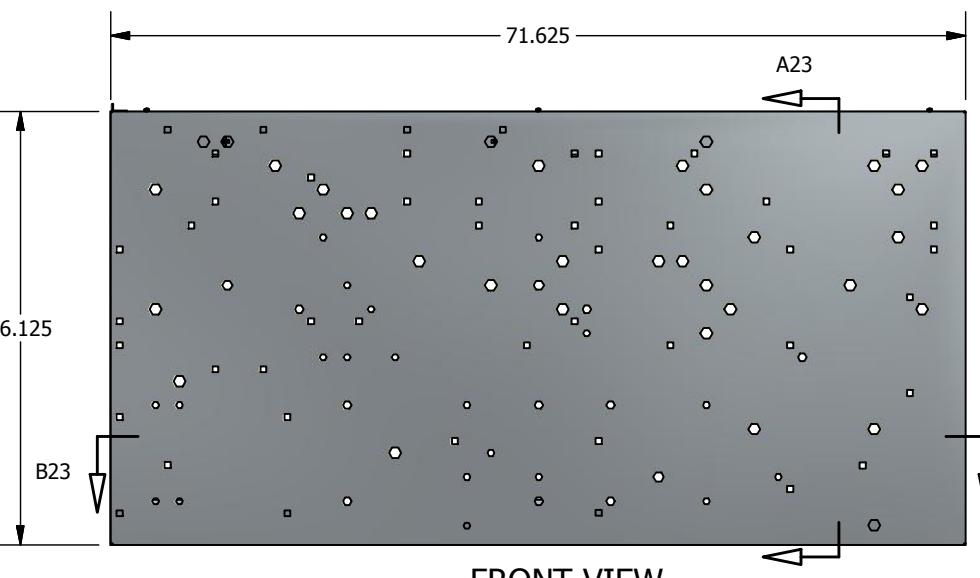

FRONT VIEW

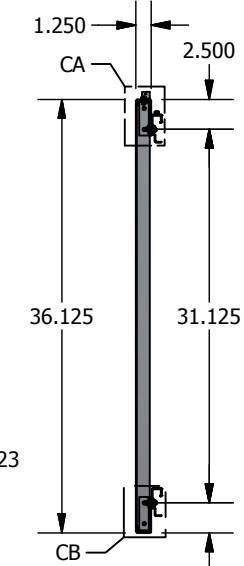

2.500  
SECTION A23-A23  
SCALE 1 / 16

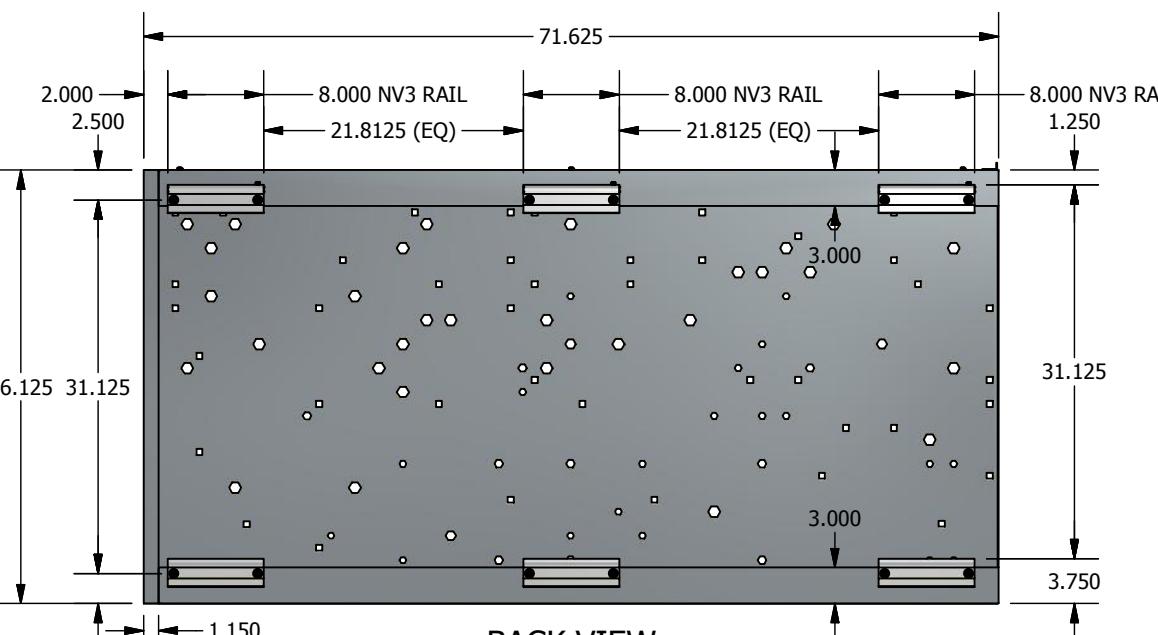

## BACK VIEW


PART TAG:	CORNER RIGHT 'RAILING' PANELS: PANEL ID PER TABLE	ISSUE DATE	REVISION
QT:	(QTY) PER TABLE	7/28/2016	A
MATERIAL:	2.00MM ZINC	SCALE	SHEET NUMBER
FINISH:	ZINC - NATURAL; ALUM. - BLACK ANOD.		
FLAT FILE:		(AS SHOWN)	32 / 37

8 7 6 5 4 3 2 1


PANEL ID	PANEL TYPE	BEND PROFILE	WIDTH (IN)	HEIGHT (IN)	PANEL TYPE (QTY)
Z11A-1-000	BALCONY	TYPE 4	59.75	34.25	15
Z11A-1-001	BALCONY	TYPE 4	61	34.25	30
Z11A-1-002	BALCONY	TYPE 4	61.25	34.25	42
Z11A-1-003	BALCONY	TYPE 4	60.25	34.25	8
PANEL TOTAL					95

**Z11A-1-002 (SHOWN)**

\*BALCONY PANELS HOLD FOR FURTHER COORDINATION

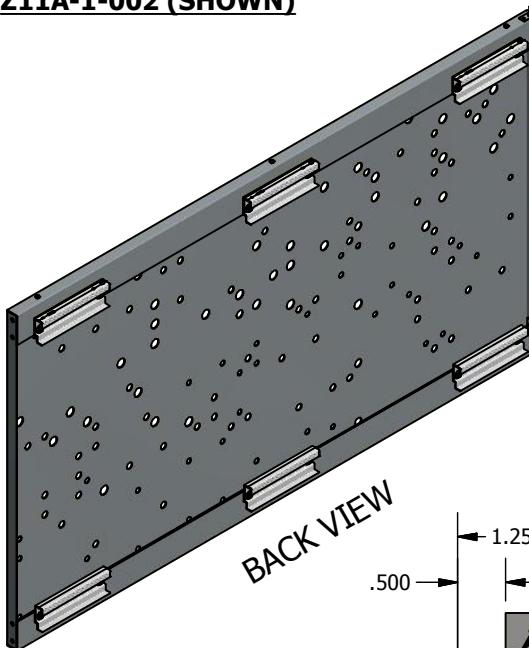

BACK VIEW

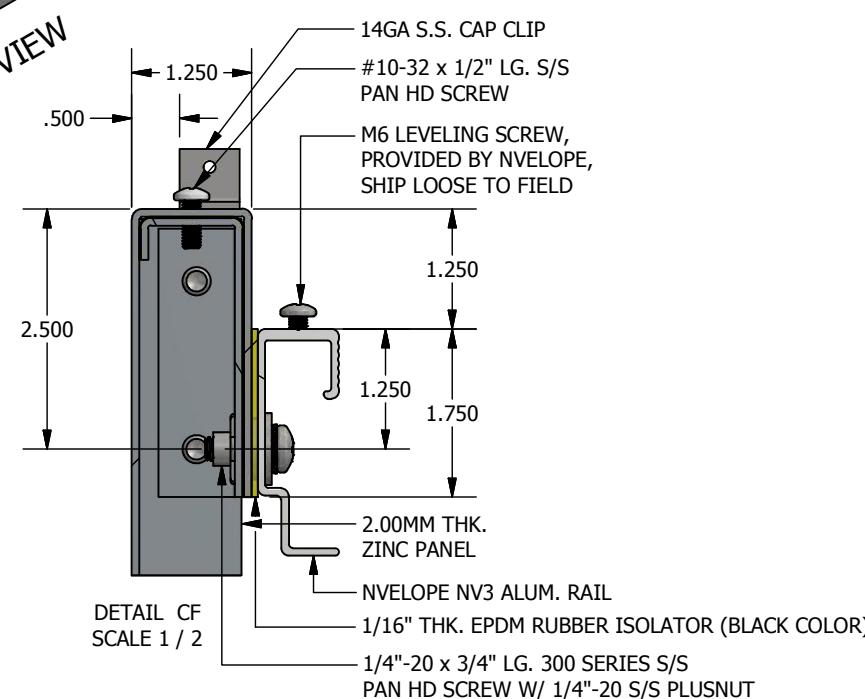

1/16" THK. EPDM RUBBER ISOLATOR (BLACK COLOR)

1/4"-20 x 3/4" LG. 300 SERIES S/S PAN HD SCREW W/ 1/4"-20 S/S PLUSNUT

1.250

.750






1.250

2.500

2.000

2MM THK. ZINC STIFFENER (REFER TO HTMI STIFFENER DETAIL)

DETAIL CG SCALE 1 / 2

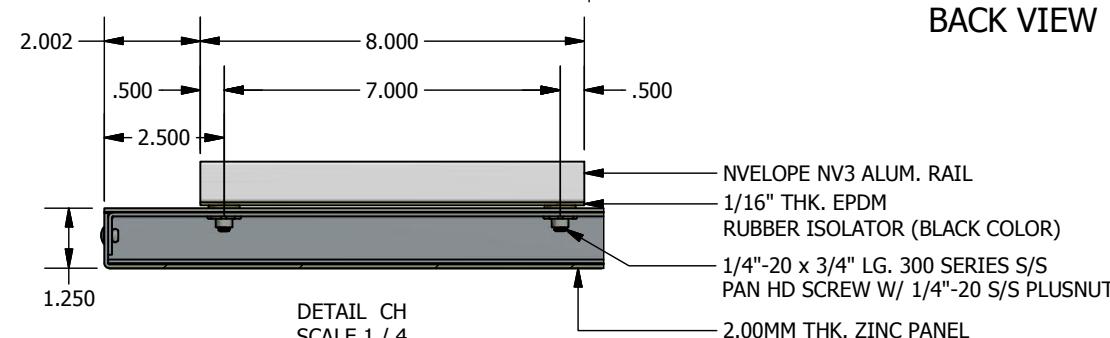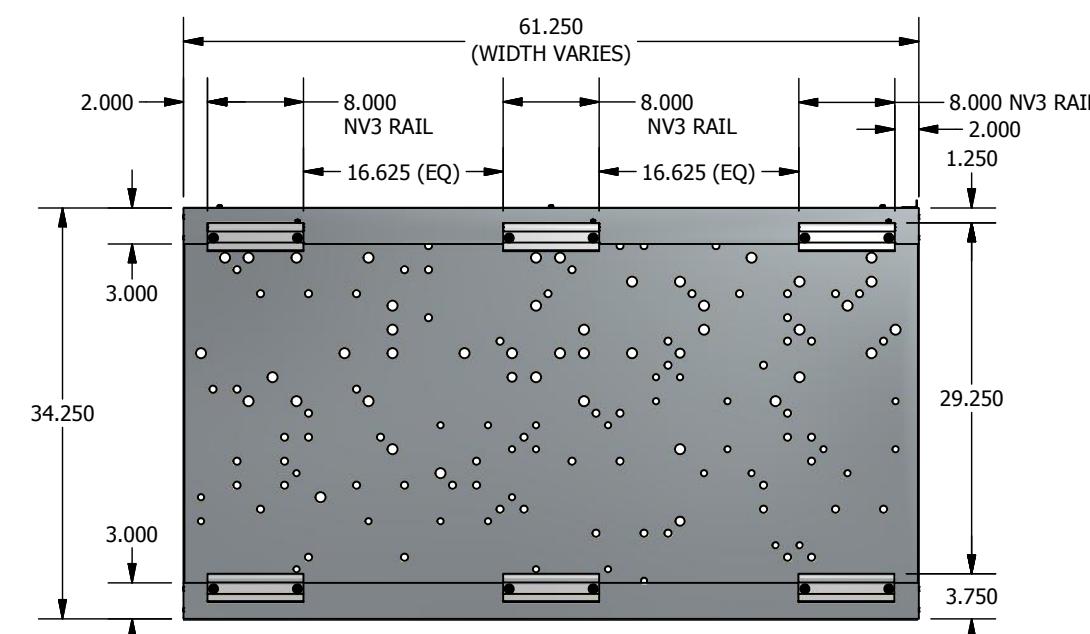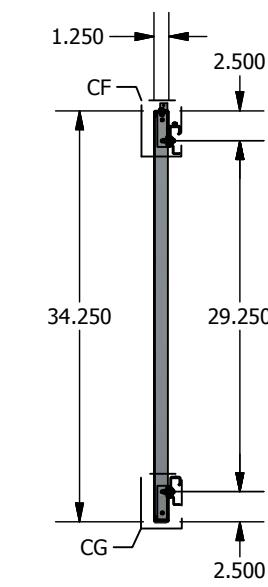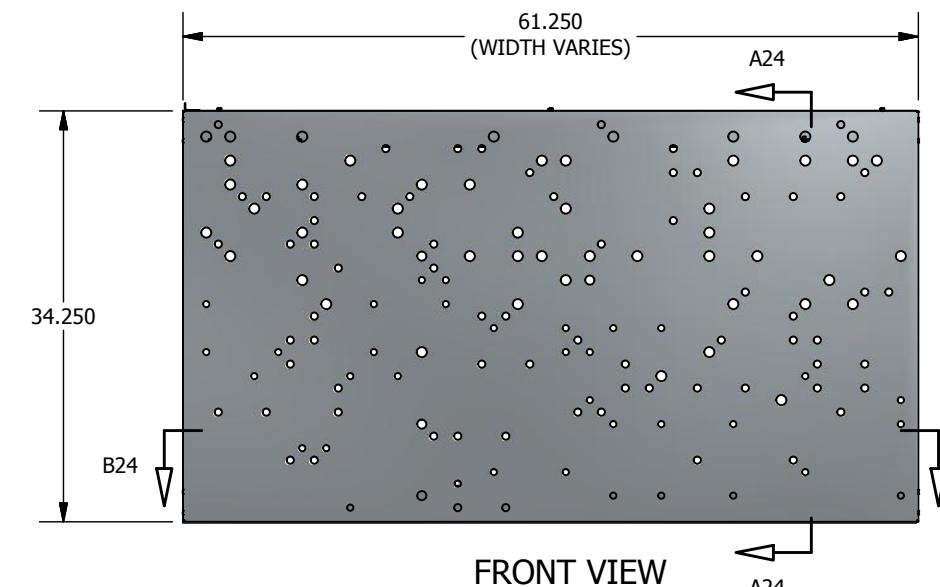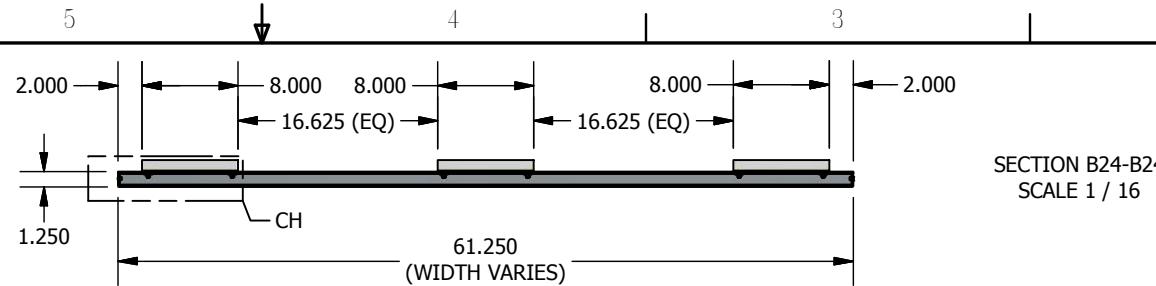

PART TAG:	'BALCONY' PANELS: PANEL ID PER TABLE
QT:	(QTY) PER TABLE
MATERIAL:	2.00MM ZINC
FINISH:	ZINC - NATURAL; ALUM. - BLACK ANOD.
FLAT FILE:	



ARCHITECTURAL METAL FABRICATION  
59-20 56TH AVE.  
MASPETH, NY 11378  
(718) 894-1212

**CONTRACTOR**

325 KENT CONSTRUCTION LLC

**ARCHITECT**

ISMAEL LEYVA

**PROJECT #**

DOMINO SITE E

**ITEM**

FAÇADE

**DRAWING**

16001\_ZINC PANEL TYPES

**DRAWN CHECKED**

SP

**ISSUE DATE REVISION**

7/28/2016 A

**SCALE SHEET NUMBER**

(AS SHOWN) 33 / 37

8

7

6

5

4

3

2


1

PANEL ID	PANEL TYPE	BEND PROFILE	WIDTH (IN)	HEIGHT (IN)	PANEL TYPE (QTY)
Z06A-2-000	RAILING	TYPE 4A_CL	66.875	40.000	1
Z06A-2-001	RAILING	TYPE 4A	71.25	40.000	1
Z06A-2-002	RAILING	TYPE 4A	70.875	40.000	1
Z06A-2-003	RAILING	TYPE 4A	62.5625	40.000	1
Z06A-2-004	RAILING	TYPE 4A	71.25	40.000	1
Z06A-2-005	RAILING	TYPE 4A_CR	66.875	40.000	1
Z11A-2-000	BALCONY	TYPE 4A	59.75	40.000	15
Z11A-2-001	BALCONY	TYPE 4A	61	40.000	30
Z11A-2-002	BALCONY	TYPE 4A	61.25	40.000	42
Z11A-2-003	BALCONY	TYPE 4A	60.25	40.000	8
PANEL TOTAL					101


**Z06A-2-001 (SHOWN)**

\*BALCONY BACK PANELS HOLD FOR  
FURTHER COORDINATION





FOR RAILING BACK PANELS, THE PANEL ID CORRESPONDS TO  
ILA PERFORATION DRAWING Z06A-1 AND Z11A-1.

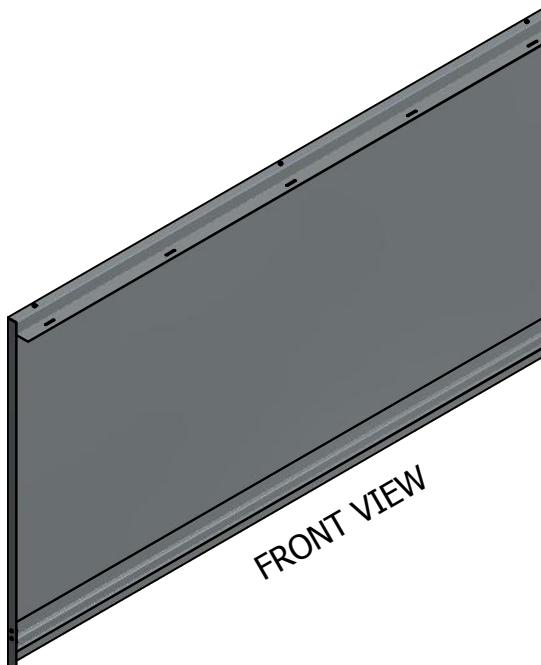

FRONT VIEW

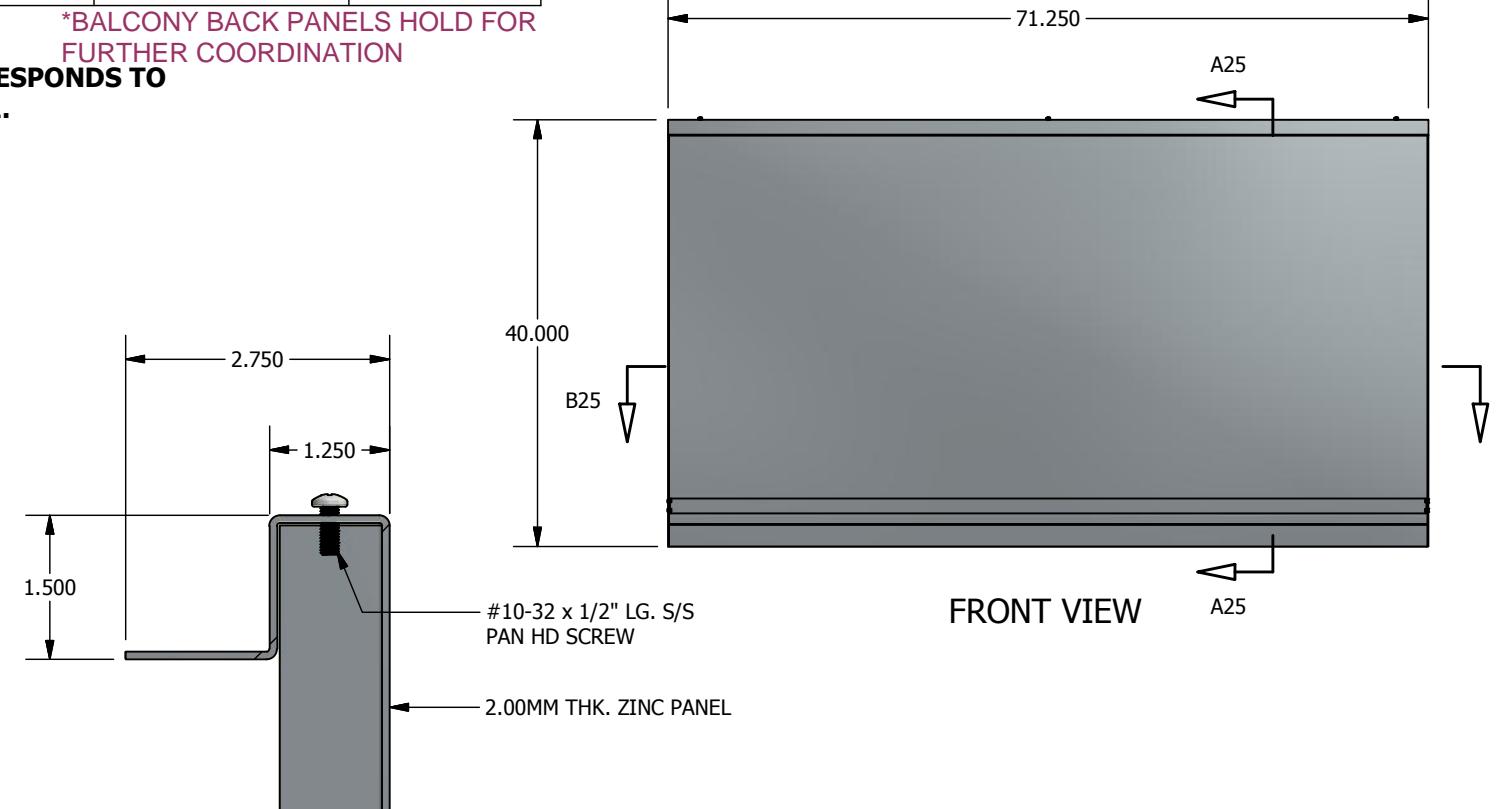

FRONT VIEW

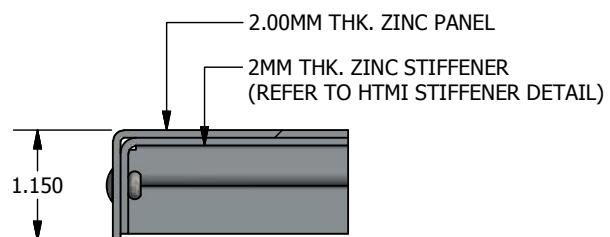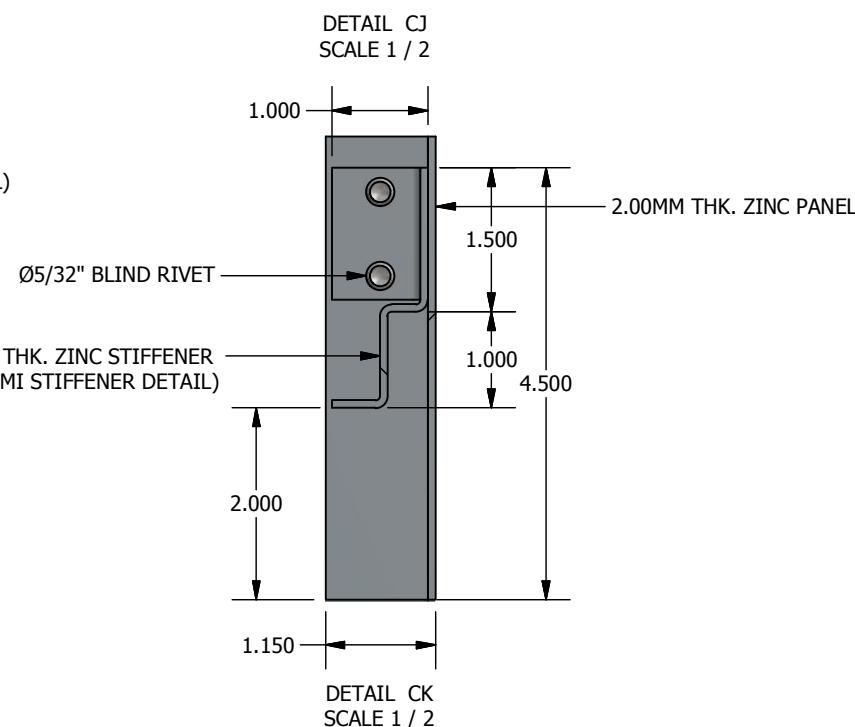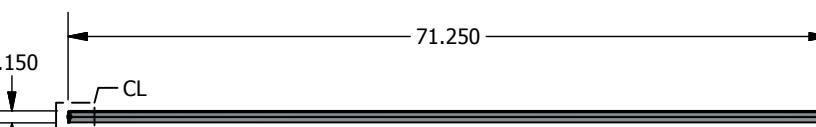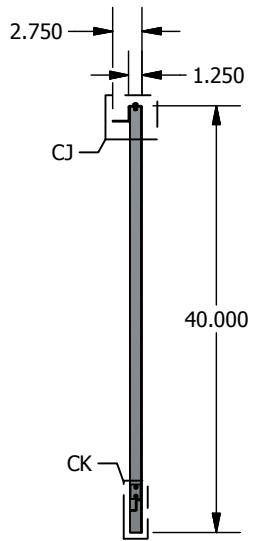DETAIL CL  
SCALE 1 / 2DETAIL CK  
SCALE 1 / 2SECTION B25-B25  
SCALE 1 / 18SECTION A25-A25  
SCALE 1 / 18

ARCHITECTURAL METAL FABRICATION  
59-20 56TH AVE.  
MASPETH, NY 11378  
(718) 894-1212

**CONTRACTOR**

325 KENT CONSTRUCTION LLC

**ARCHITECT**

ISMAEL LEYVA

**PROJECT #**

DOMINO SITE E

**ITEM**

FAÇADE

**DRAWING**

16001\_ZINC PANEL TYPES

**DRAWN CHECKED**

SP

**ISSUE DATE REVISION**

7/28/2016 A

**SCALE SHEET NUMBER**


(AS SHOWN) 34 / 37

PART TAG:	'RAILING/BALCONY BACK' PANELS: PANEL ID PER TABLE
QT:	(QTY) PER TABLE
MATERIAL:	2.00MM ZINC
FINISH:	ZINC - NATURAL; ALUM. - BLACK ANOD.
FLAT FILE:	


8 7 6 5 4 3 2 1

PANEL ID	PANEL TYPE	BEND PROFILE	WIDTH (IN)	HEIGHT (IN)	PANEL TYPE (QTY)
Z06A-1-001	RAILING	TYPE 4B	71.25	6.750	1
Z06A-1-002	RAILING	TYPE 4B	70.875	6.750	1
Z06A-1-003	RAILING	TYPE 4B	62.5625	6.750	1
Z06A-1-004	RAILING	TYPE 4B	71.25	6.750	1
Z11A-1-000	BALCONY	TYPE 4B	59.75	6.750	15
Z11A-1-001	BALCONY	TYPE 4B	61	6.750	30
Z11A-1-002	BALCONY	TYPE 4B	61.25	6.750	42
Z11A-1-003	BALCONY	TYPE 4B	60.25	6.750	8
PANEL TOTAL					99


\*BALCONY CAP PANELS HOLD FOR  
FURTHER COORDINATION

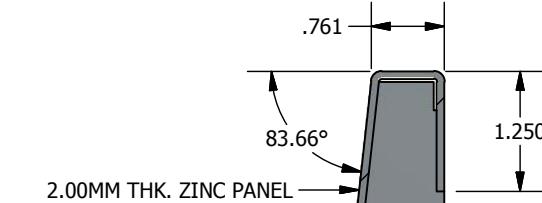


DETAIL CM  
SCALE 1 / 2

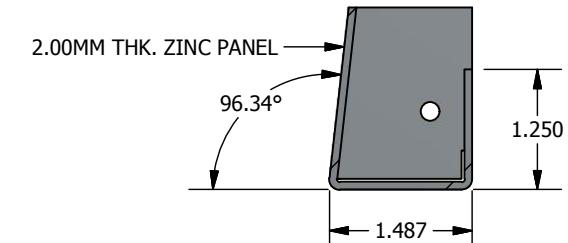


DETAIL CN  
SCALE 1 / 2

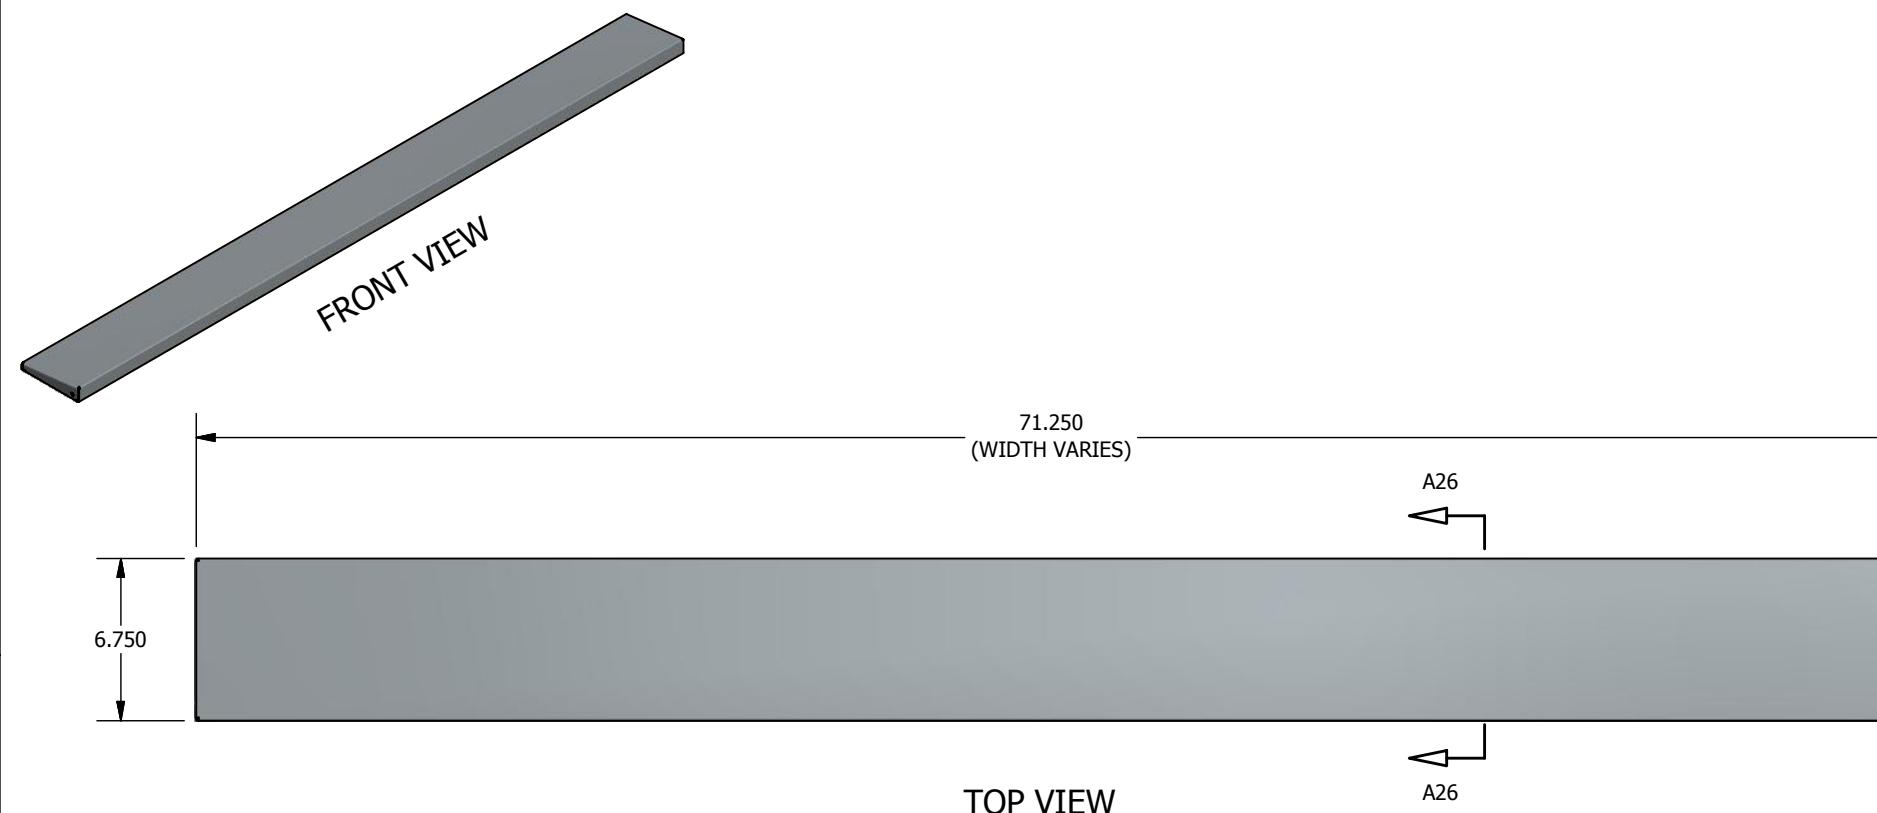

TOP VIEW

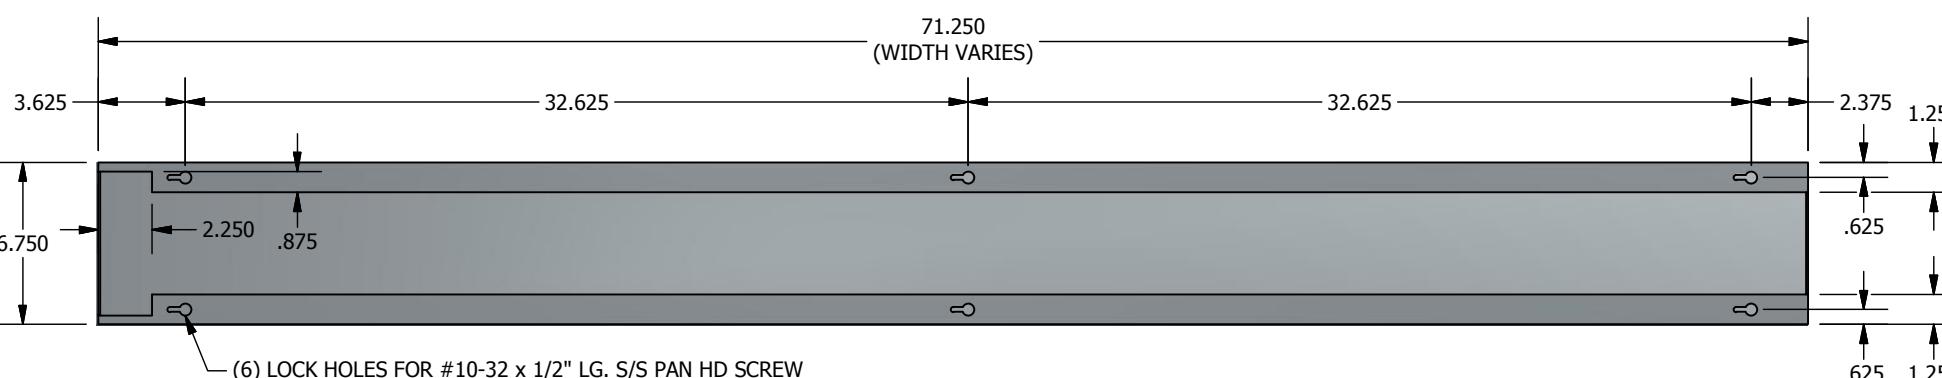

BOTTOM VIEW

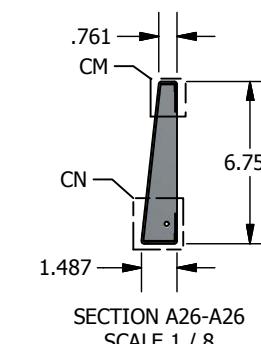

SECTION A26-A26  
SCALE 1 / 8



ARCHITECTURAL METAL FABRICATION  
59-20 56TH AVE.  
MASPETH, NY 11378  
(718) 894-1212

**CONTRACTOR**

325 KENT CONSTRUCTION LLC

**ARCHITECT**

ISMAEL LEYVA

**PROJECT #**

DOMINO SITE E

**ITEM**

FAÇADE

**DRAWING**

16001\_ZINC PANEL TYPES

**DRAWN CHECKED**

SP

PART TAG:	'RAILING/BALCONY CAP' PANELS: PANEL ID PER TABLE	ISSUE DATE	REVISION
QT:	(QTY) PER TABLE	7/28/2016	A
MATERIAL:	2.00MM ZINC		
FINISH:	ZINC - NATURAL; ALUM. - BLACK ANOD.		
FLAT FILE:		(AS SHOWN)	35 / 37




8 7 6 5 4 3 2 1

8 7 6 5 4 3 2 1

PANEL ID	PANEL TYPE	BEND PROFILE	WIDTH (IN)	HEIGHT (IN)	PANEL TYPE (QTY)
Z06A-1-000	RAILING	TYPE 4B_CL	73.625	6.750	1
PANEL TOTAL					1

\*RAILNG CAP PANEL AT CORNER HOLDS FOR FURTHER COORDINATION

FRONT VIEW

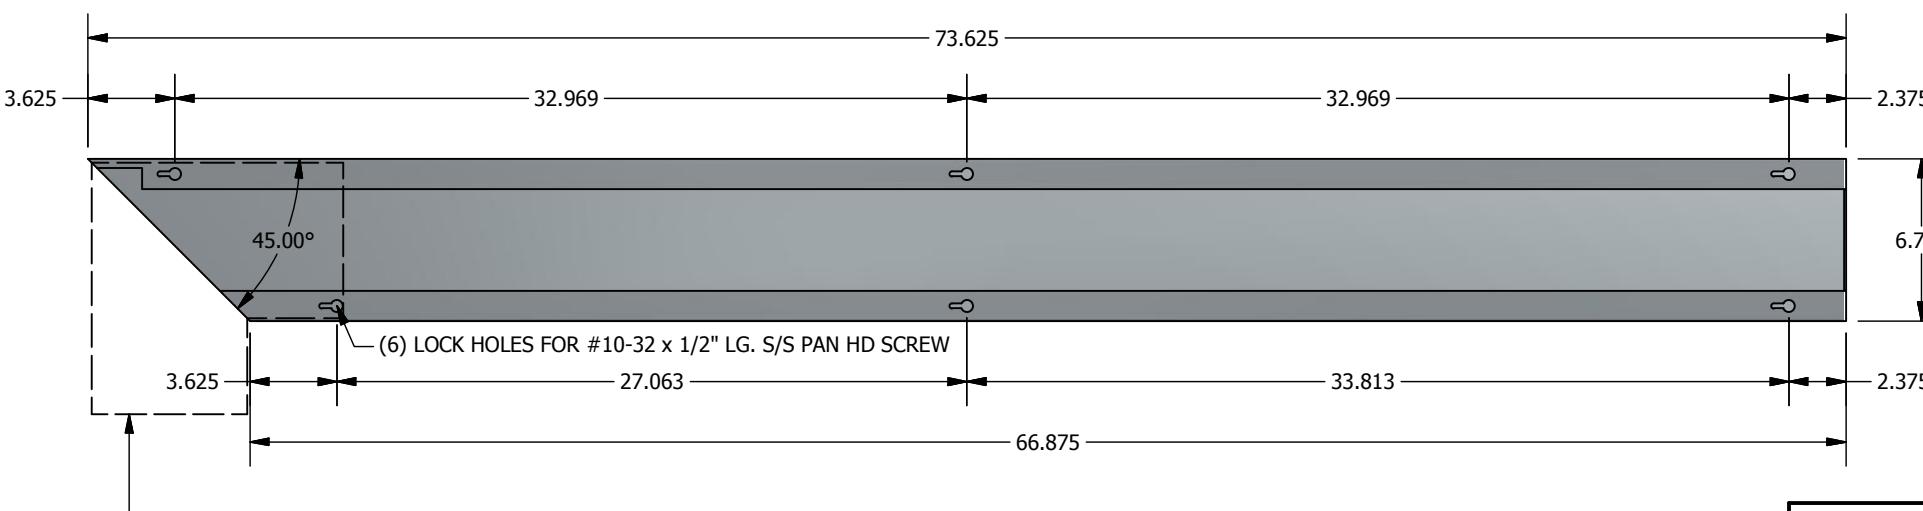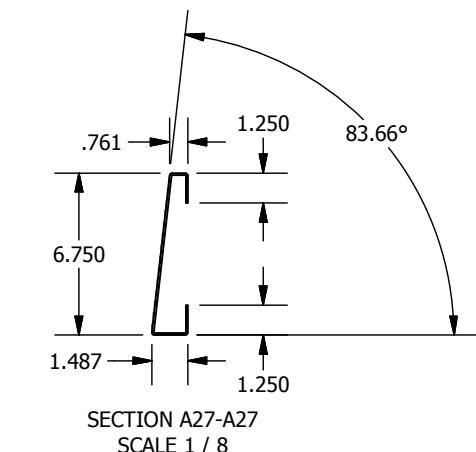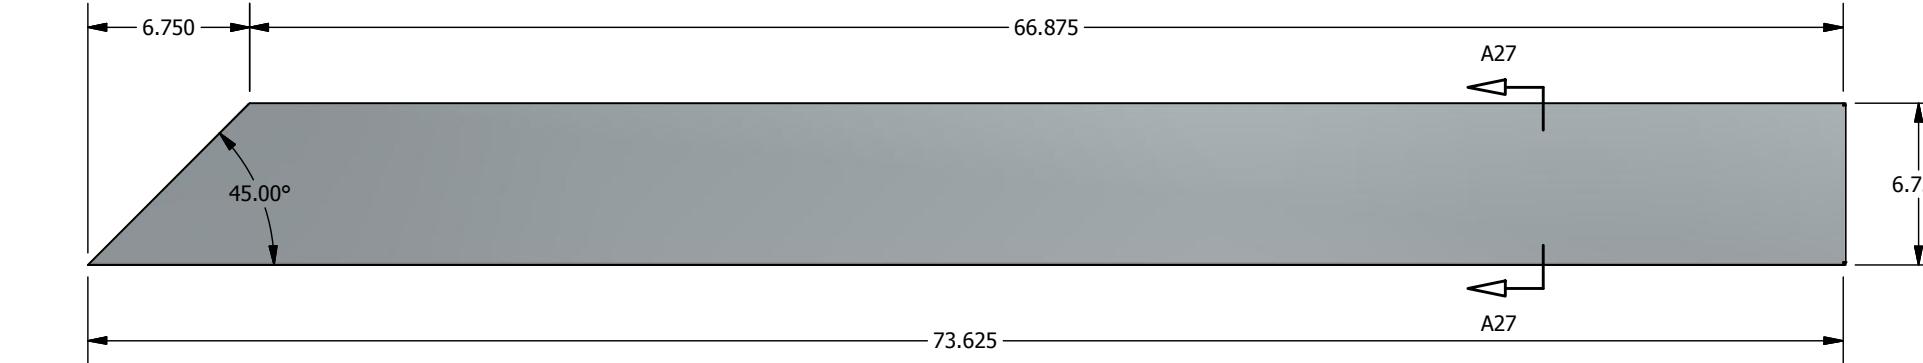

PART TAG:	CORNER LEFT 'RAILING CAP' PANELS: PANEL ID PER TABLE
QT:	(QTY) PER TABLE
MATERIAL:	2.00MM ZINC
FINISH:	ZINC - NATURAL; ALUM. - BLACK ANOD.
FLAT FILE:	(AS SHOWN)


**HI TECH**  
ARCHITECTURAL METAL FABRICATION  
59-20 56TH AVE.  
MASPETH, NY 11378  
(718) 894-1212

CONTRACTOR	325 KENT CONSTRUCTION LLC
ARCHITECT	ISMAEL LEYVA
PROJECT #	DOMINO SITE E
ITEM	FACADE
DRAWING	16001_ZINC PANEL TYPES
DRAWN	SP
CHECKED	
ISSUE DATE	7/28/2016
REVISION	A
SCALE	1 / 8
SHEET NUMBER	36 / 37



8 7 6 5 4 3 2 1

PANEL ID	PANEL TYPE	BEND PROFILE	WIDTH (IN)	HEIGHT (IN)	PANEL TYPE (QTY)
Z06A-1-005	RAILING	TYPE 4B_CR	73.625	6.750	1
TOTAL PANEL					1


\*RAILING CAP PANEL AT CORNER HOLDS FOR FURTHER COORDINATION

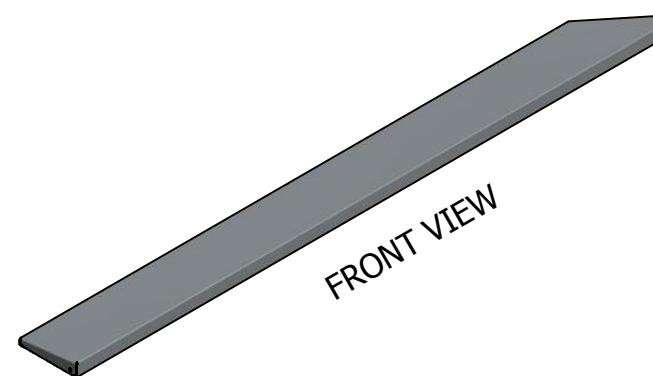

FRONT VIEW

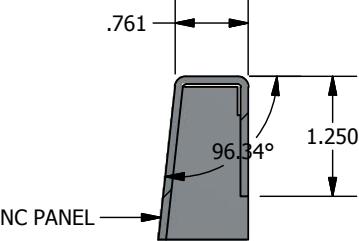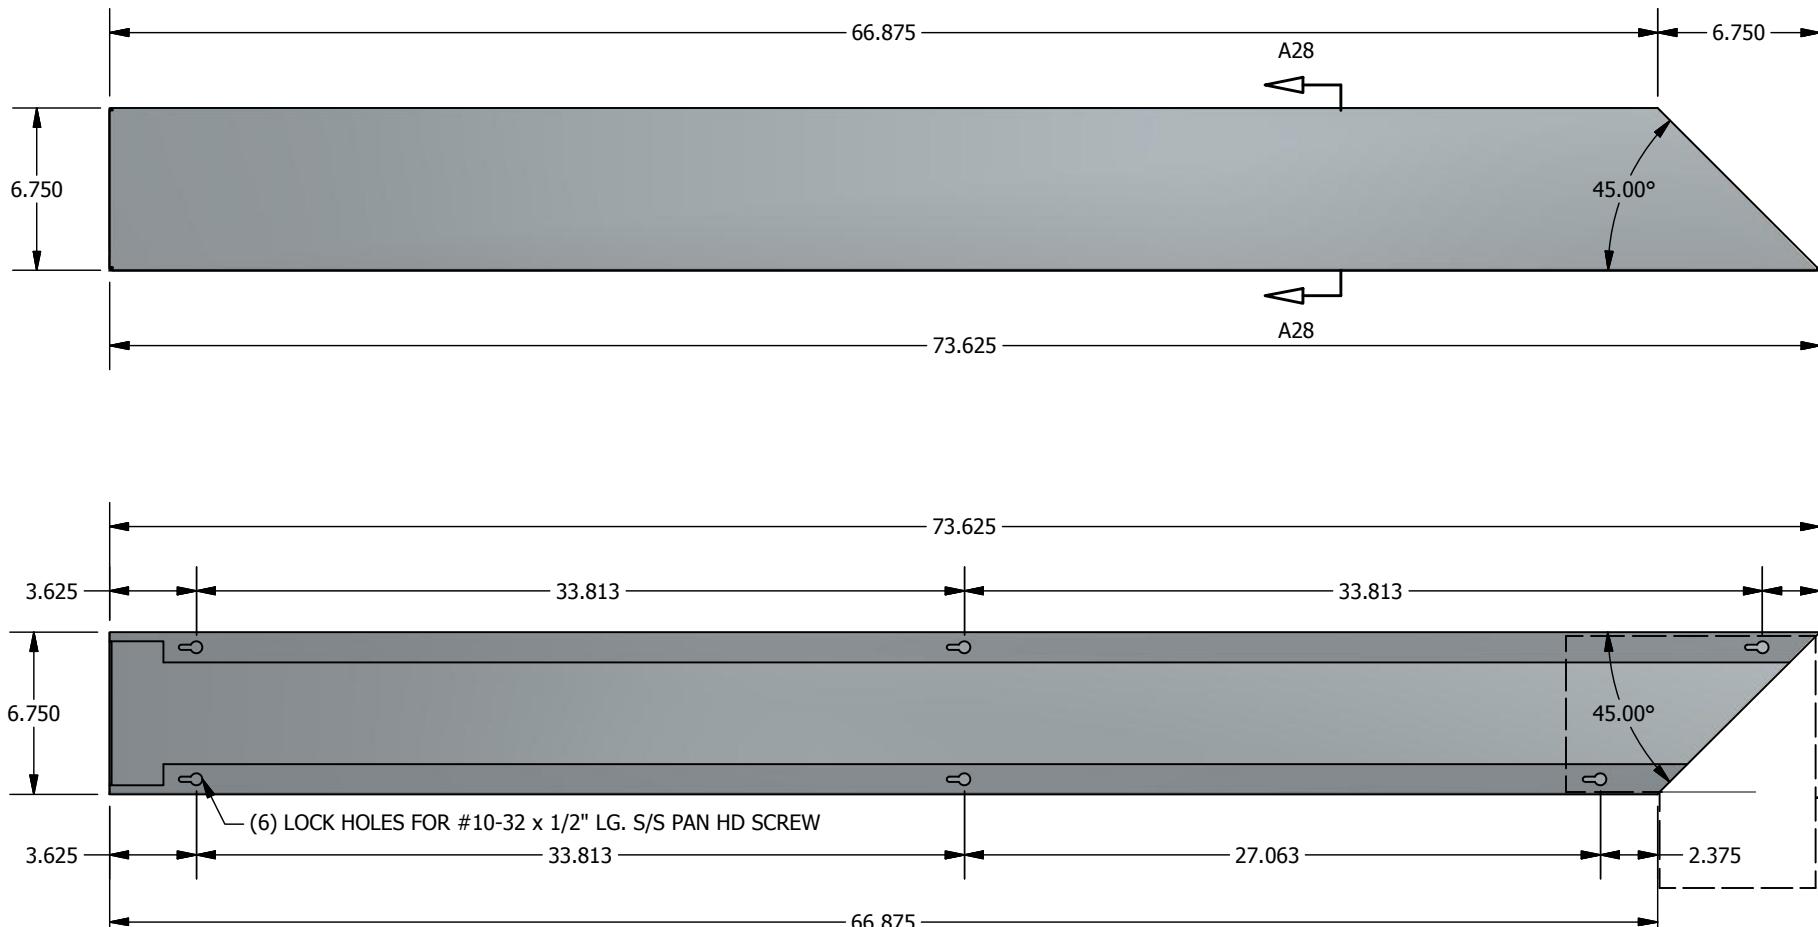


DETAIL CP  
SCALE 1 / 2

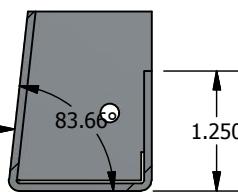

2.00MM THK. ZINC PANFL

DETAIL CR  
SCALE 1 / 2

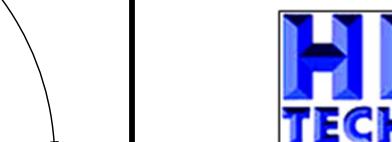

ARCHITECTURAL METAL FABRICATION  
59-20 56TH AVE.  
MASPETH, NY 11378  
(718) 844-1312

---

**CONTRACTOR**

325 KENT CONSTRUCTION LLC

---

ARCHITECT

ISMAEL LEYVA

PROJECT

DOMINO SITE E

ITEM

FACADE

## DRAWING

## 16001\_ZINC PANEL TYPES

DRAWN

PART TAG:	CORNER RIGHT 'RAILING CAP' PANELS: PANEL ID PER TABLE	ISSUE DATE	REVISION
QT:	(QTY) PER TABLE	7/28/2016	A
MATERIAL:	2.00MM ZINC	SCALE	SHEET NUMBER
FINISH:	ZINC - NATURAL; ALUM. - BLACK ANOD.		
FLAT FILE:		(AS SHOWN)	37 / 37